


Альбом чертежей

Exemplu

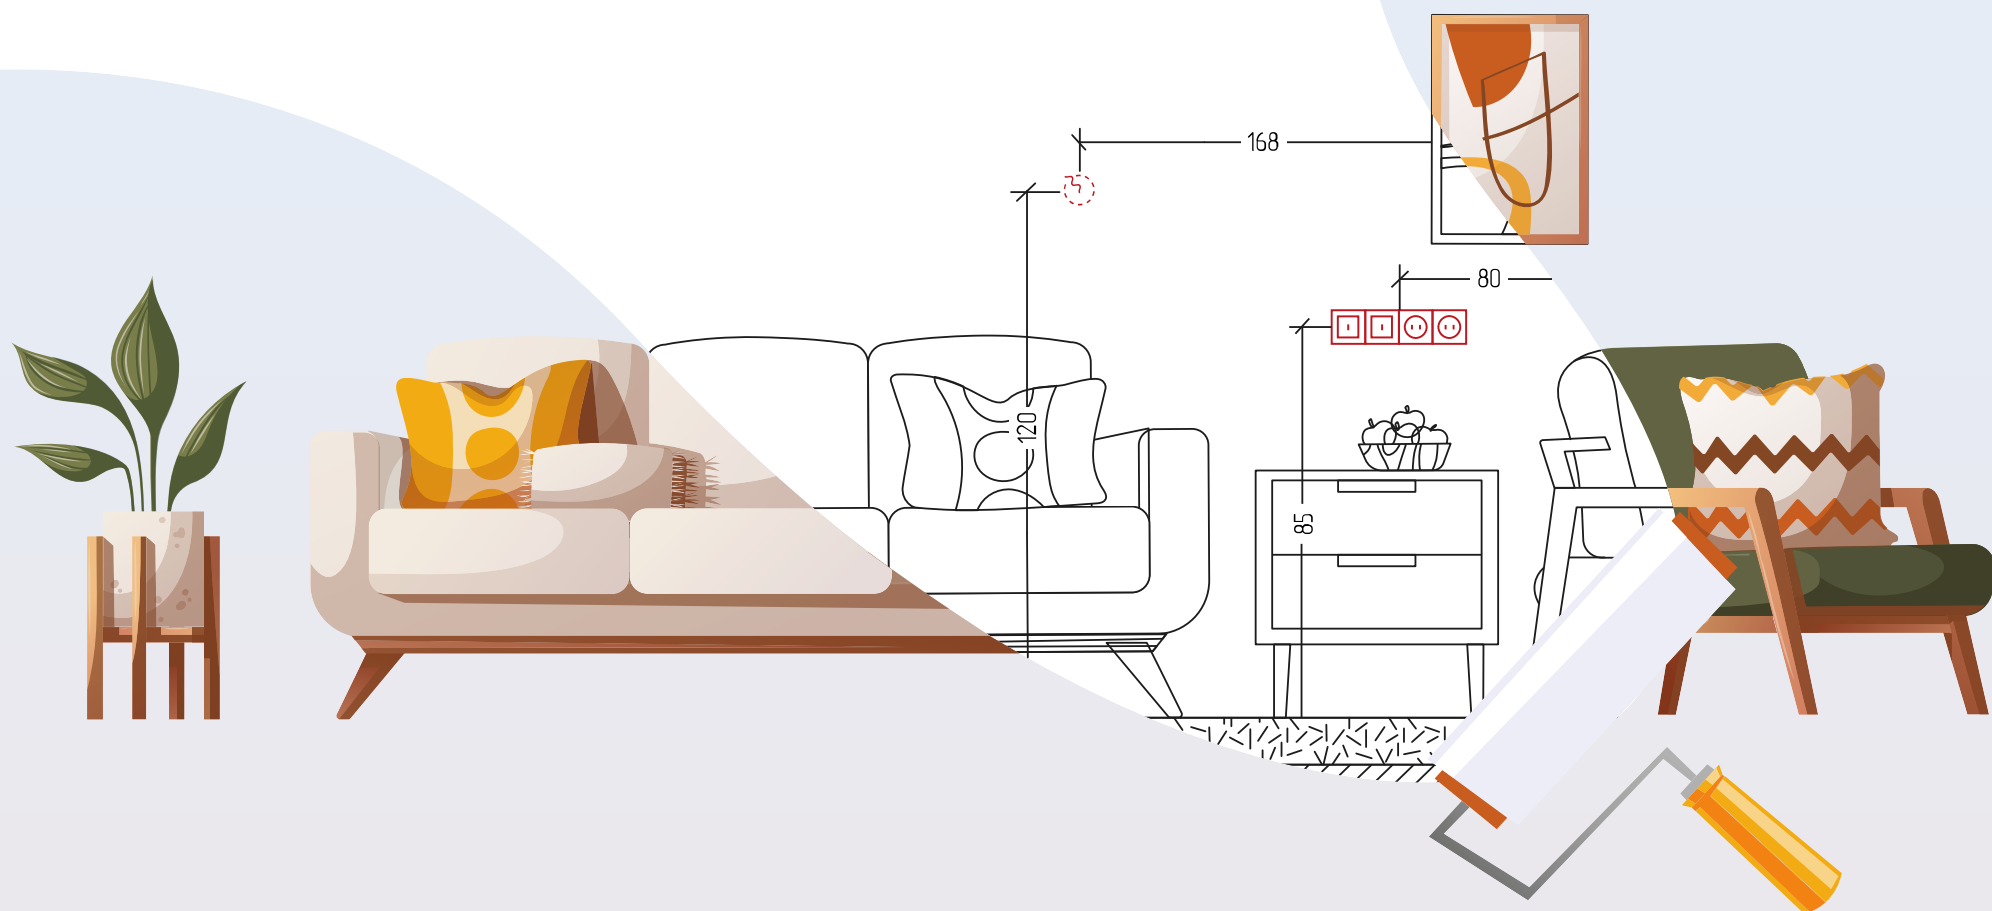


Efrosi E. FlamasteR SRL 079044935, 2026

Исходный план

Условные обозначения:


- Материал: блоки
- Сантехнический стояк
- Потолочный ригель

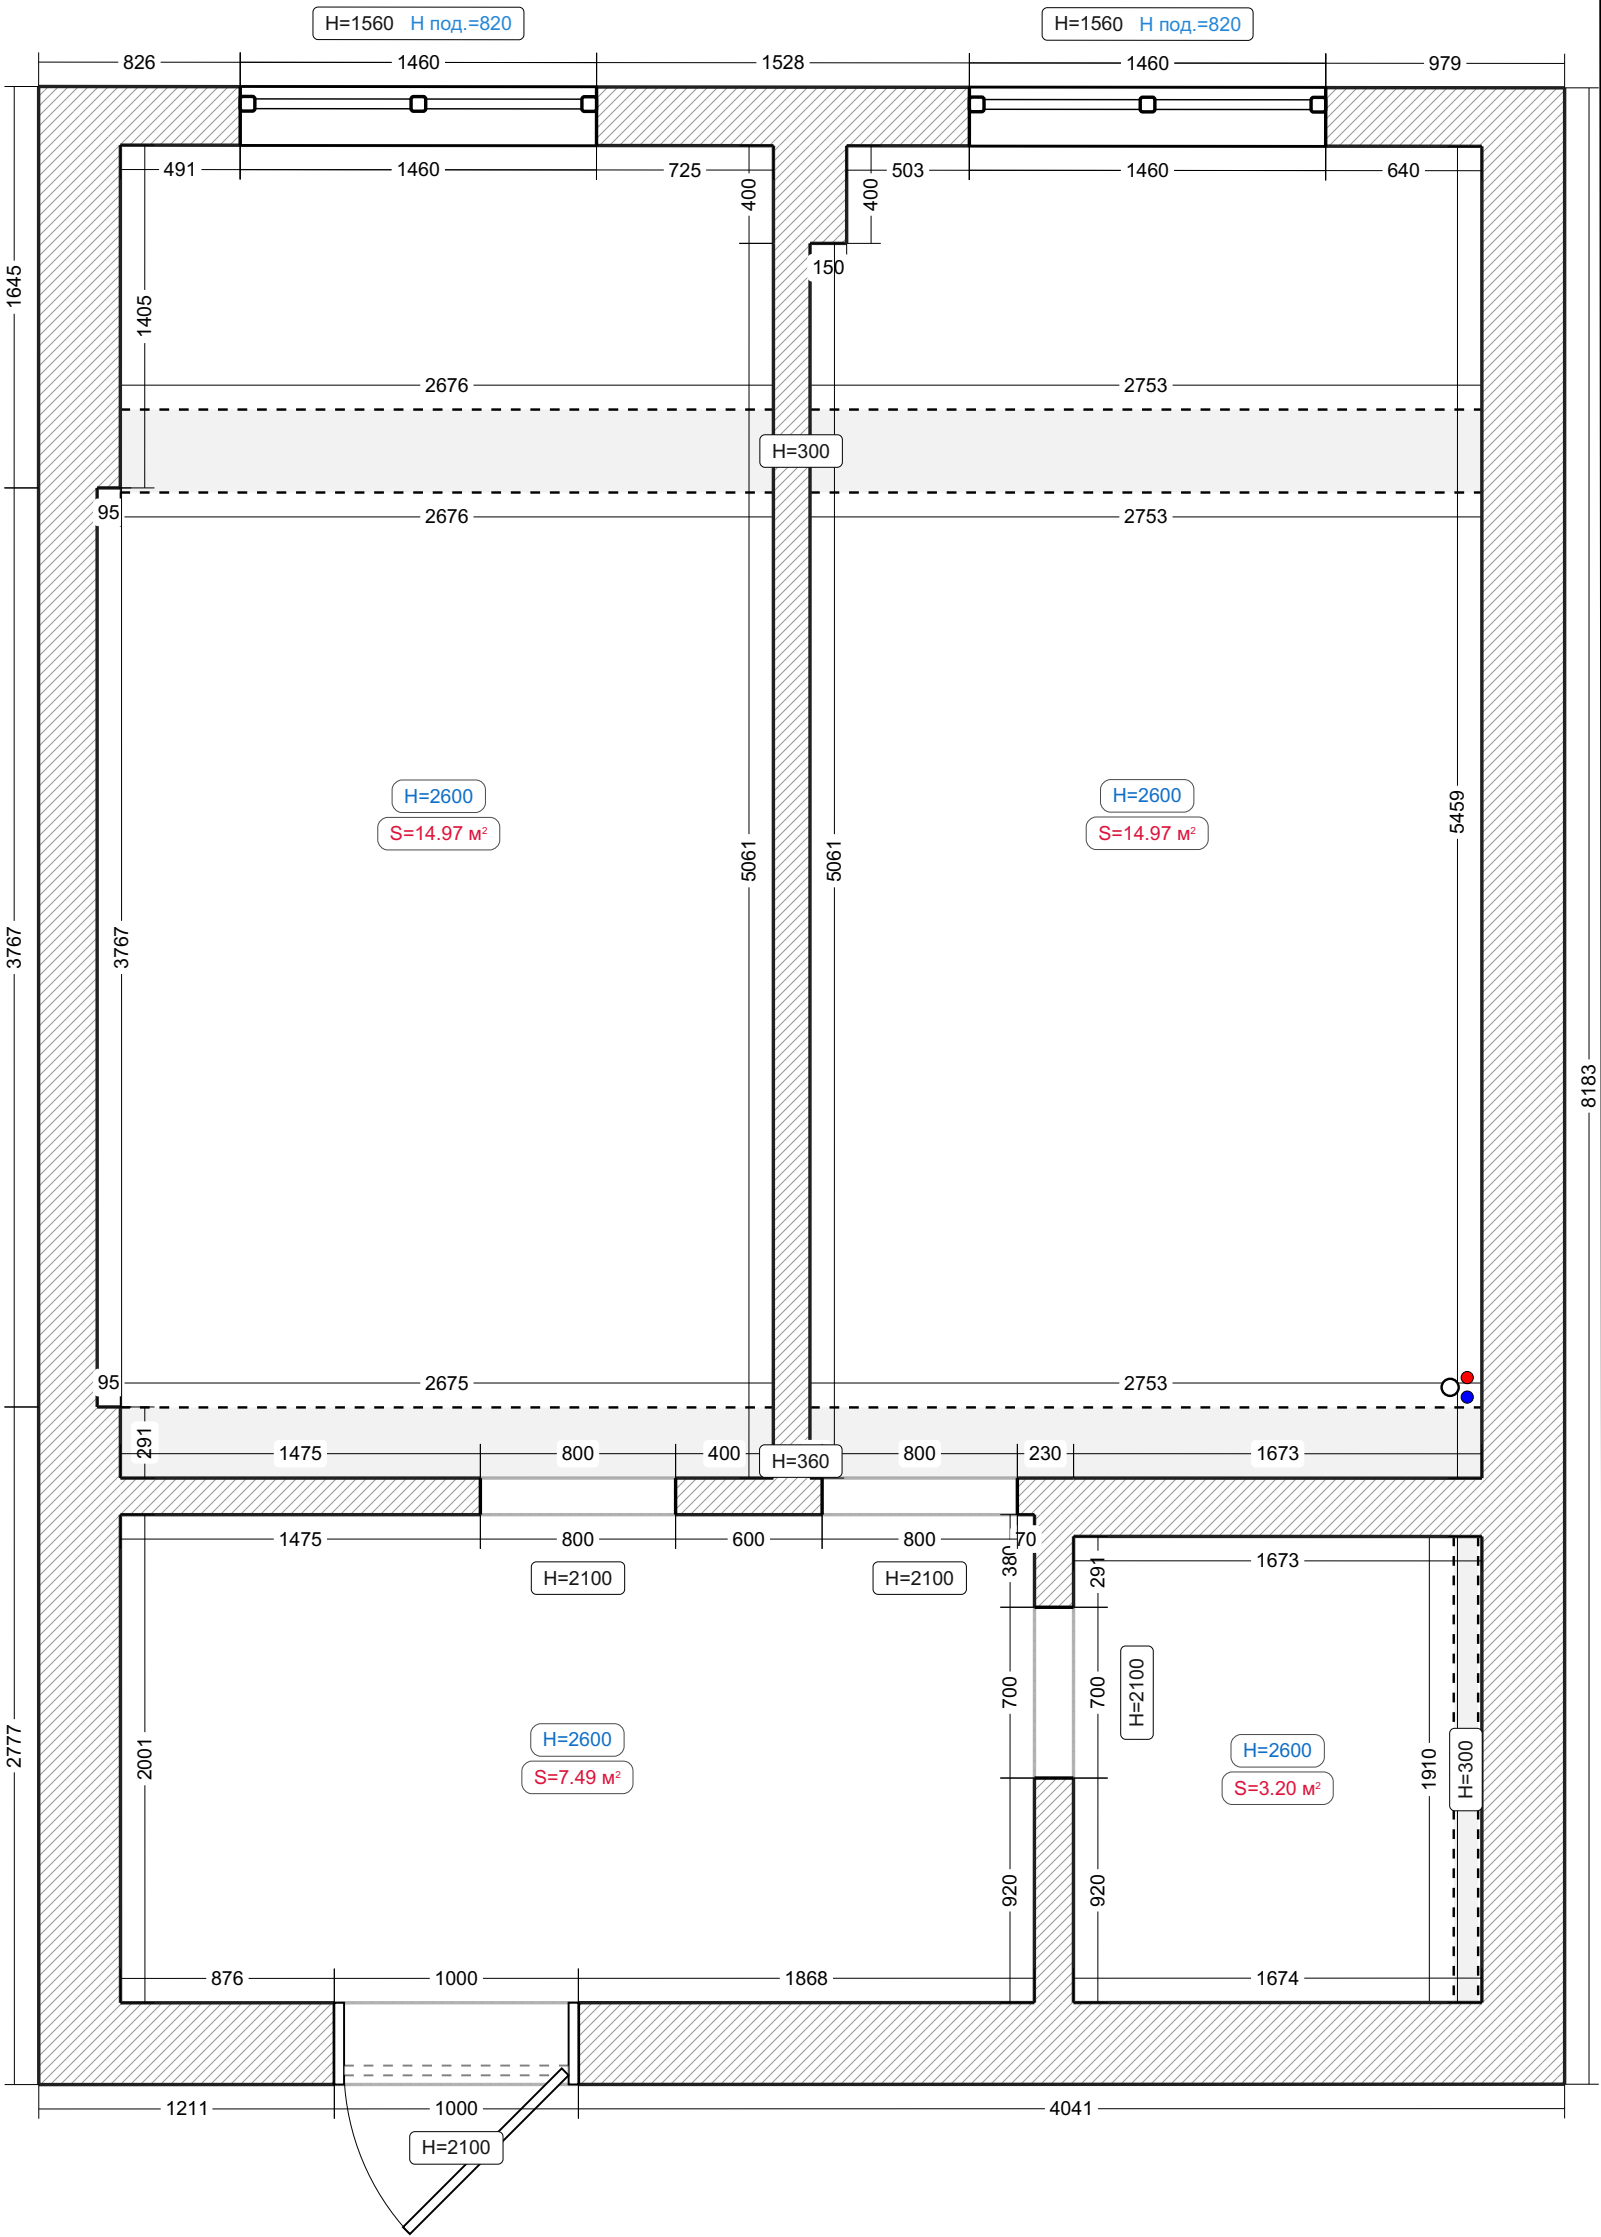


Перегородки

Условные обозначения:

- Стеклокартонная стена
- Стекло. перегородка
- Гипсокартонный короб

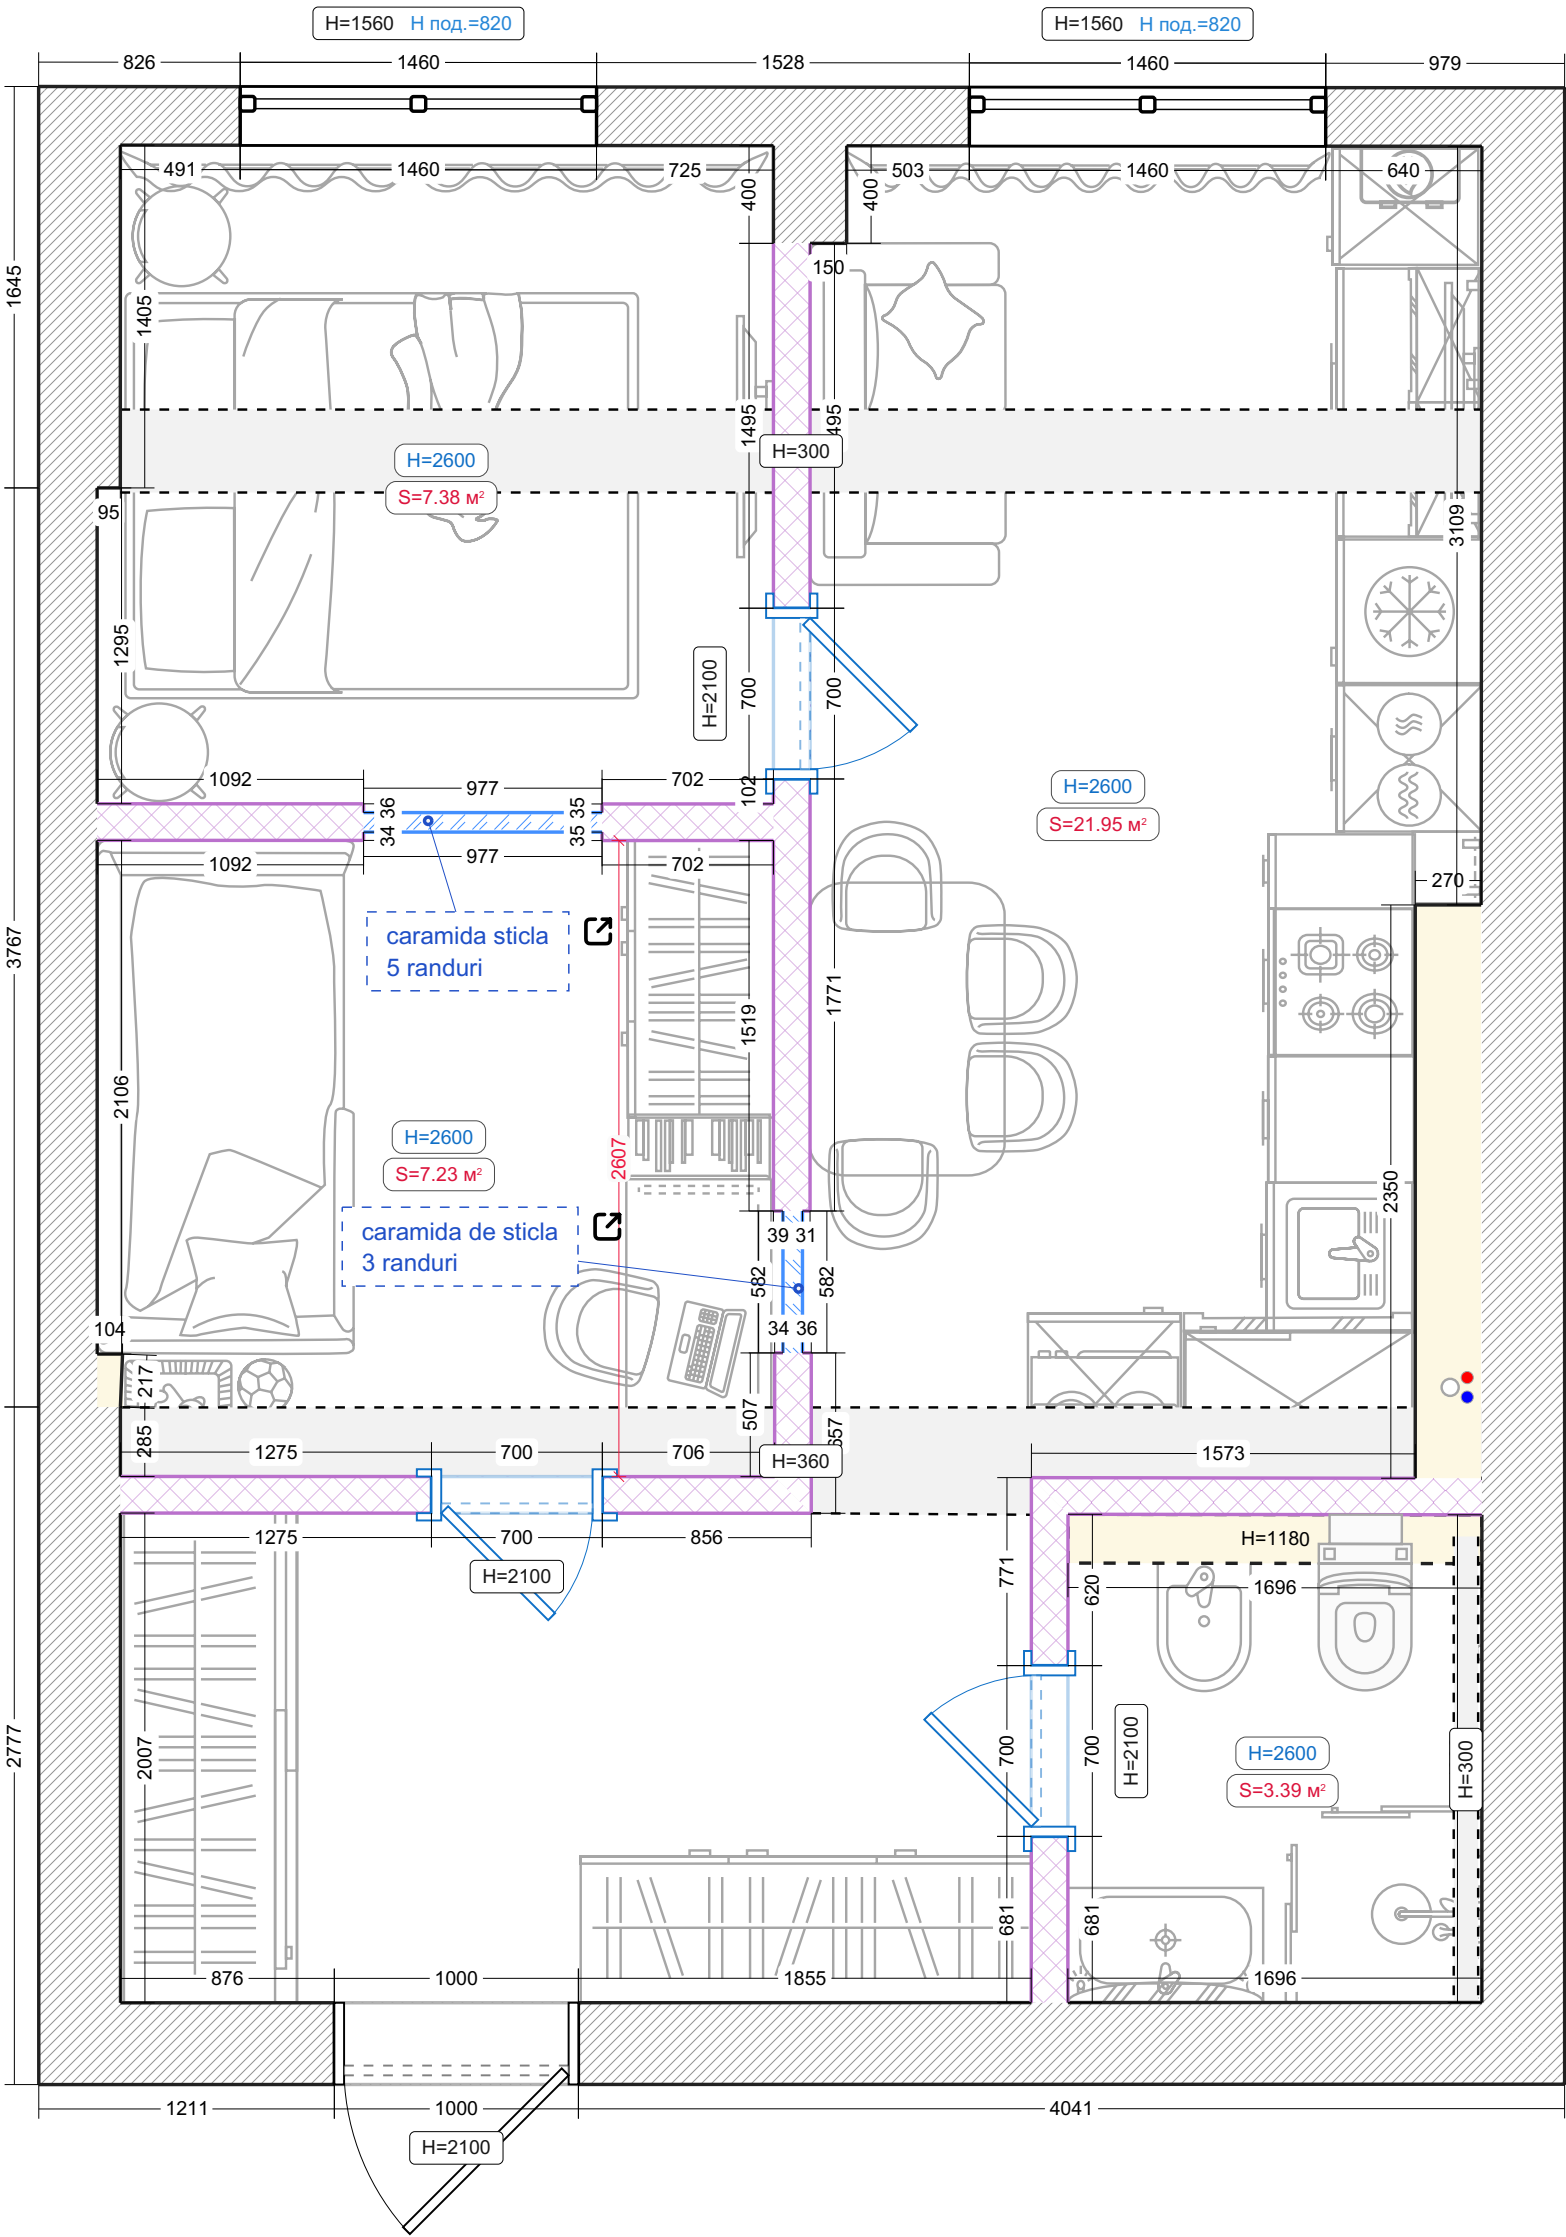



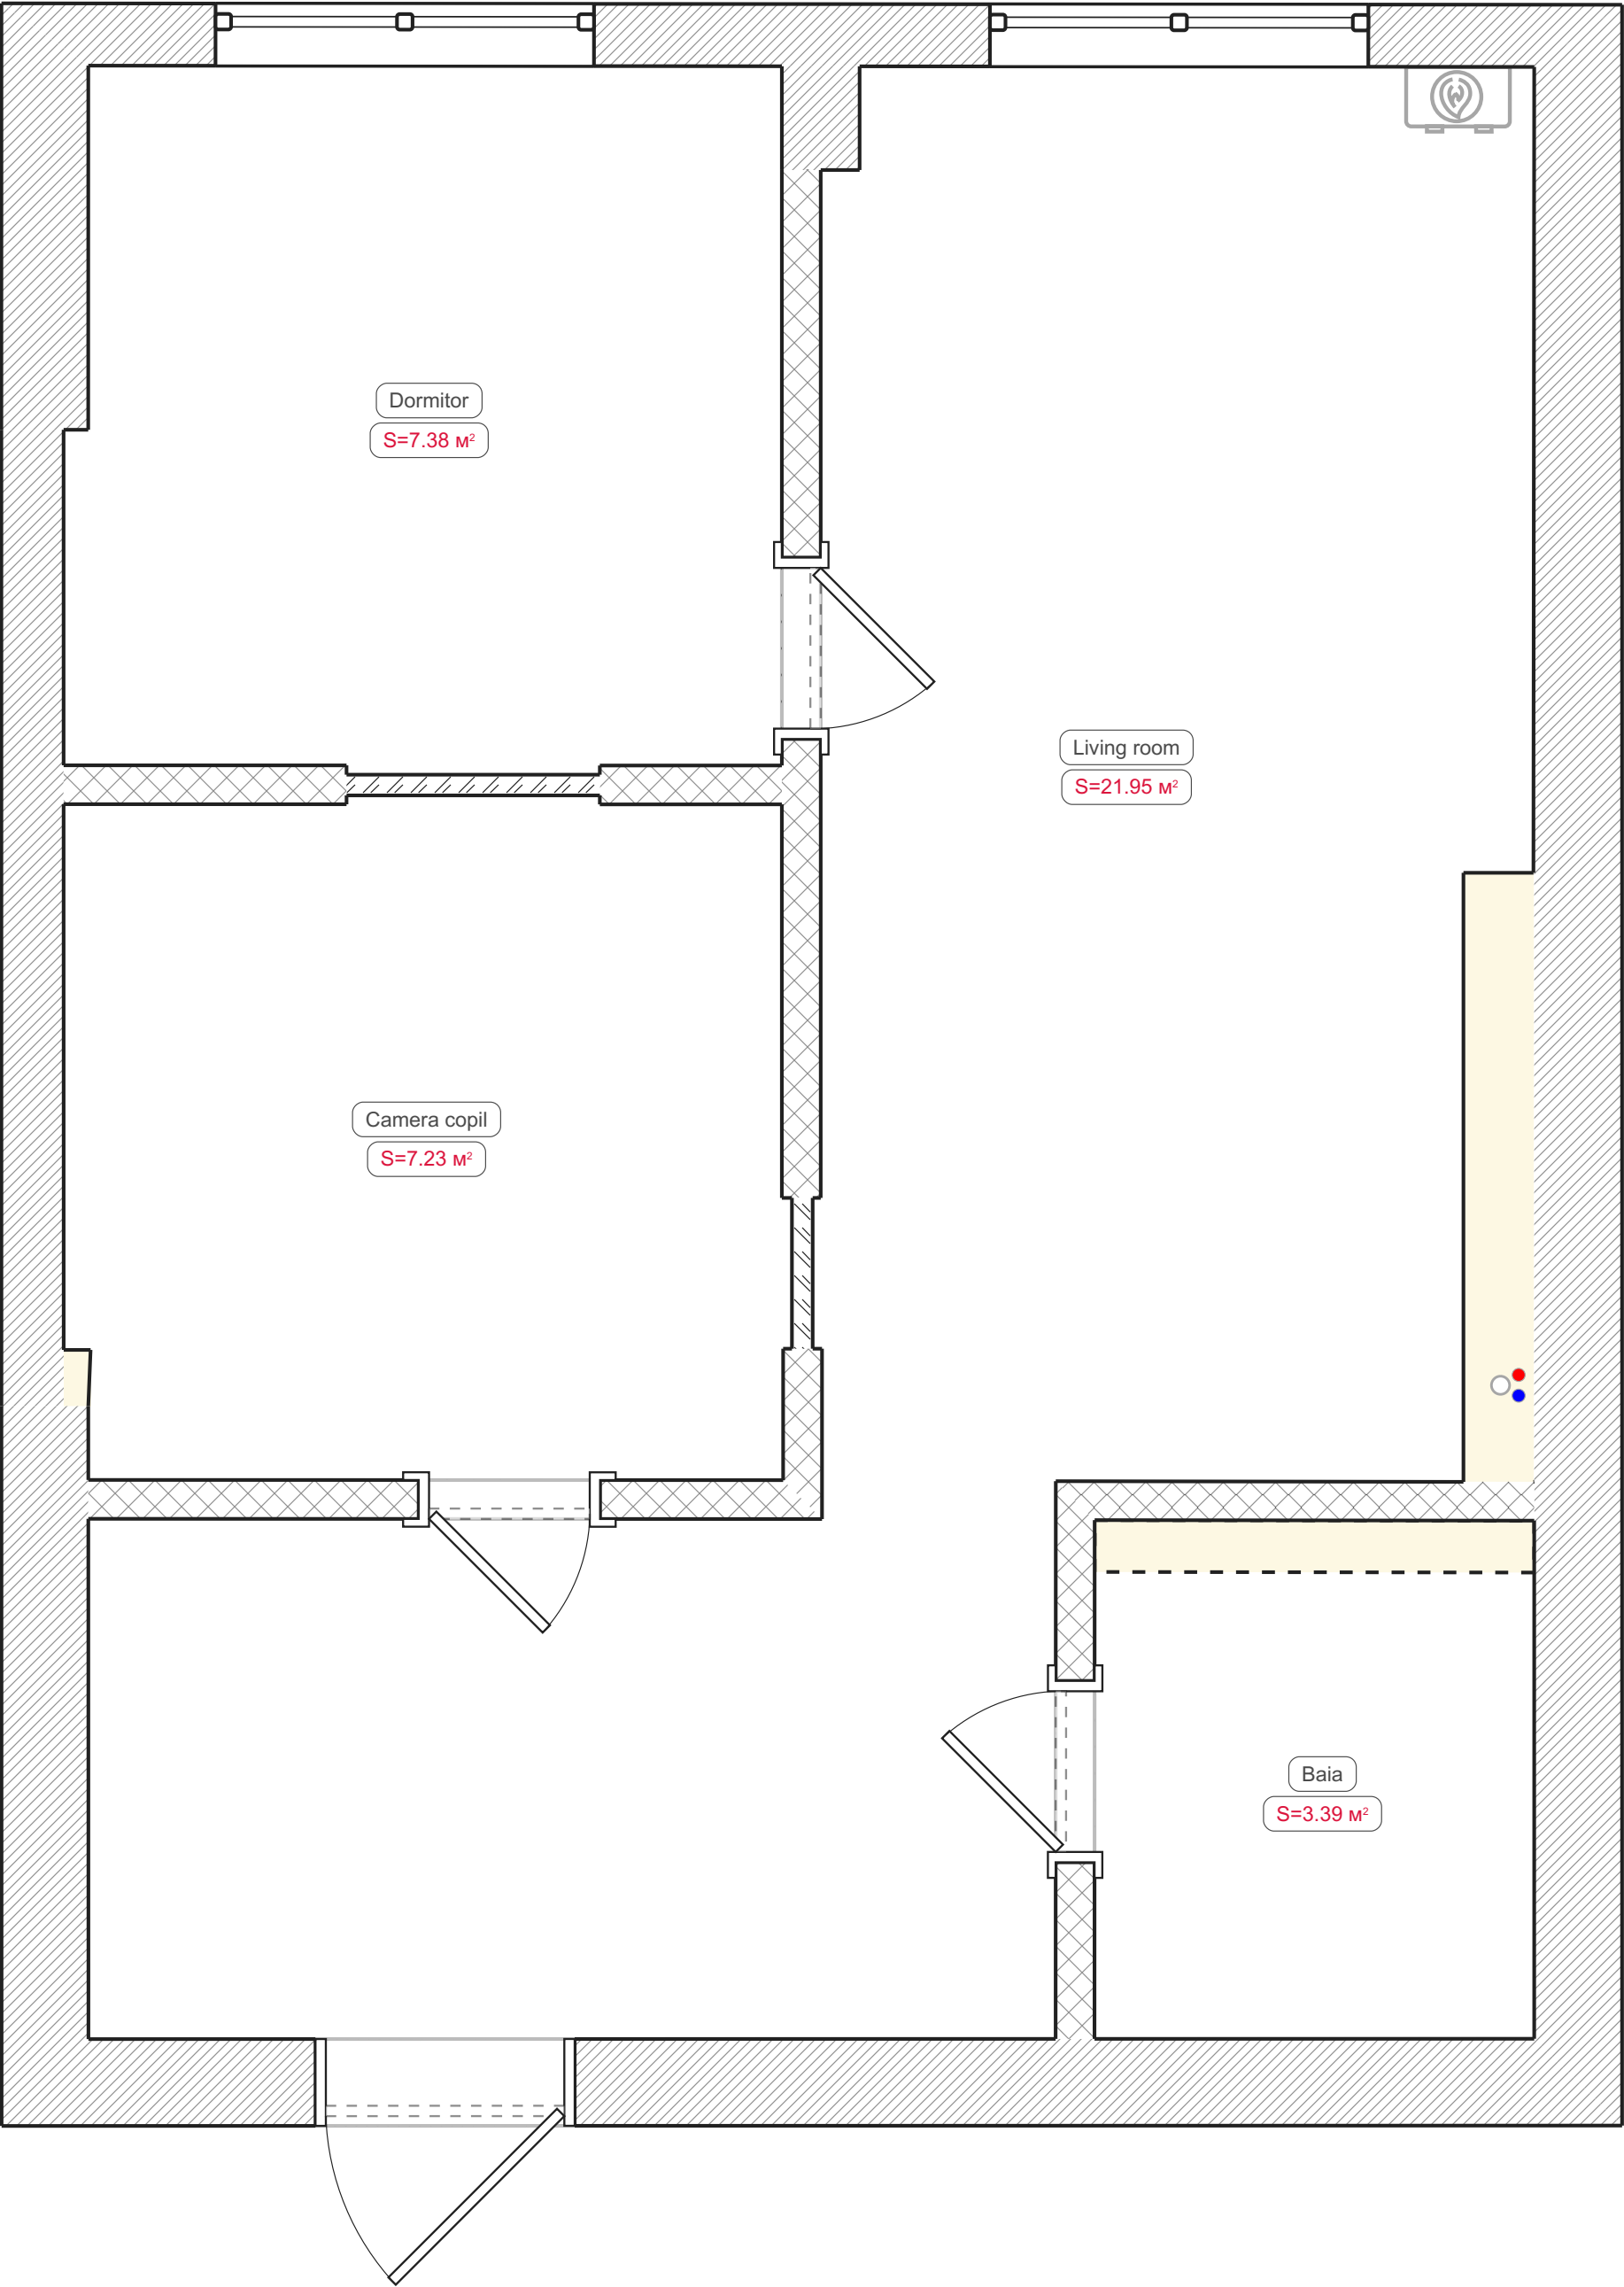



Радиаторы

Условные обозначения:

 Радиатор панельный

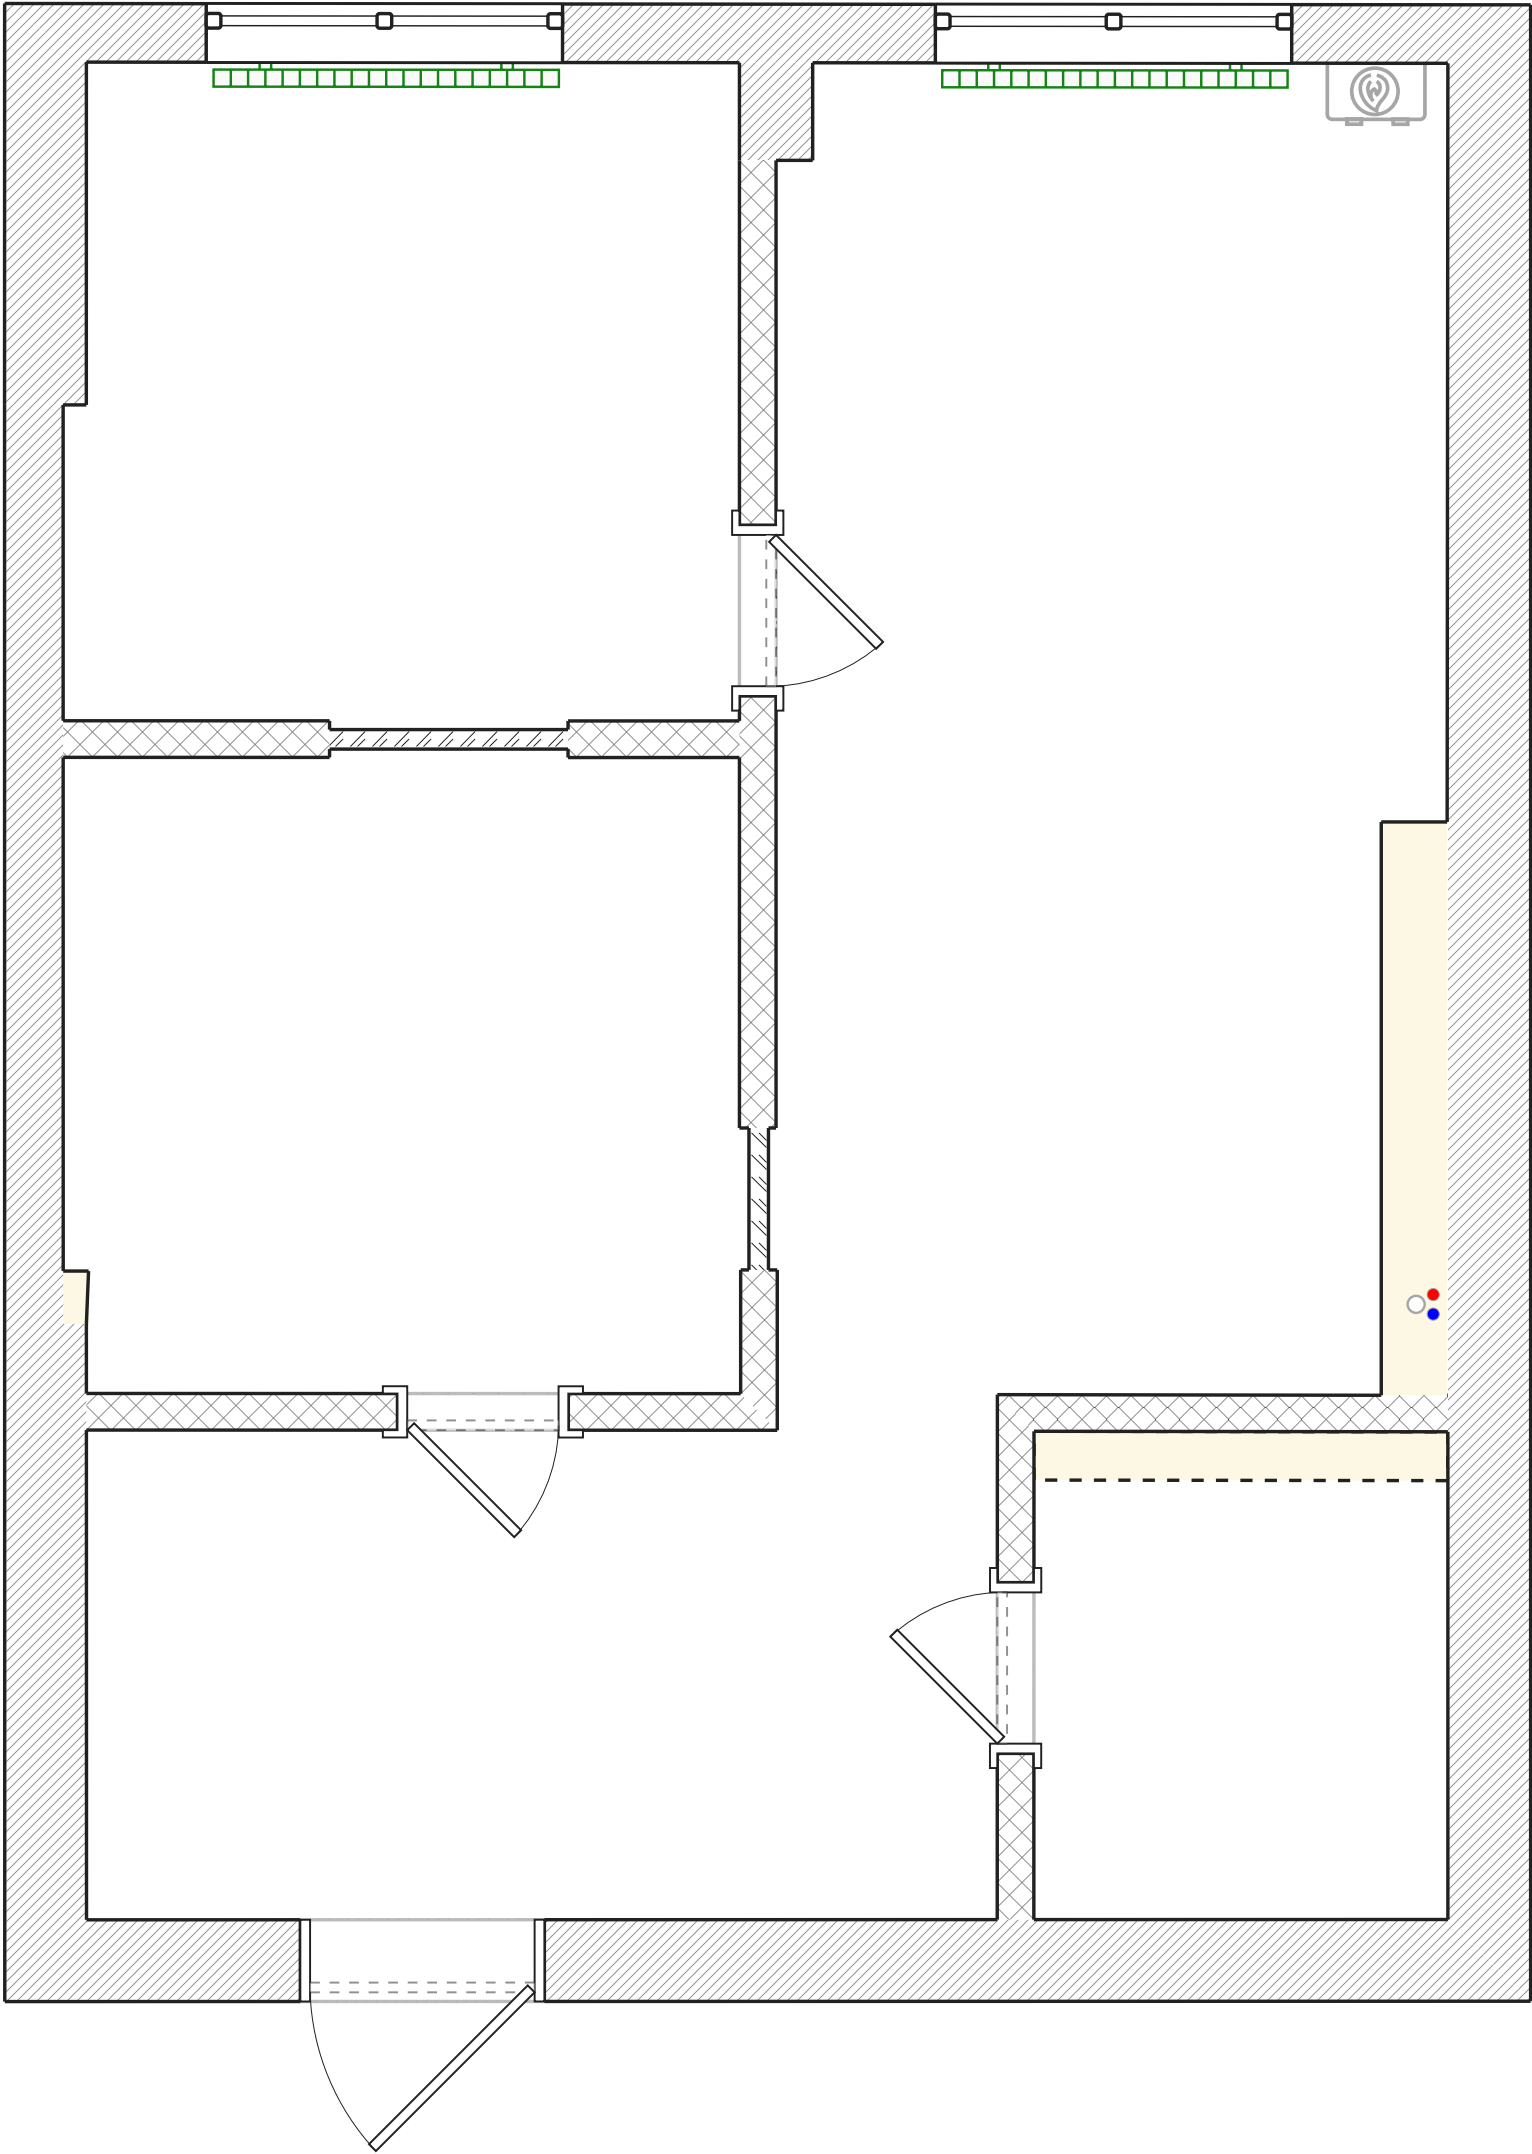

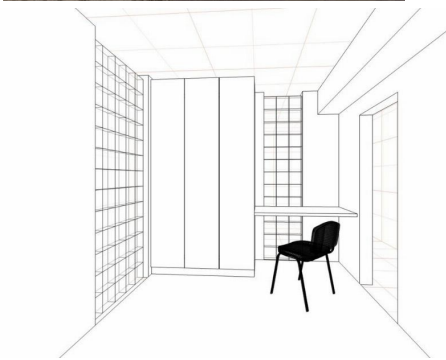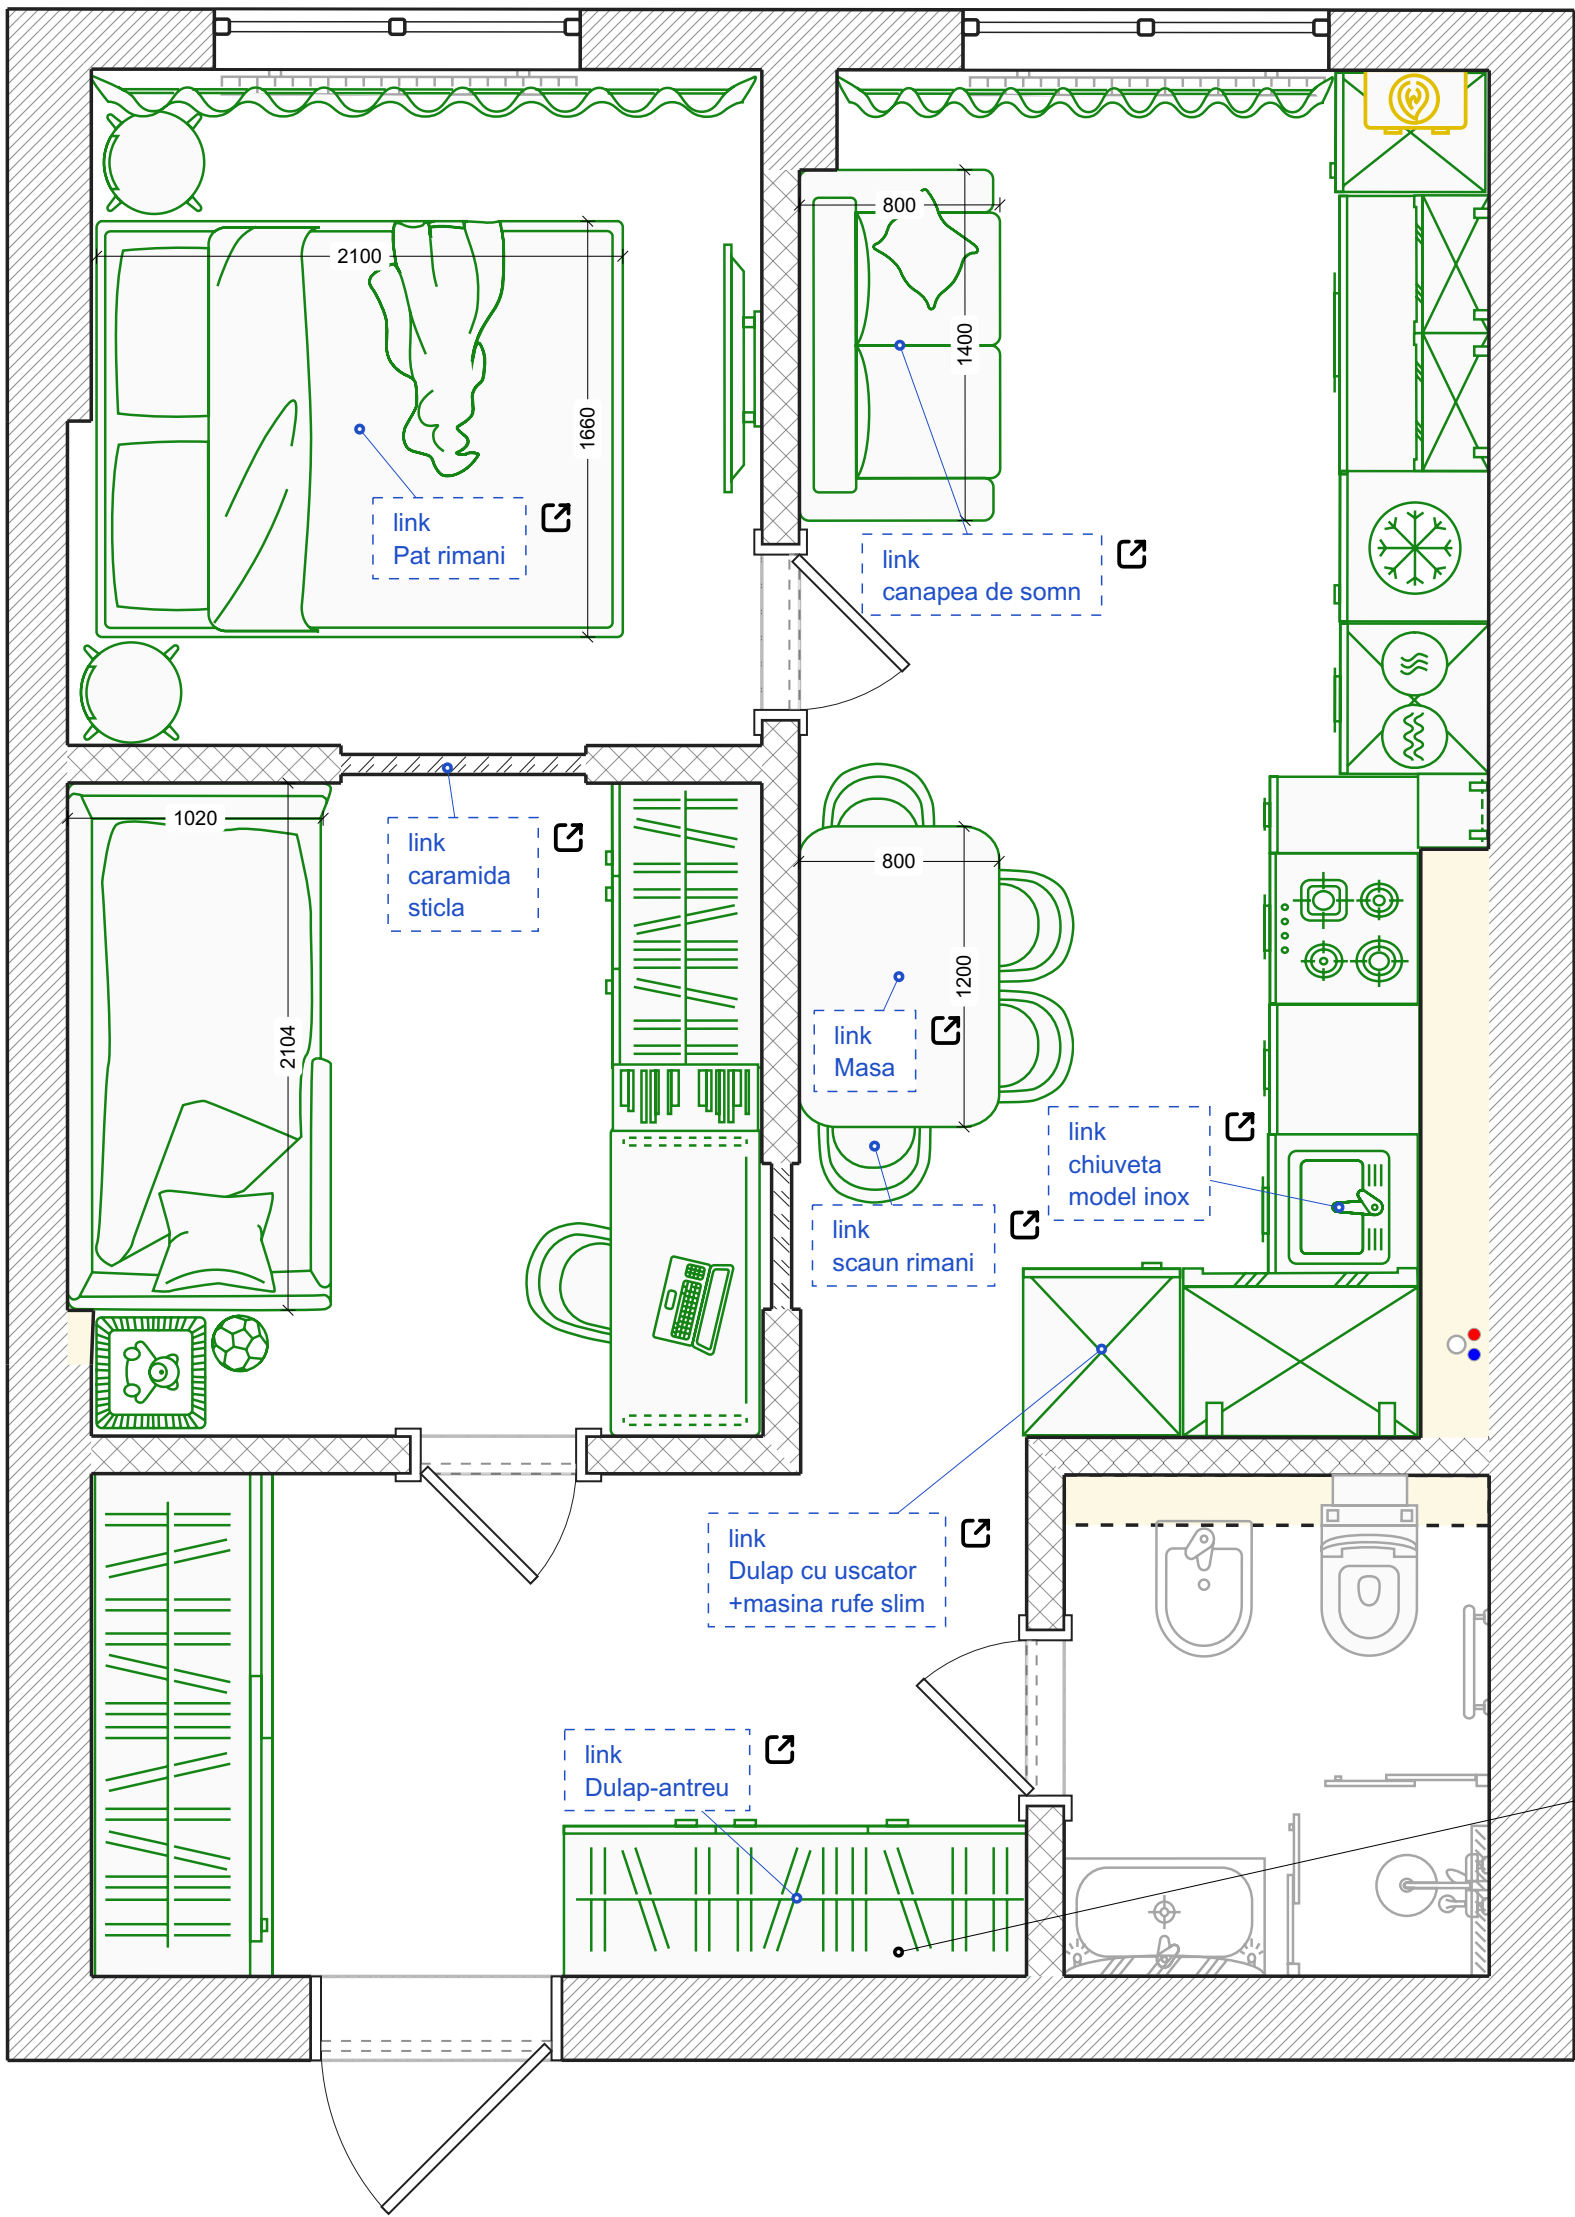


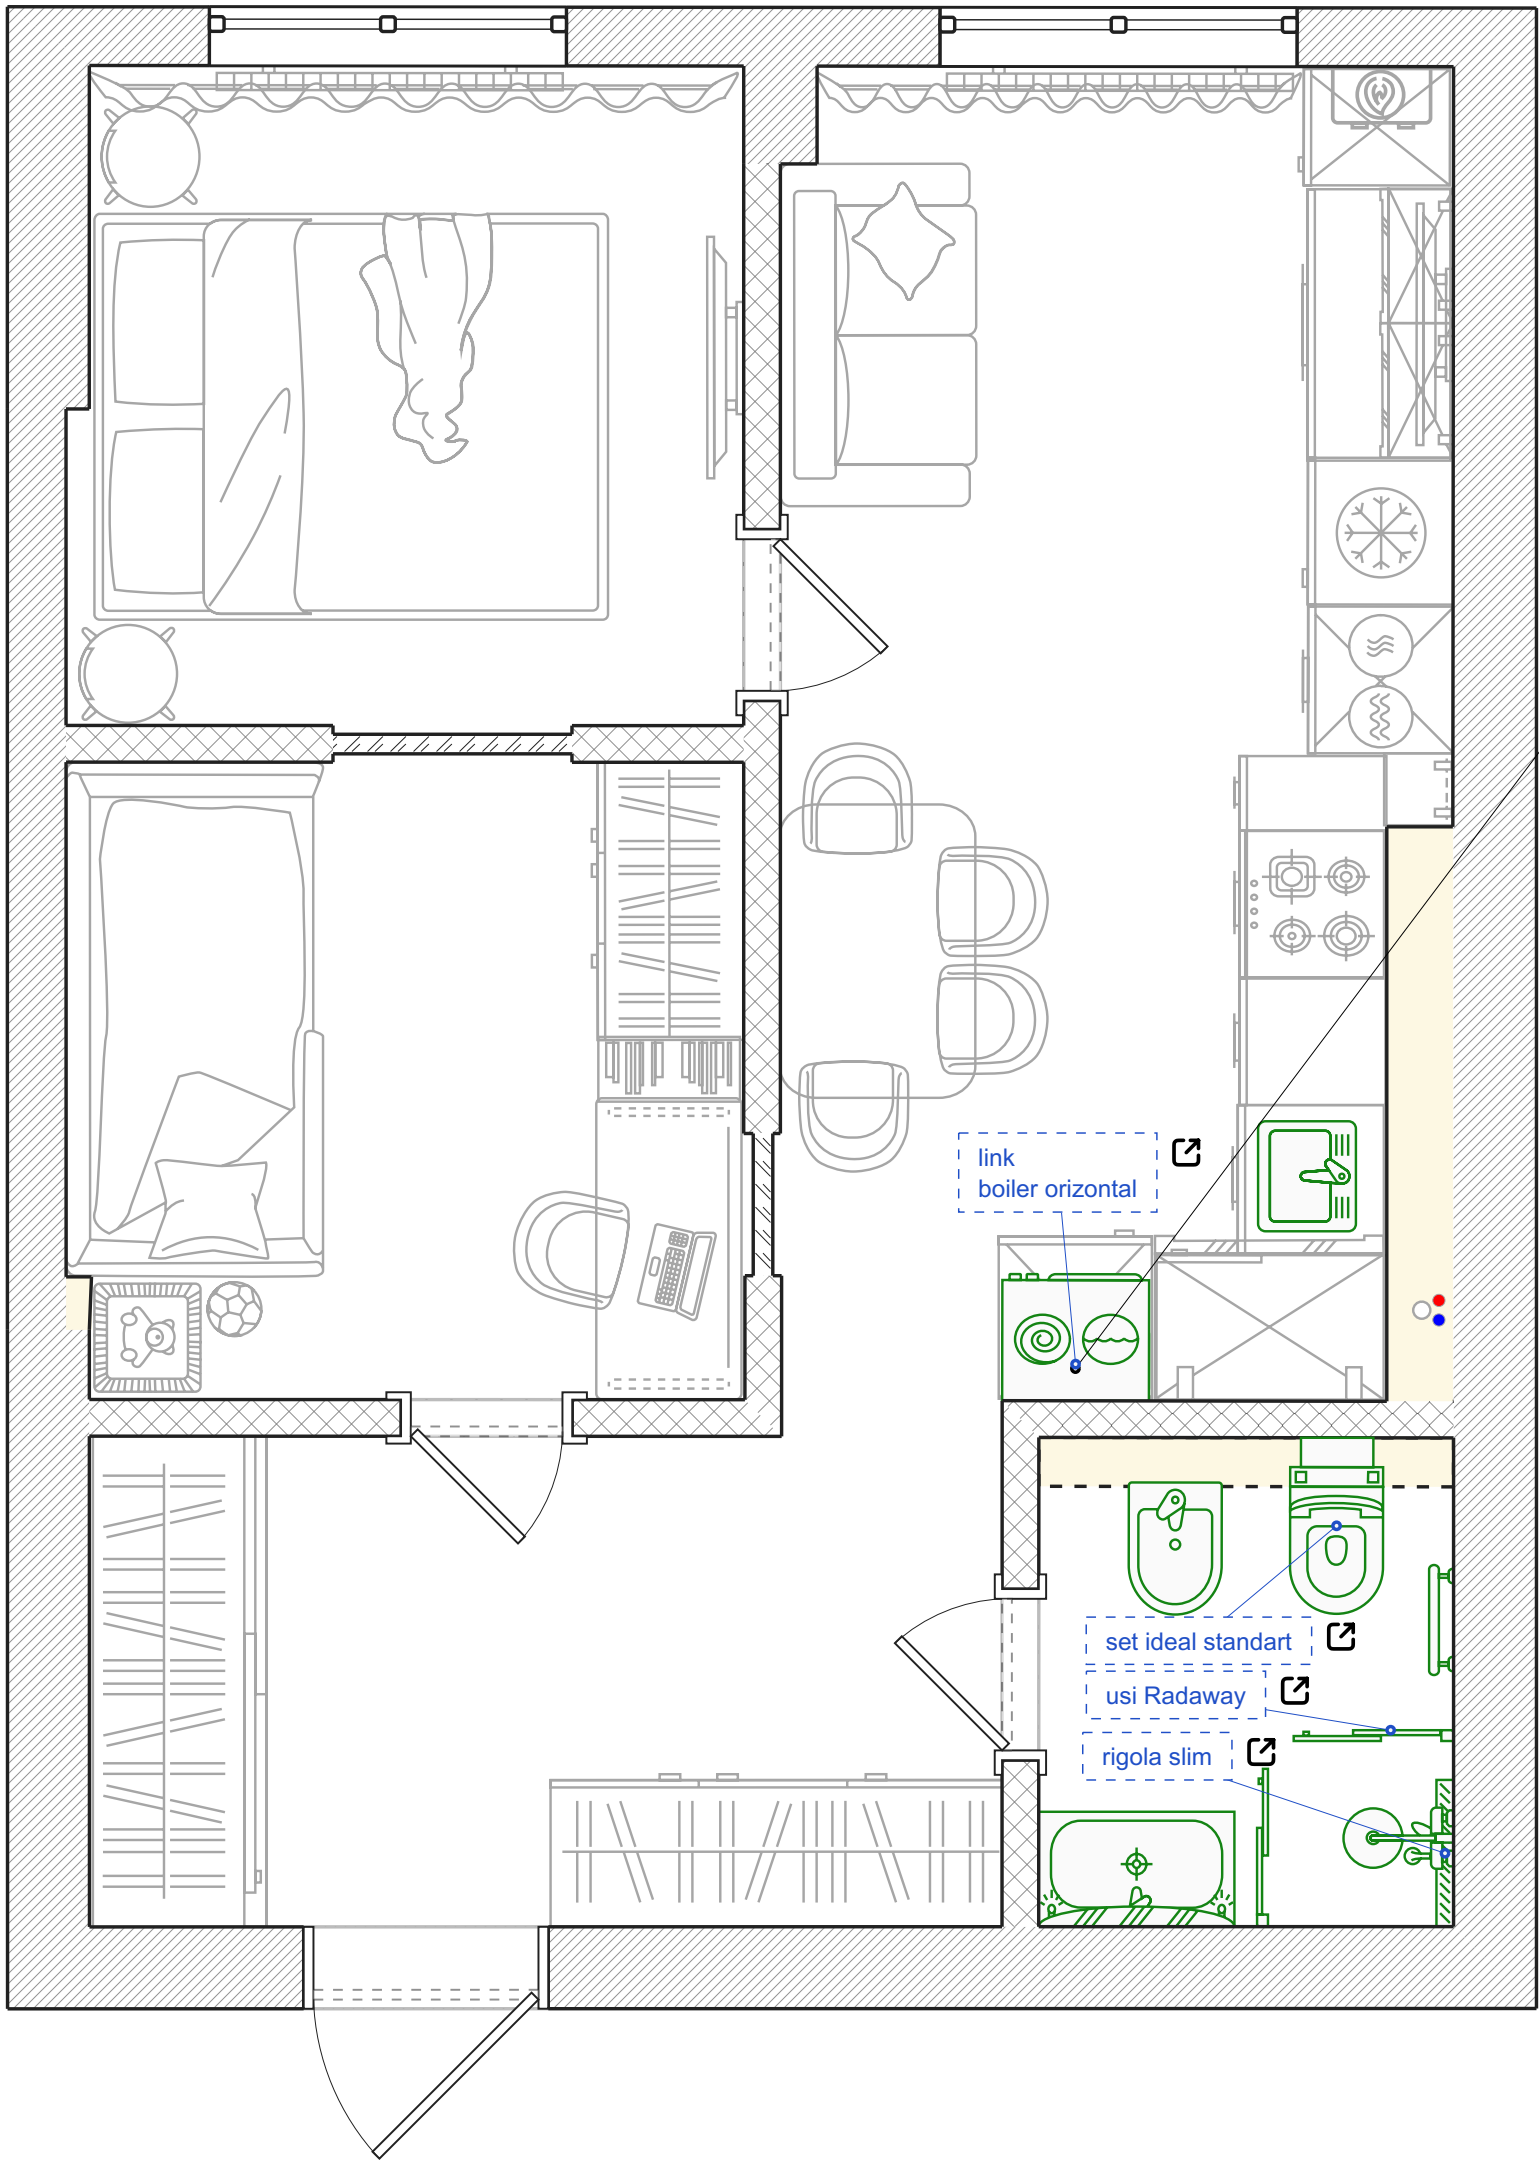



Водоснабжение

Условные обозначения:

- Вывод холодной воды
- Вывод горячей воды
- Вывод канализации
- ☒ Коллекторный узел
- Водопроводная труба ХВС
- Водопроводная труба ГВС
- Канализационная труба

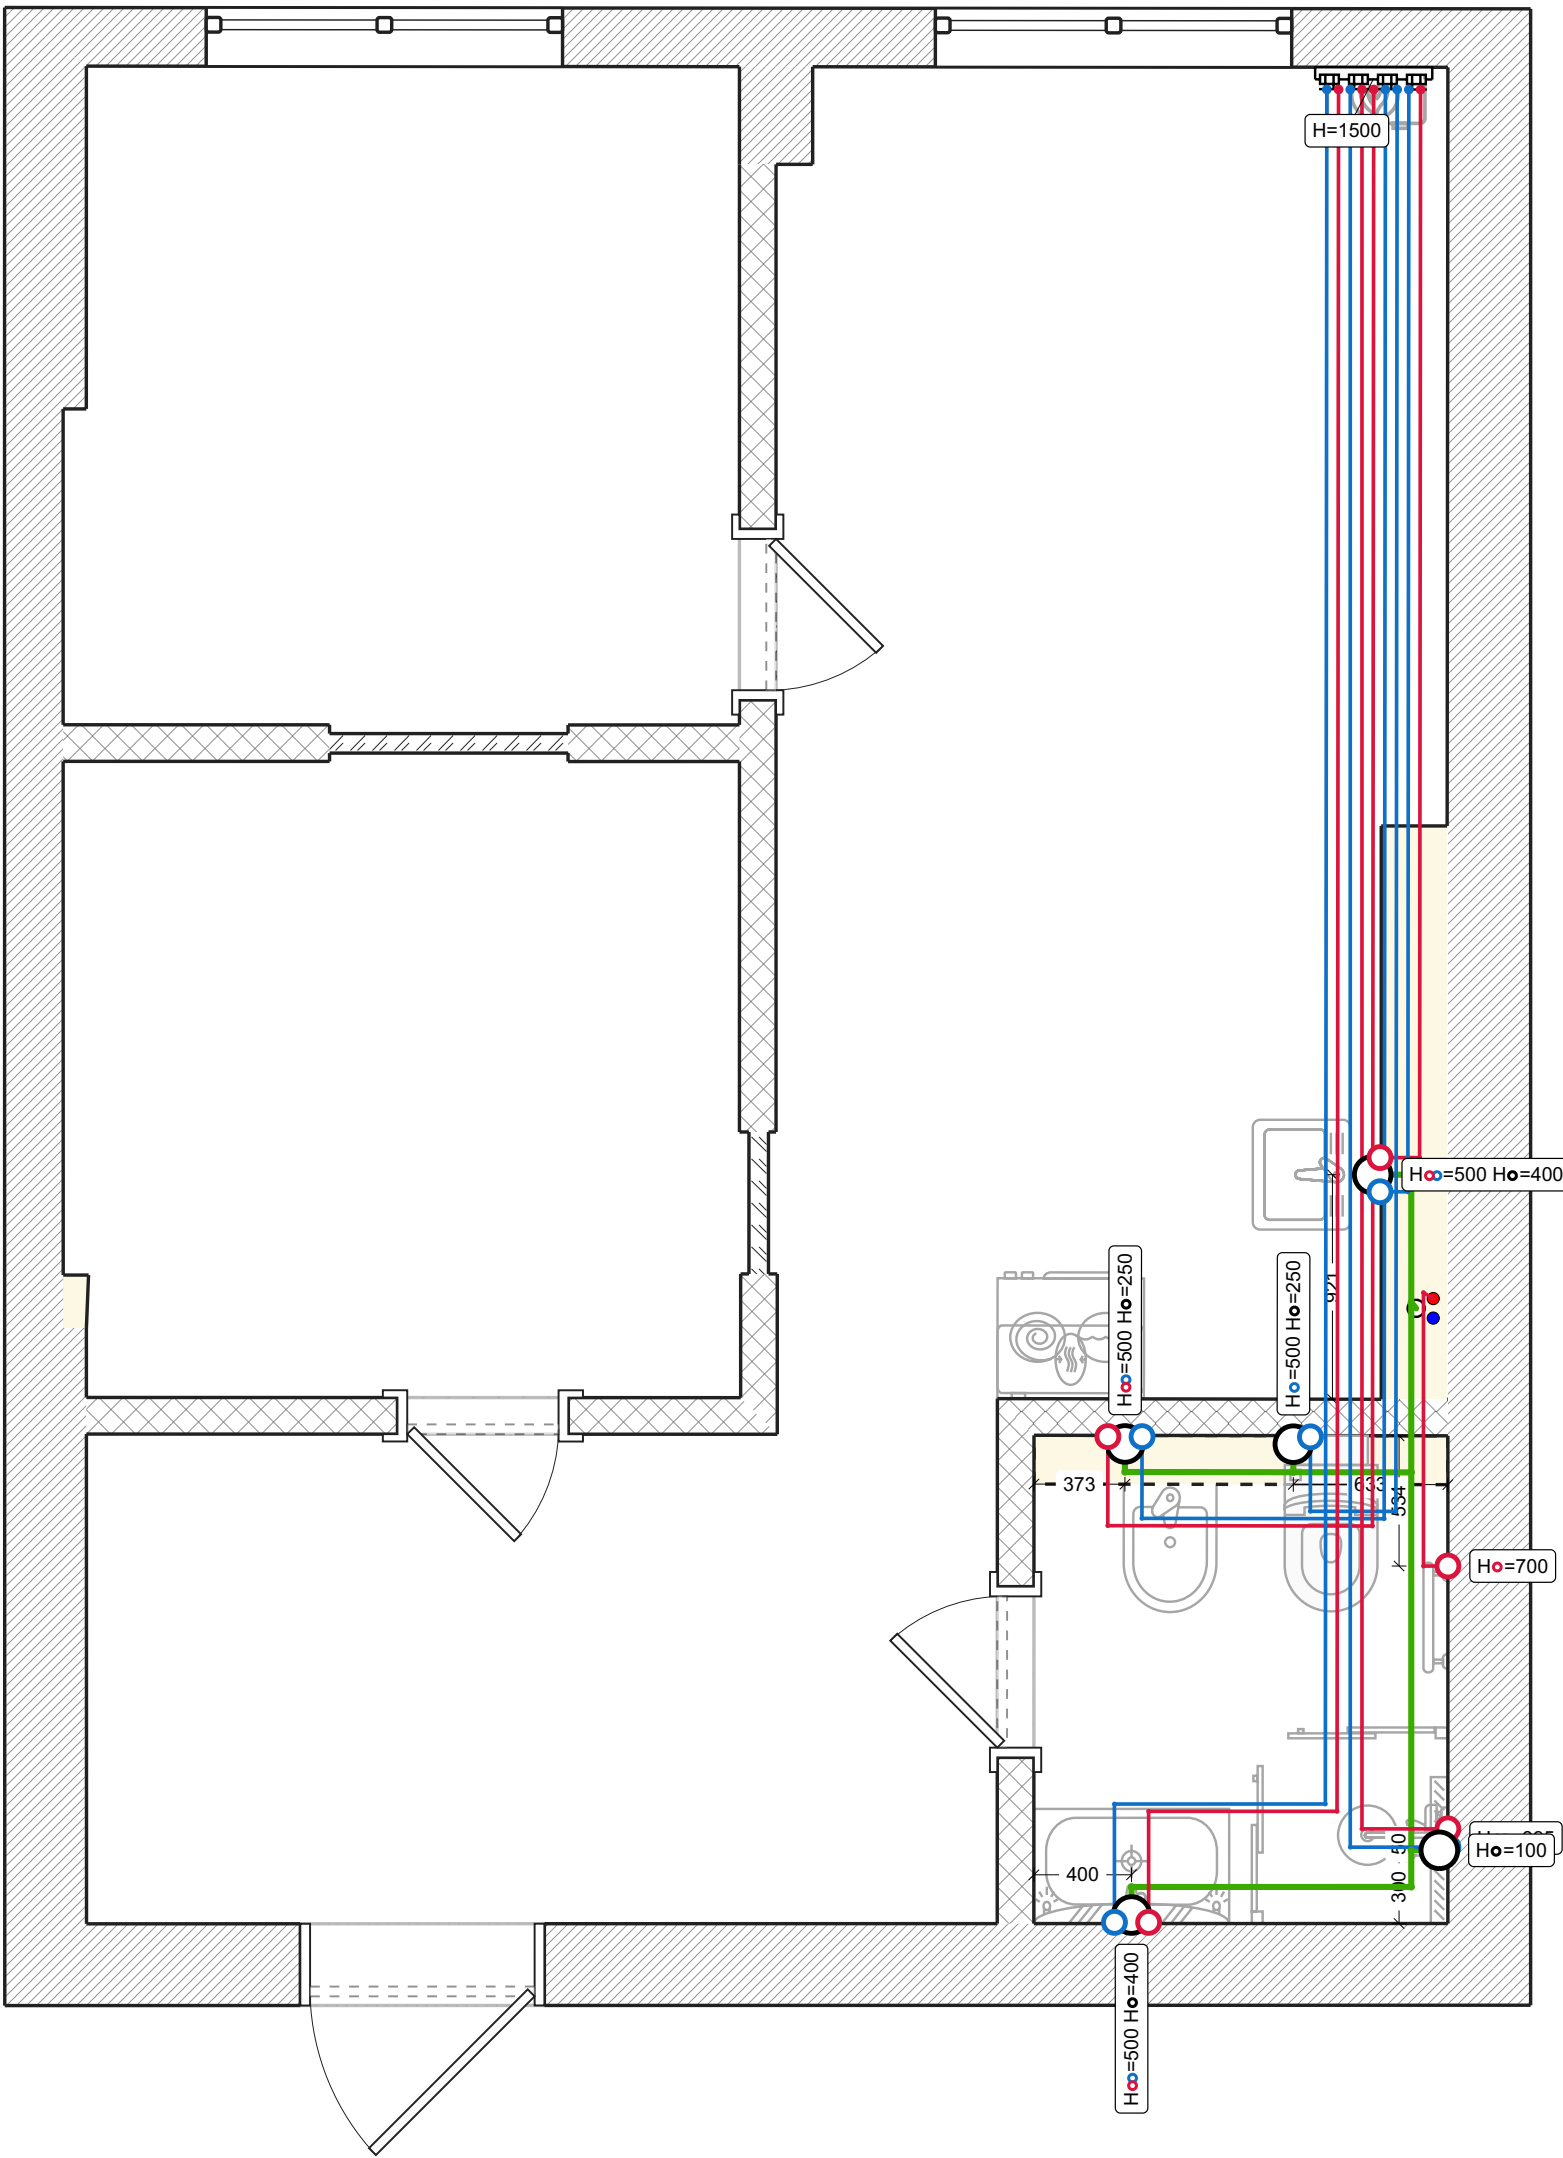



Розетки

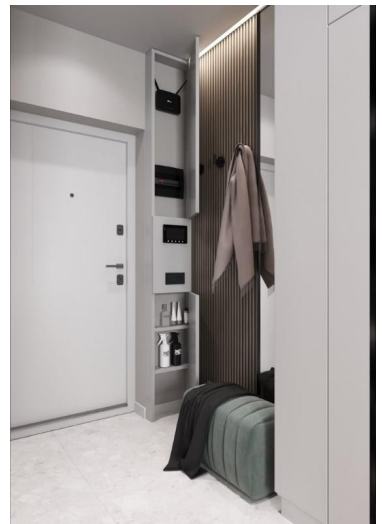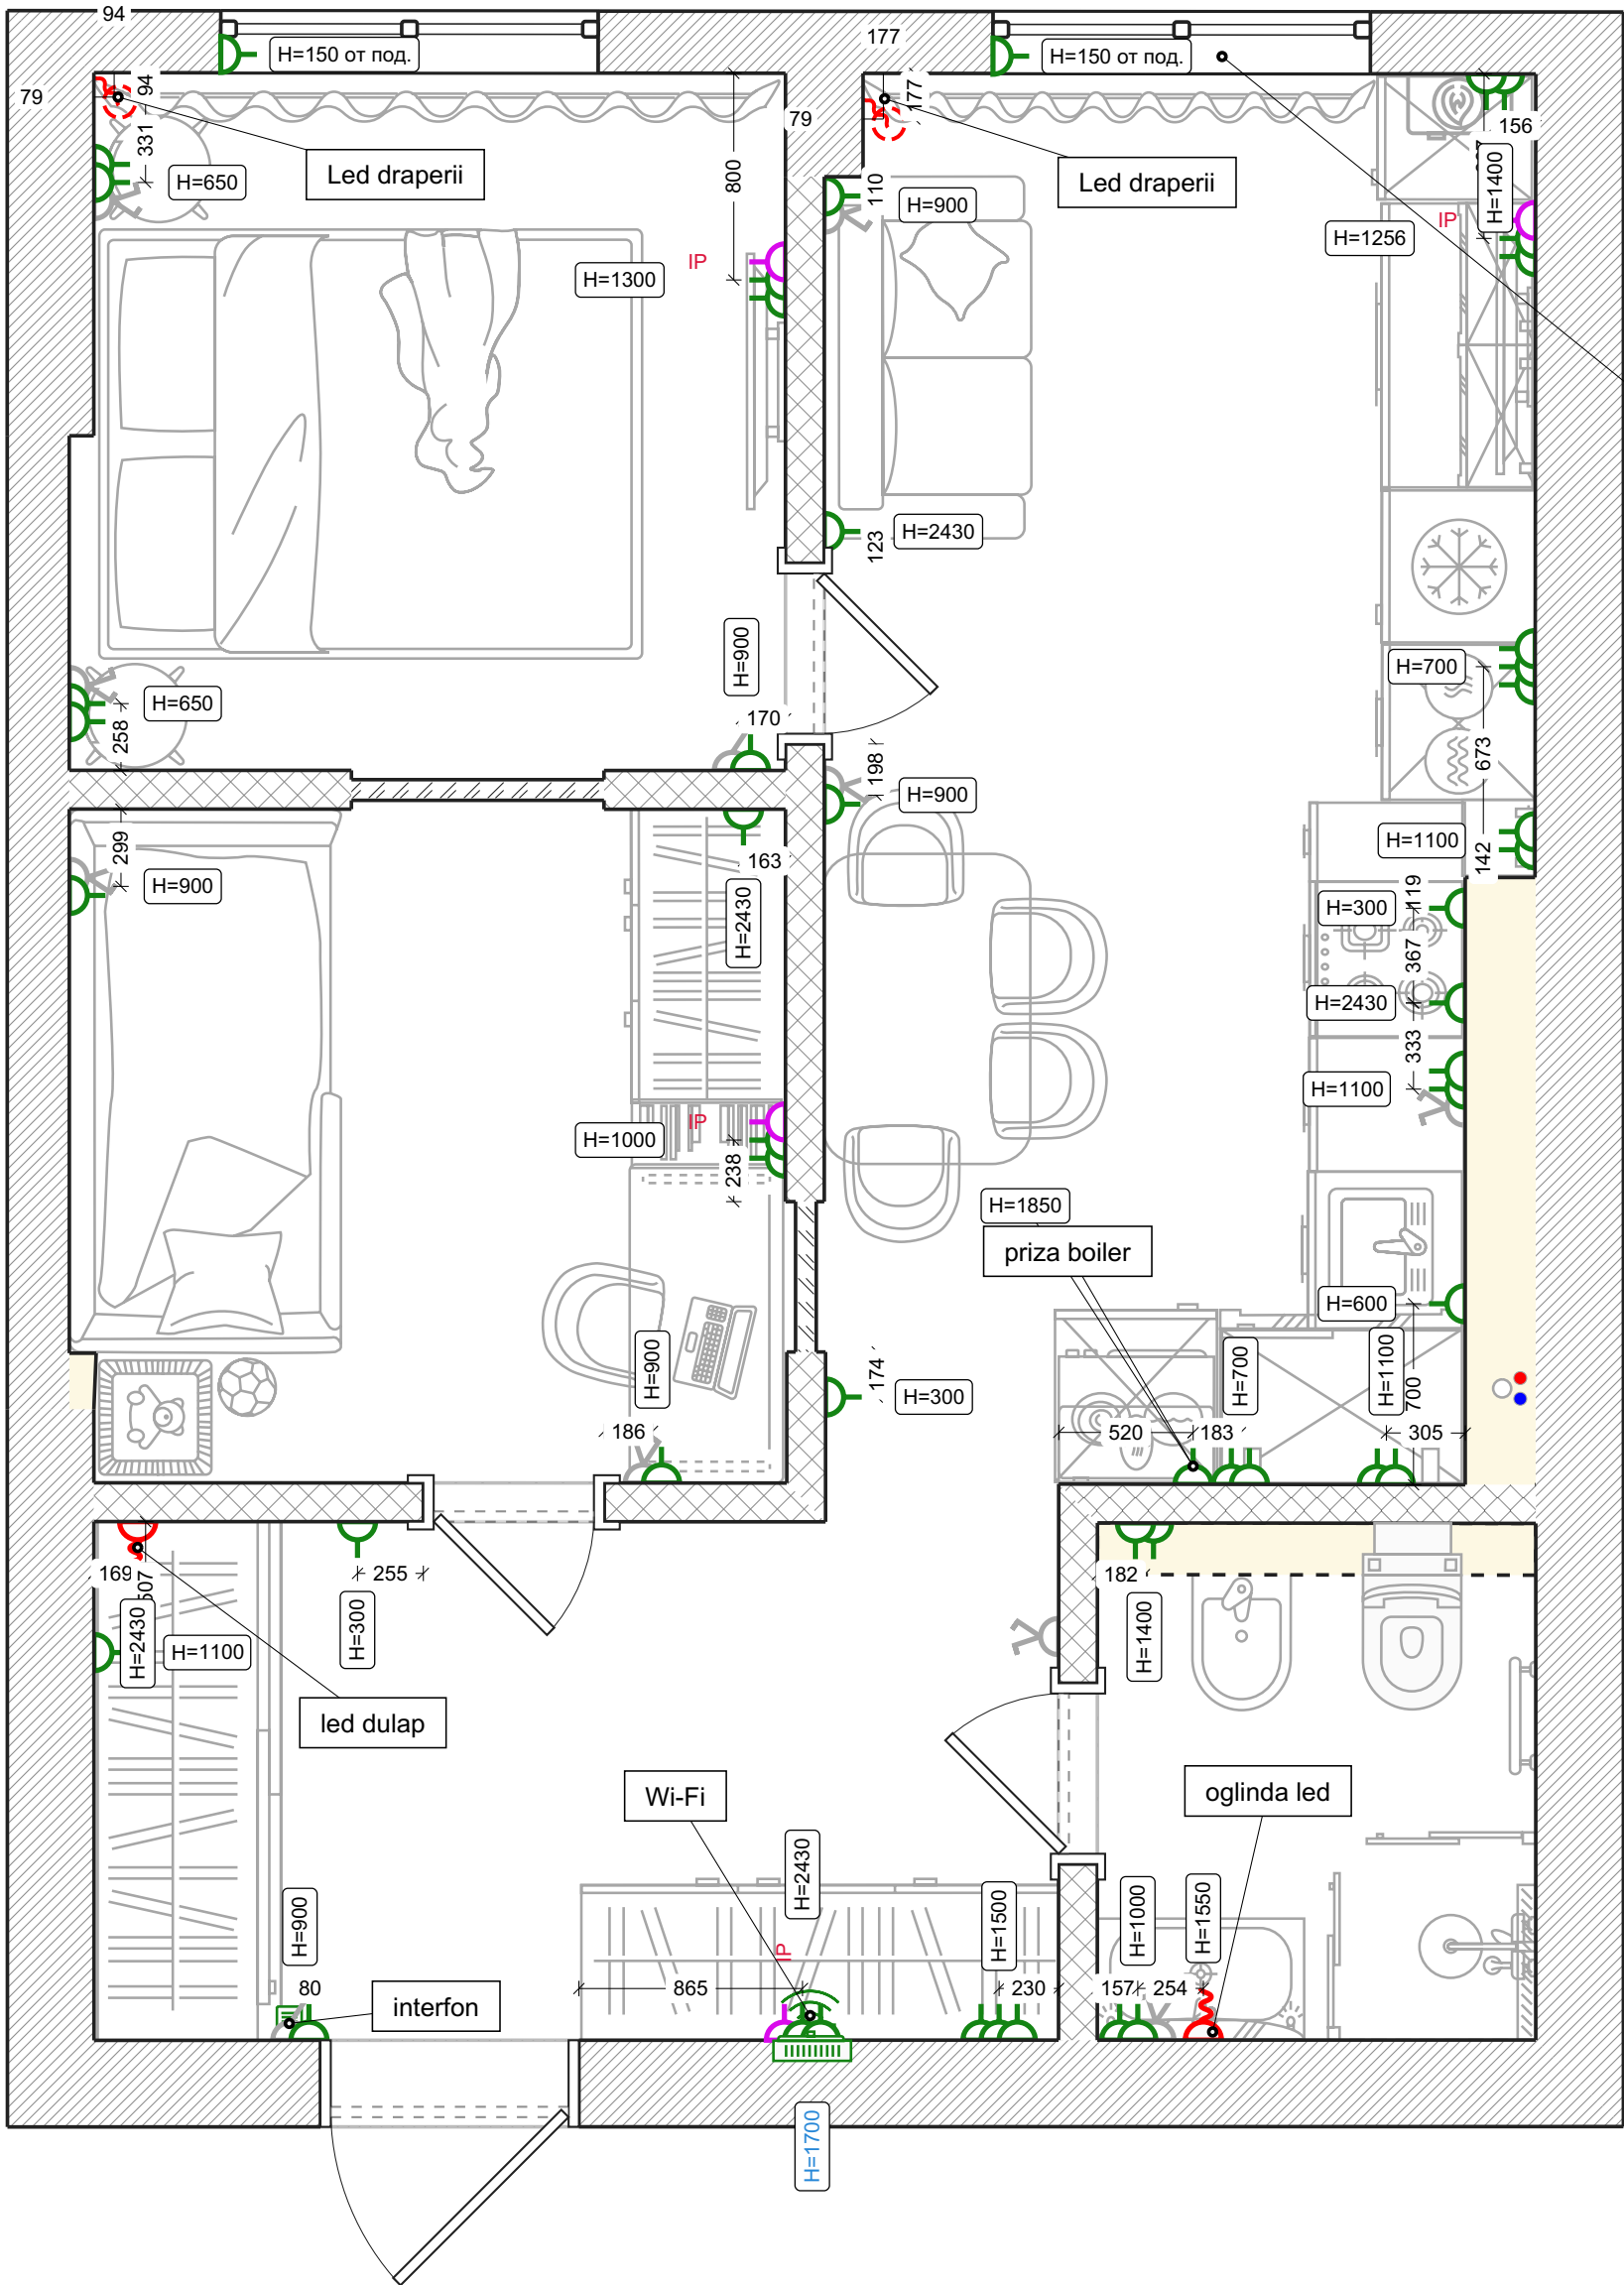

Условные обозначения:

- | | | | | | |
|--|---------------------|--|--------------------|--|------------------|
| | Стандартная розетка | | Домофон | | Потолочный вывод |
| | Слаботочная розетка | | Wi-fi роутер | | |
| | Вывод провода 220В | | Встр. электрощиток | | |

Освещение

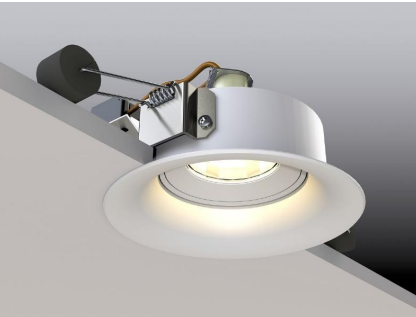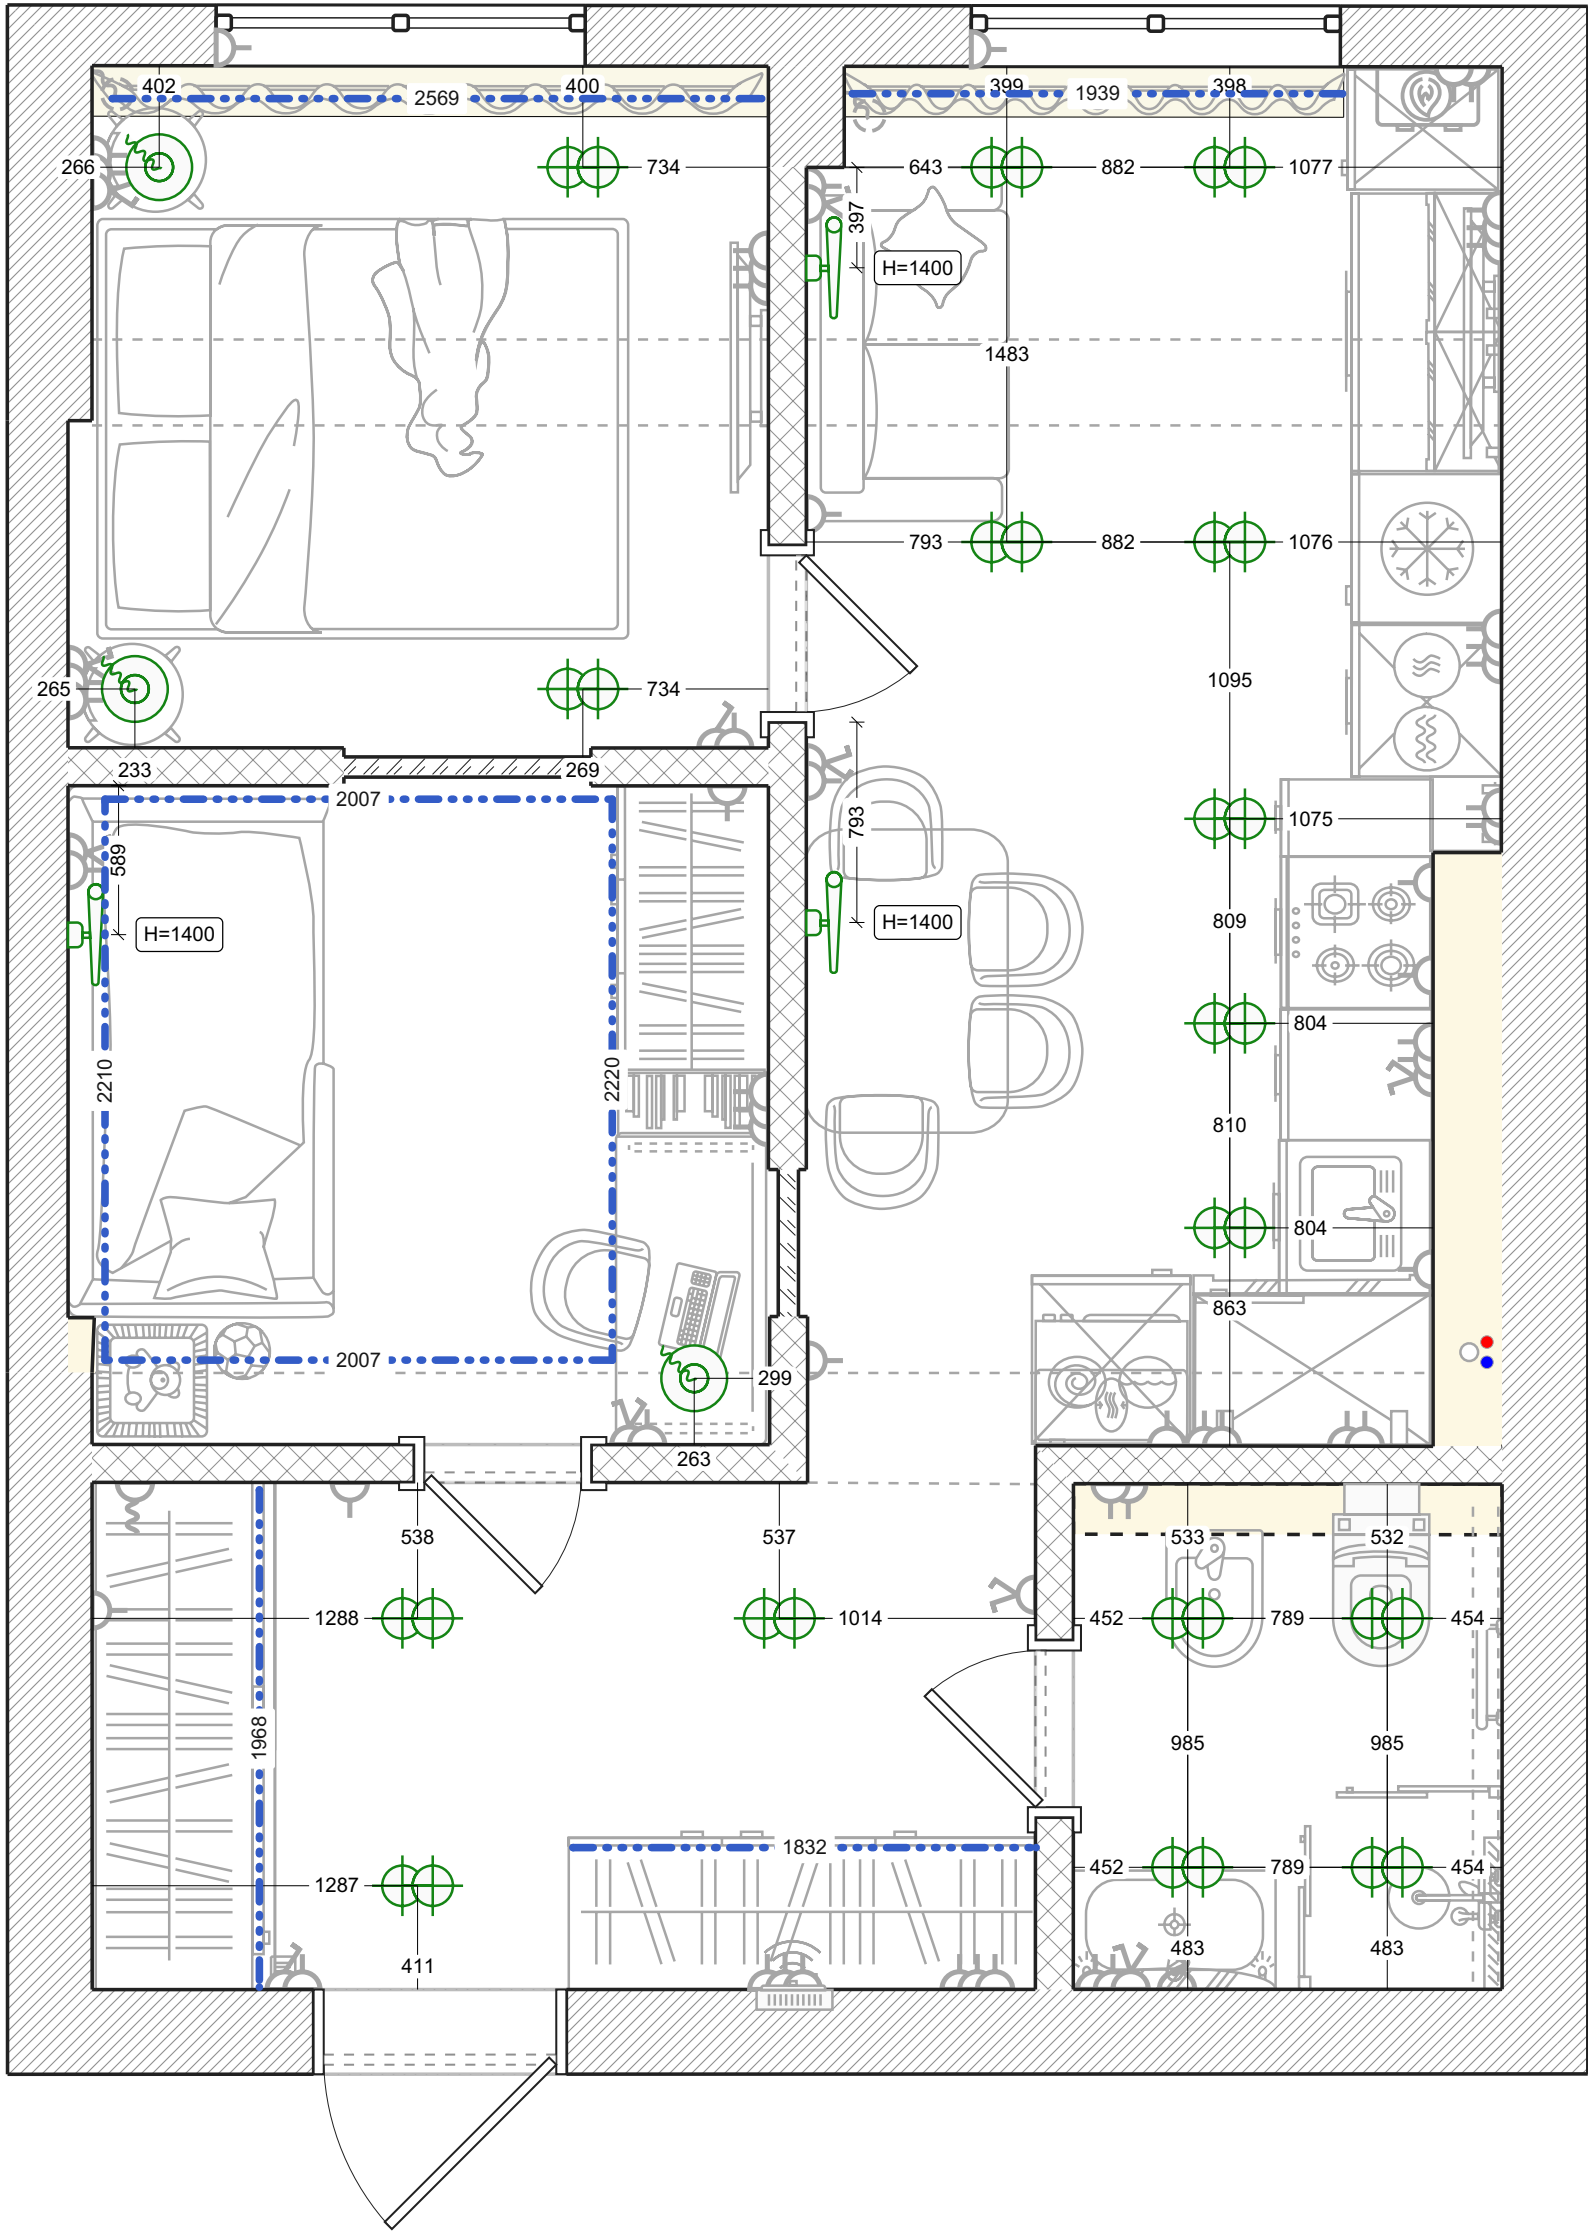


Условные обозначения:

- Подвесной светильник
- Светильник встра. двойной
- Светодиодная подсветка
- Светильник-палка

Выключатели

Условные обозначения:


- 1-клавишный выключатель
- 2-клавишный выключатель

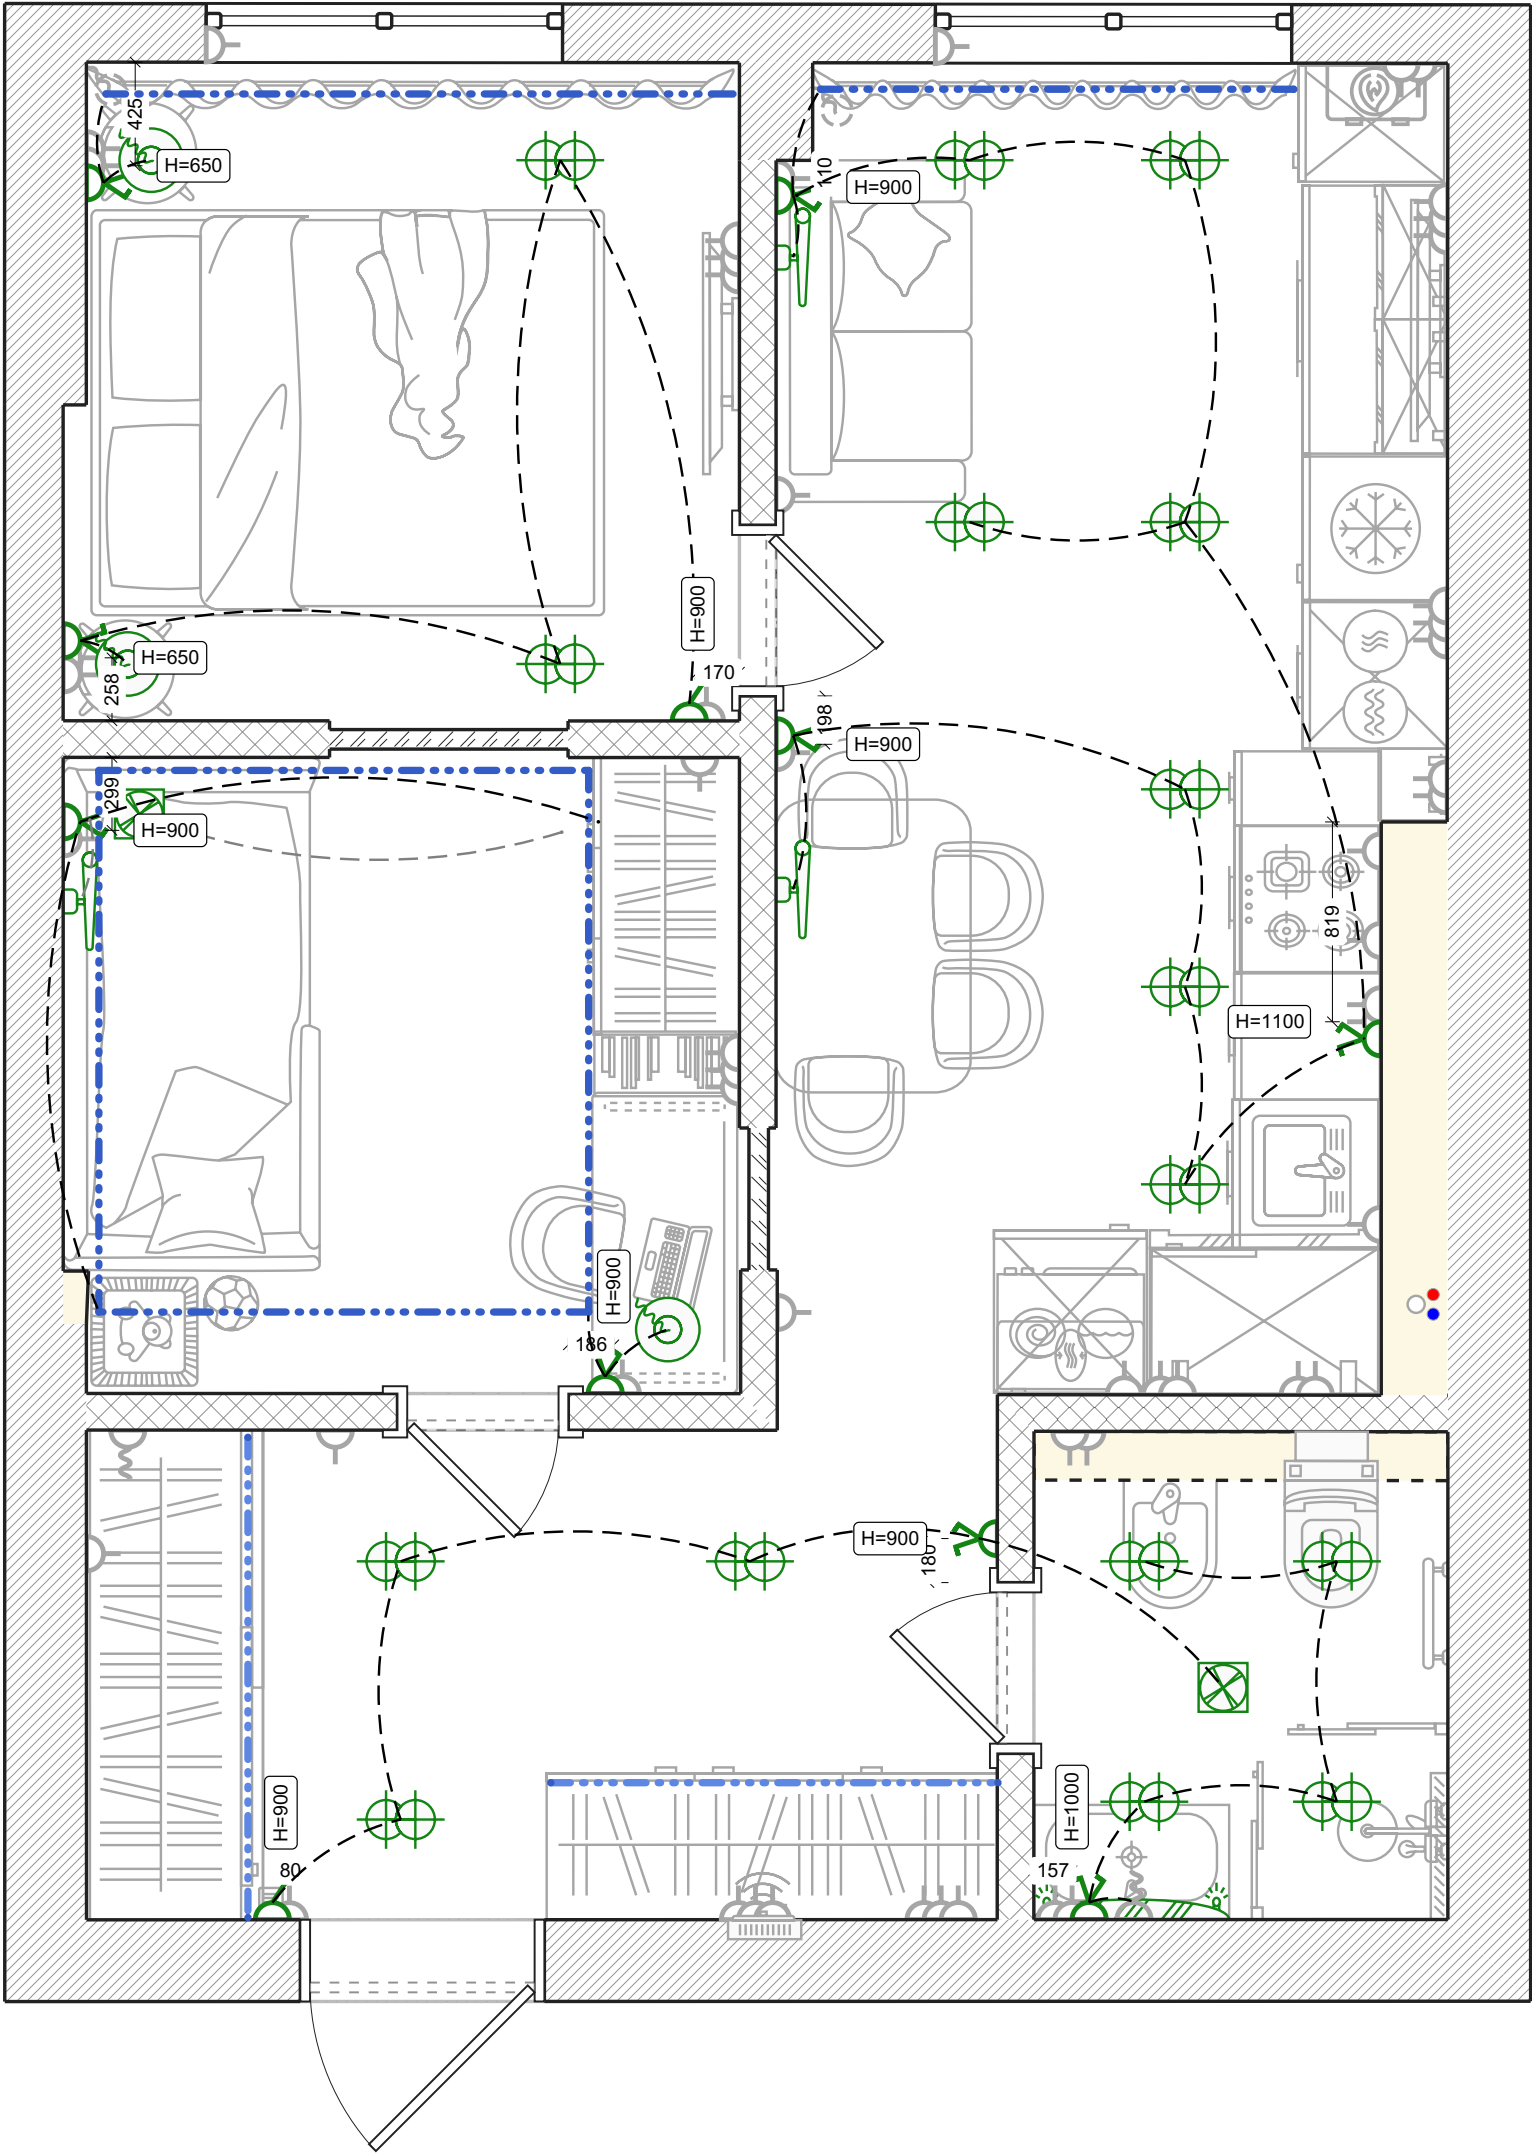

Теплые полы

Условные обозначения:


-  Водяной теплый пол
-  Соединительные магистрали

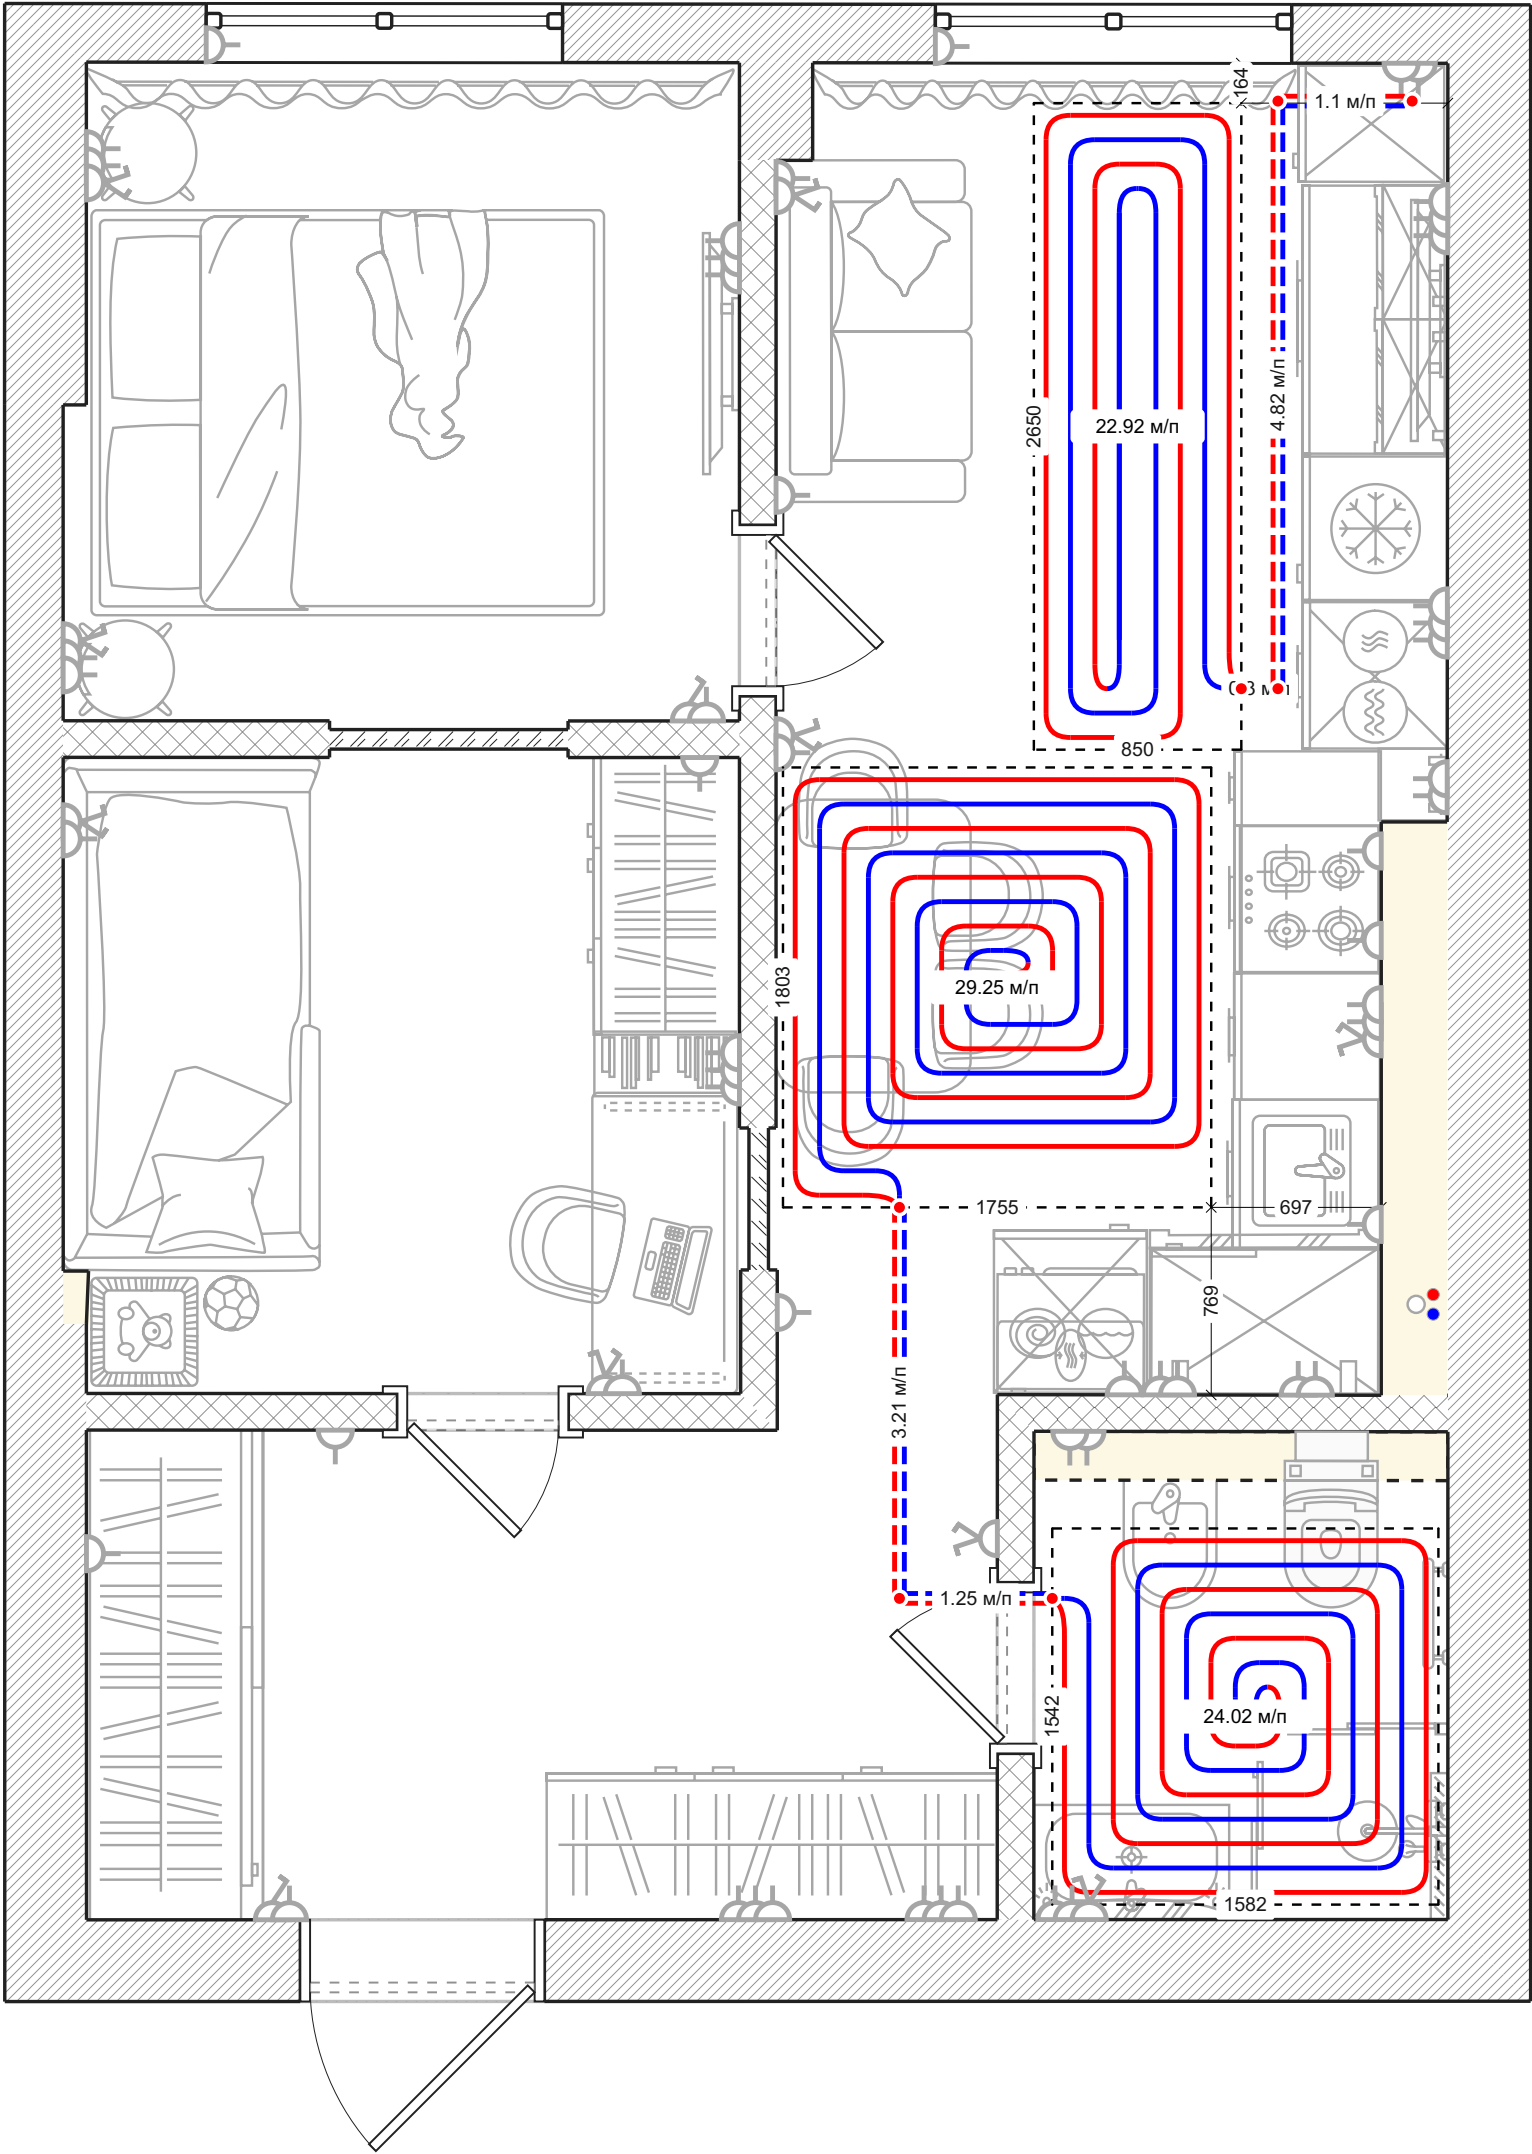

Кондиционеры

Условные обозначения:

-  Внешн. блок сплит-системы
-  Внутр. блок сплит-системы
-  Трубопровод для дренажа
-  Трасса кондиционера

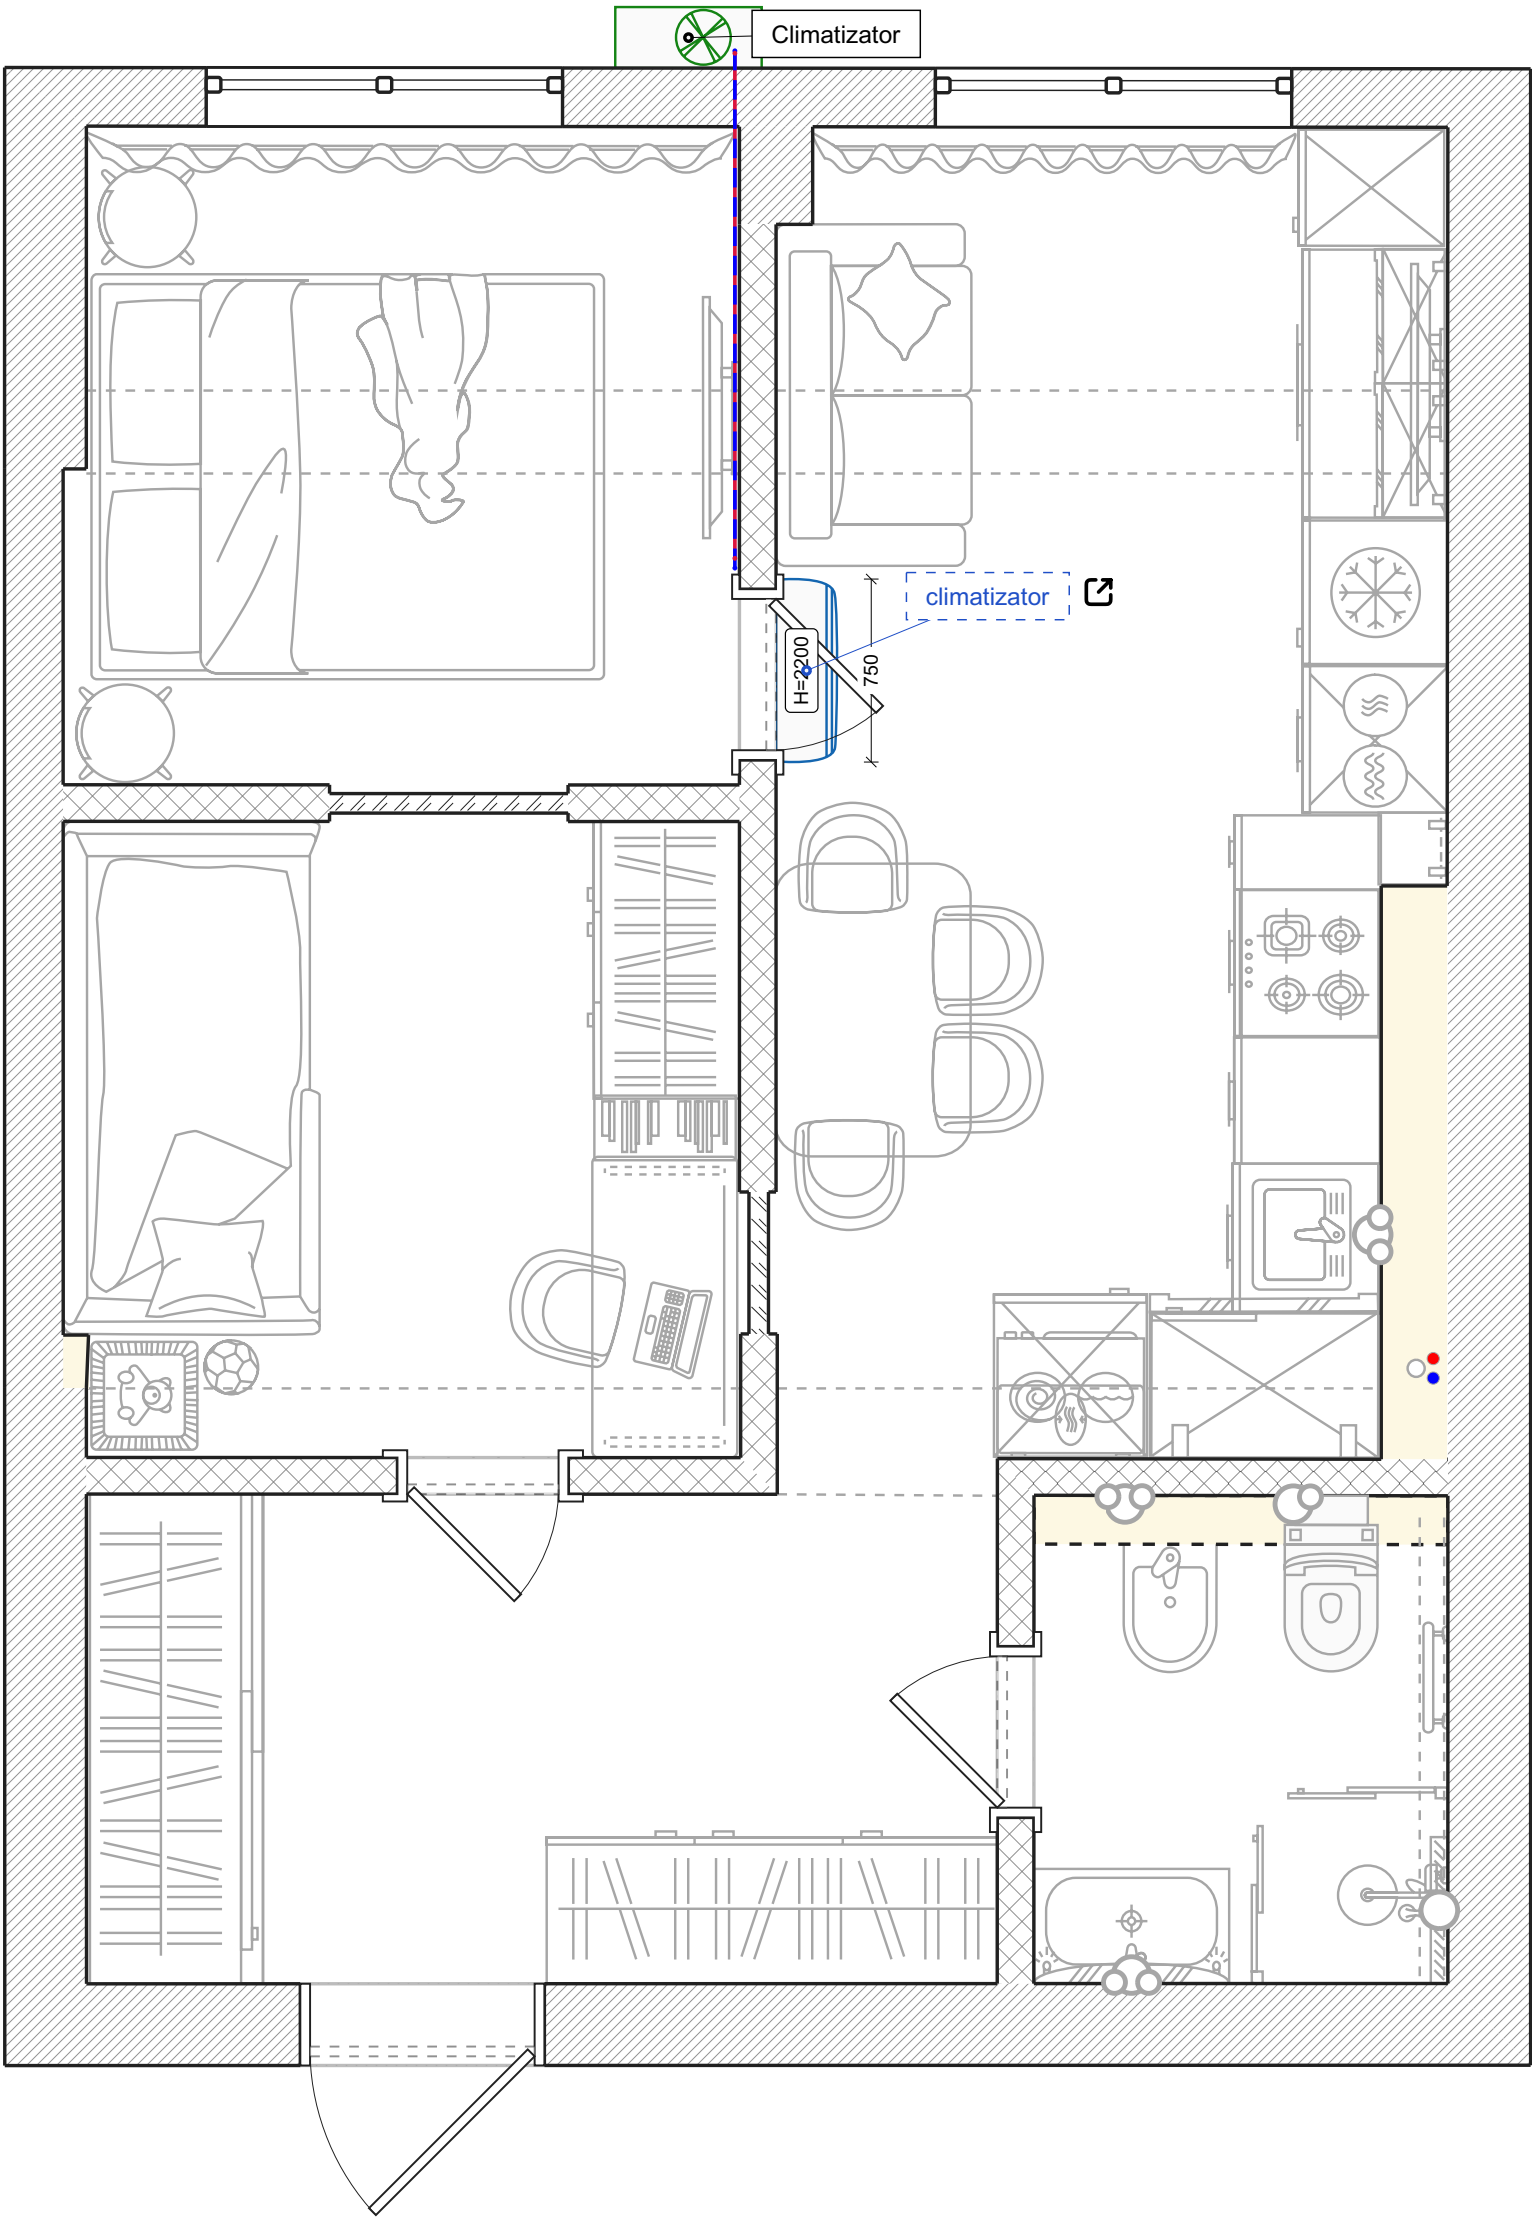


Электрощиток

Условные обозначения:

- Автомат. выключатель
- Электросчетчик
- Автомат вводной
- Выключатель нагрузки
- Щитовая розетка
- УЗО
- Реле напряжения

PE
N
L

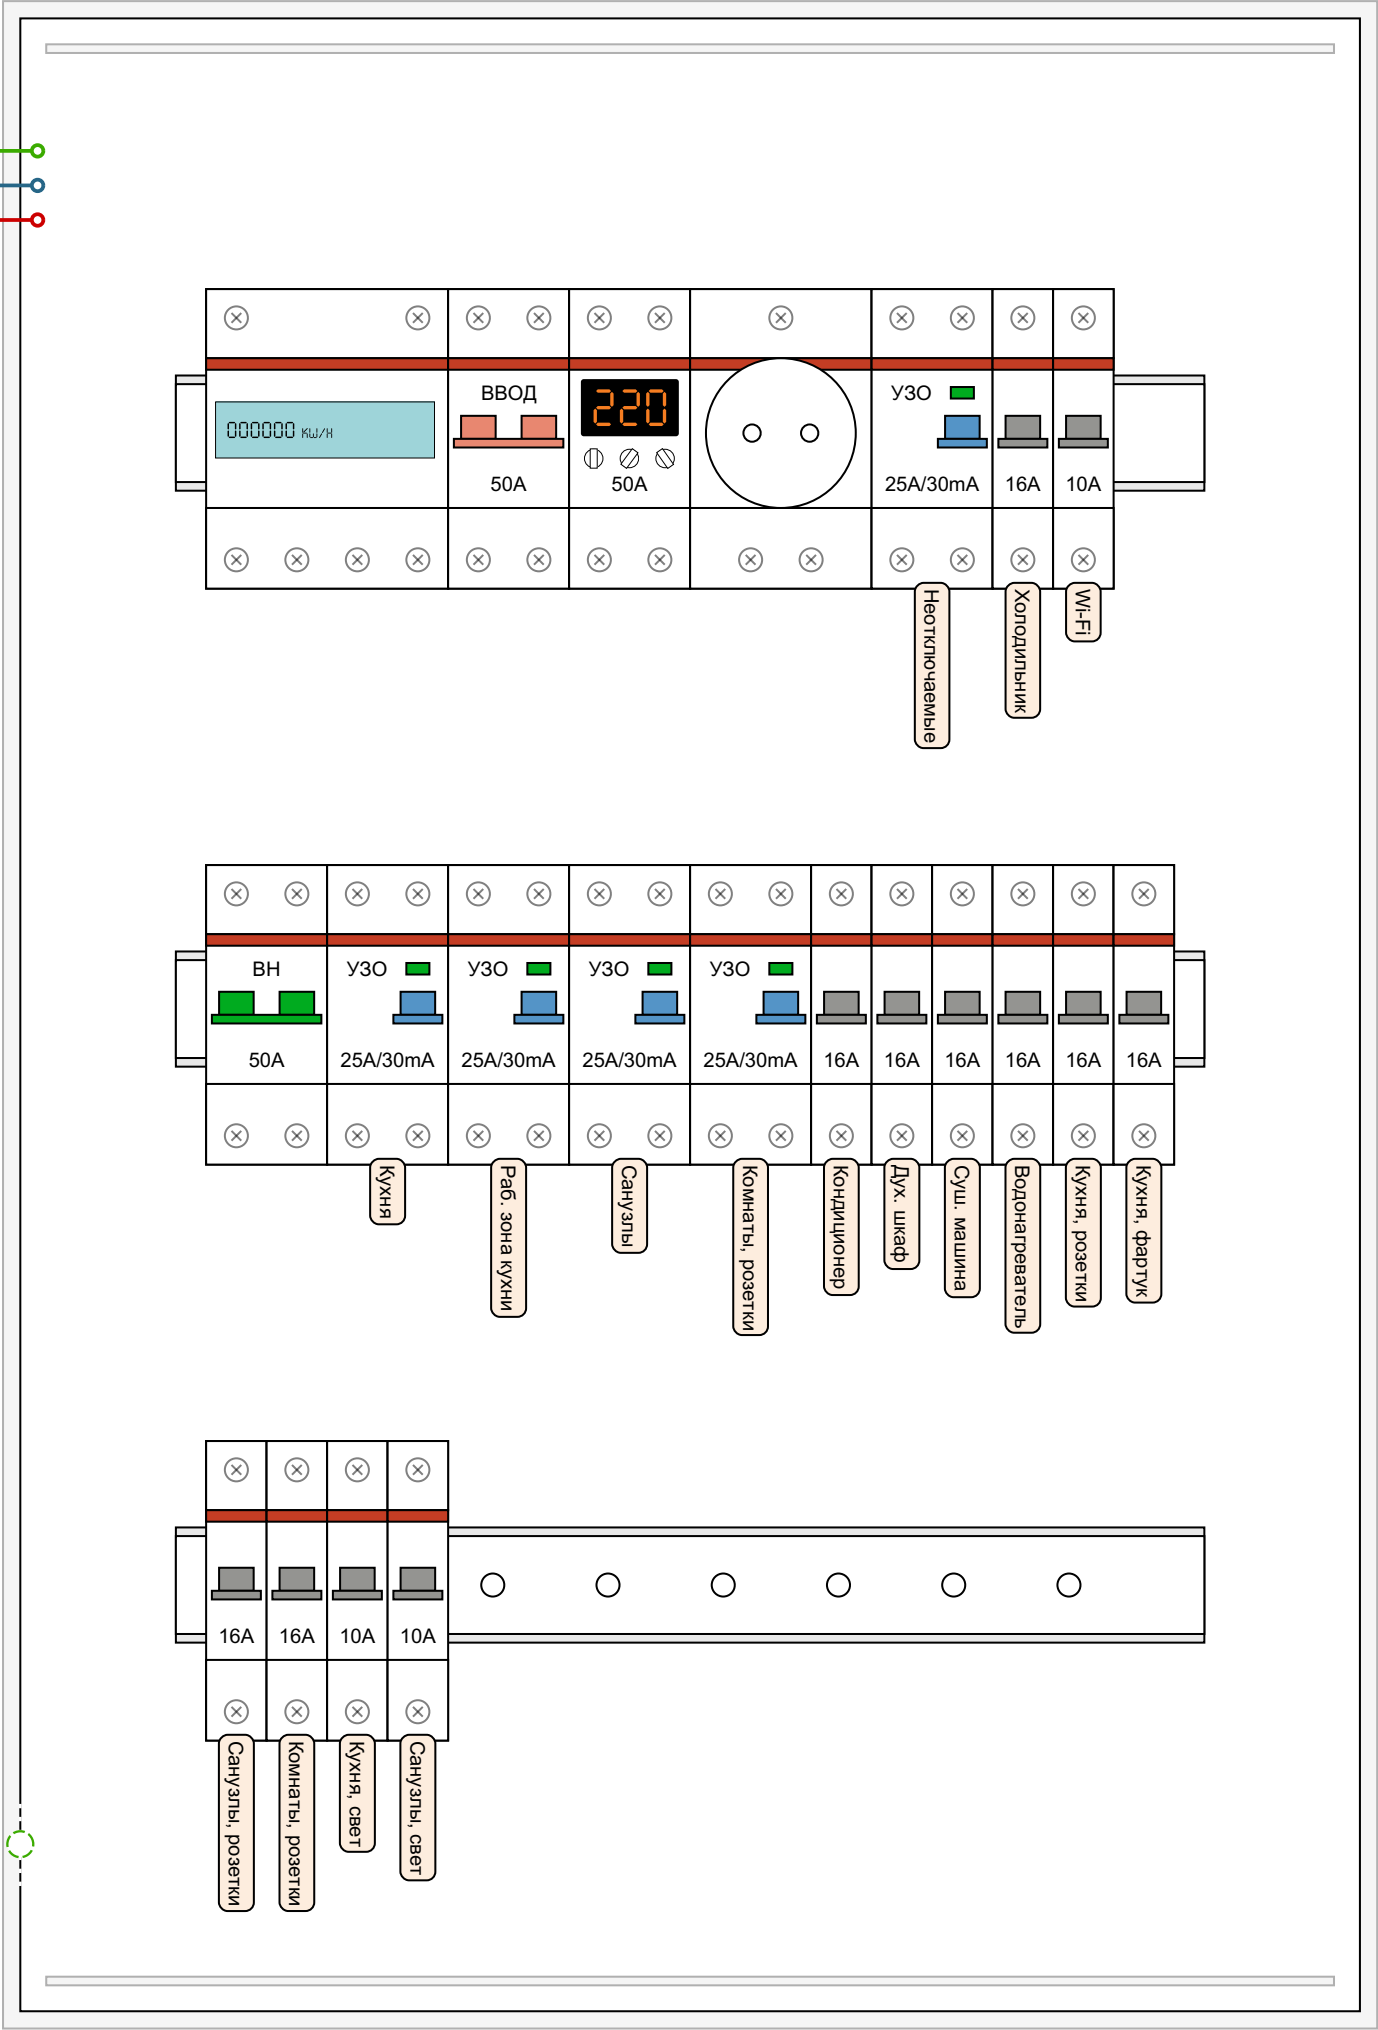


Вентиляция

Условные обозначения:

 Вентилятор потолочный


 Воздуховод вытяжной

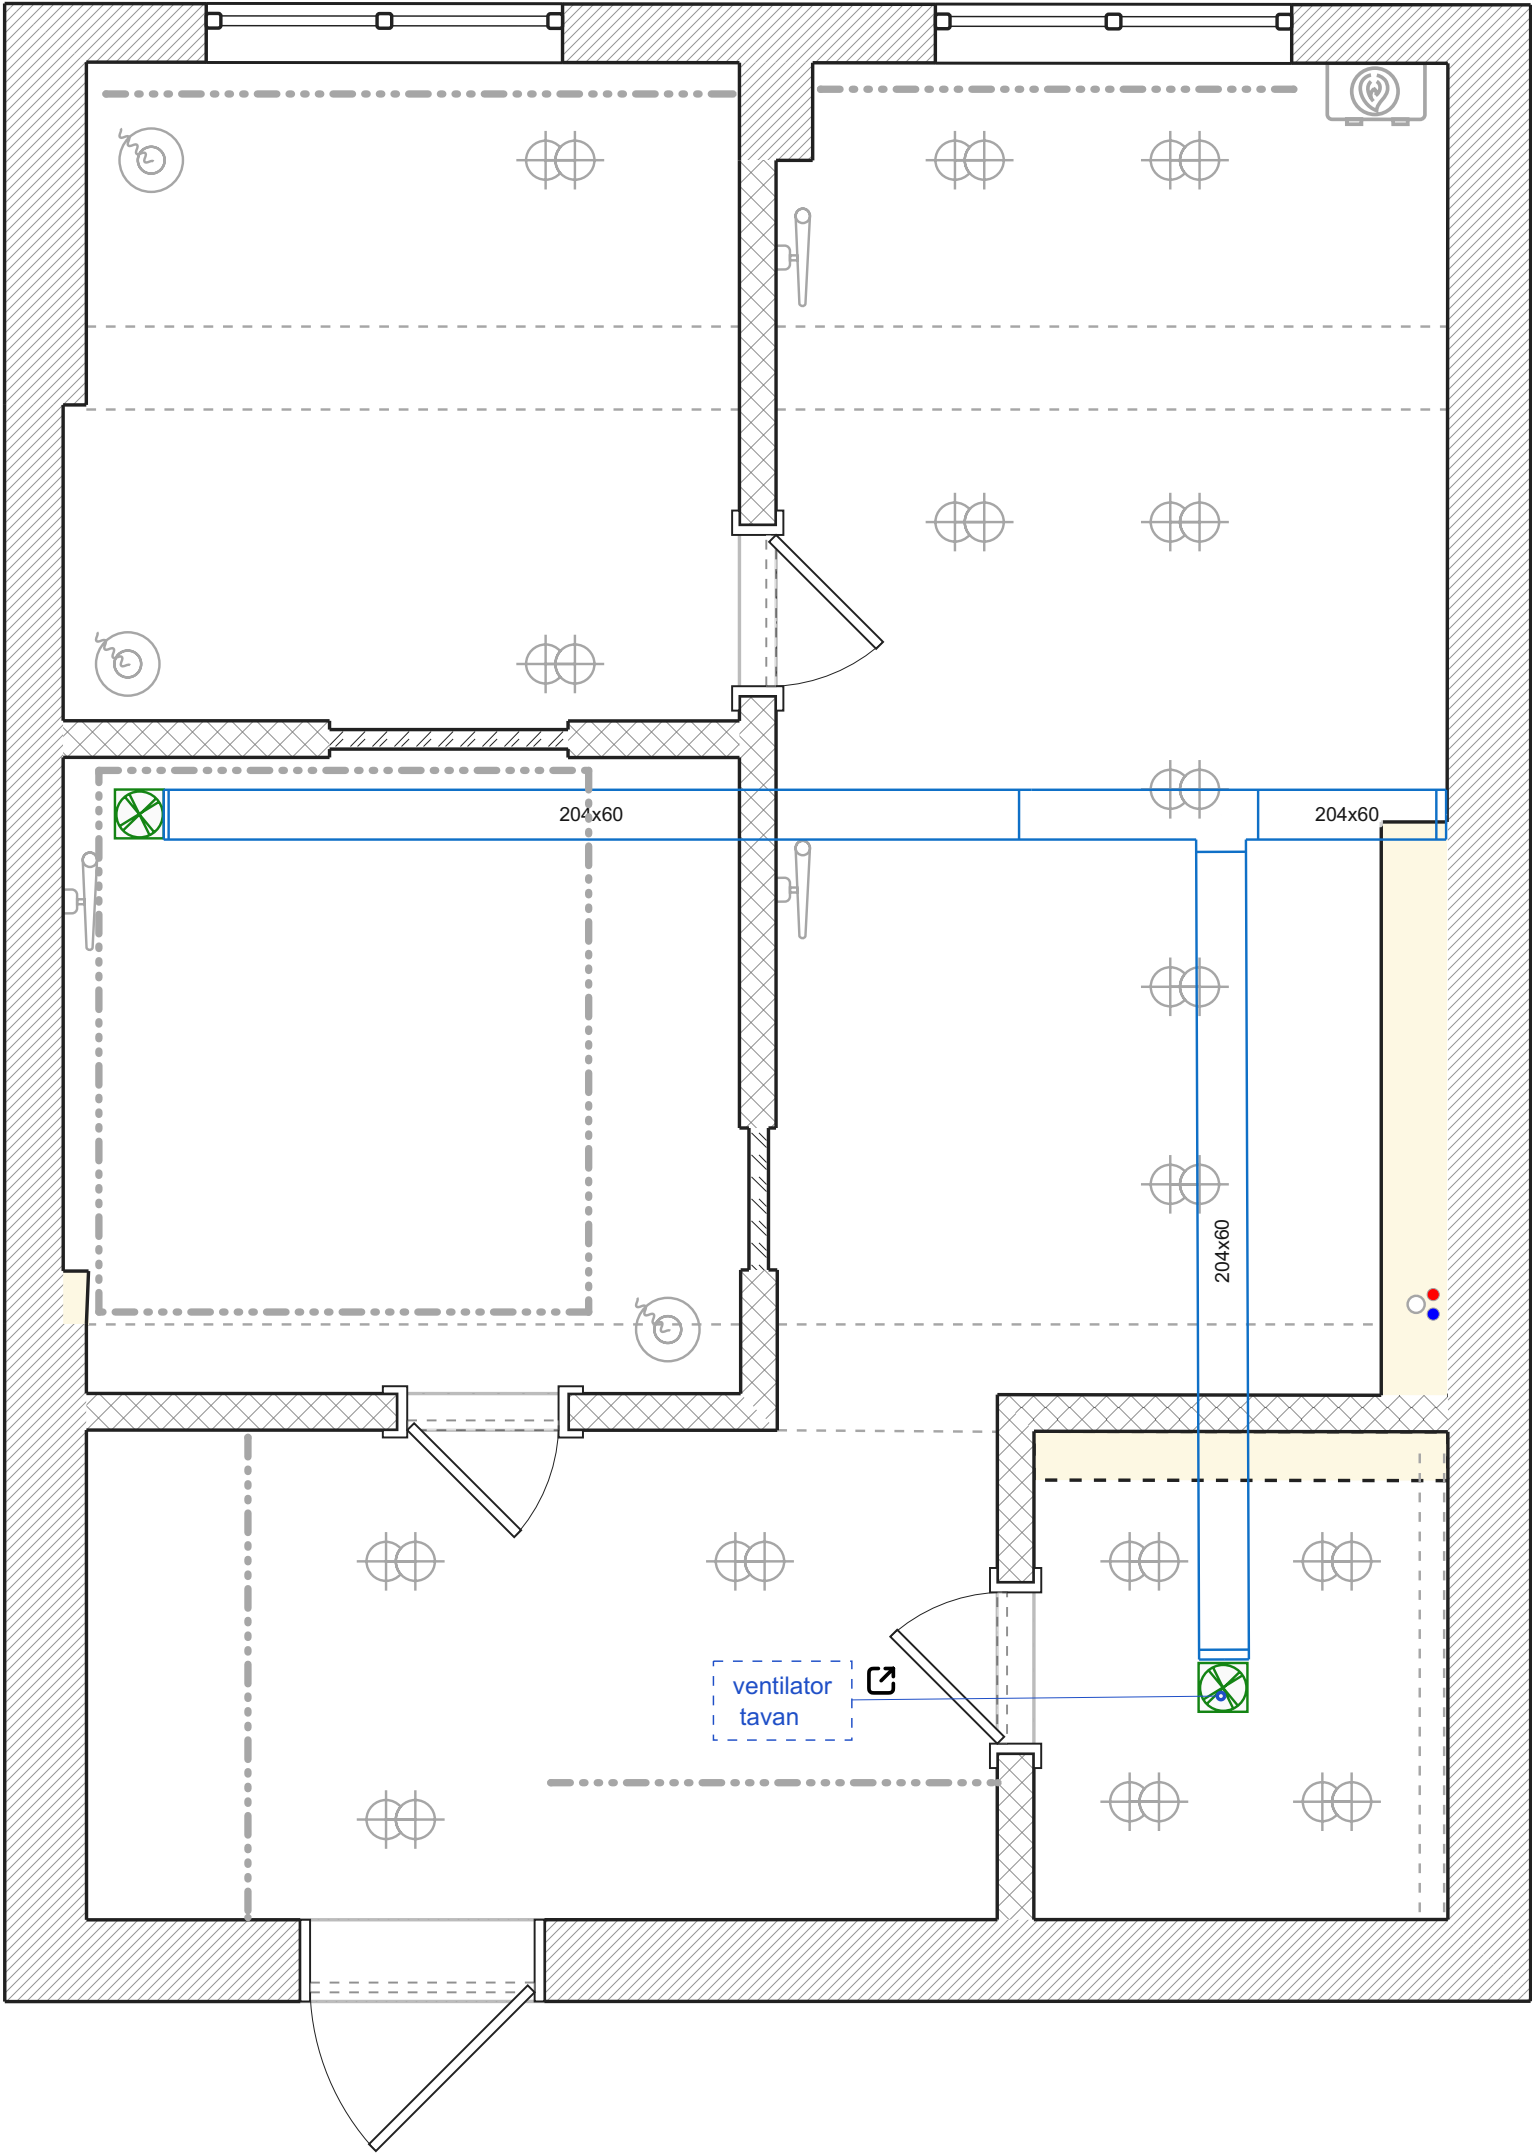

Электропроводка

Условные обозначения:


 Встр. электрощиток

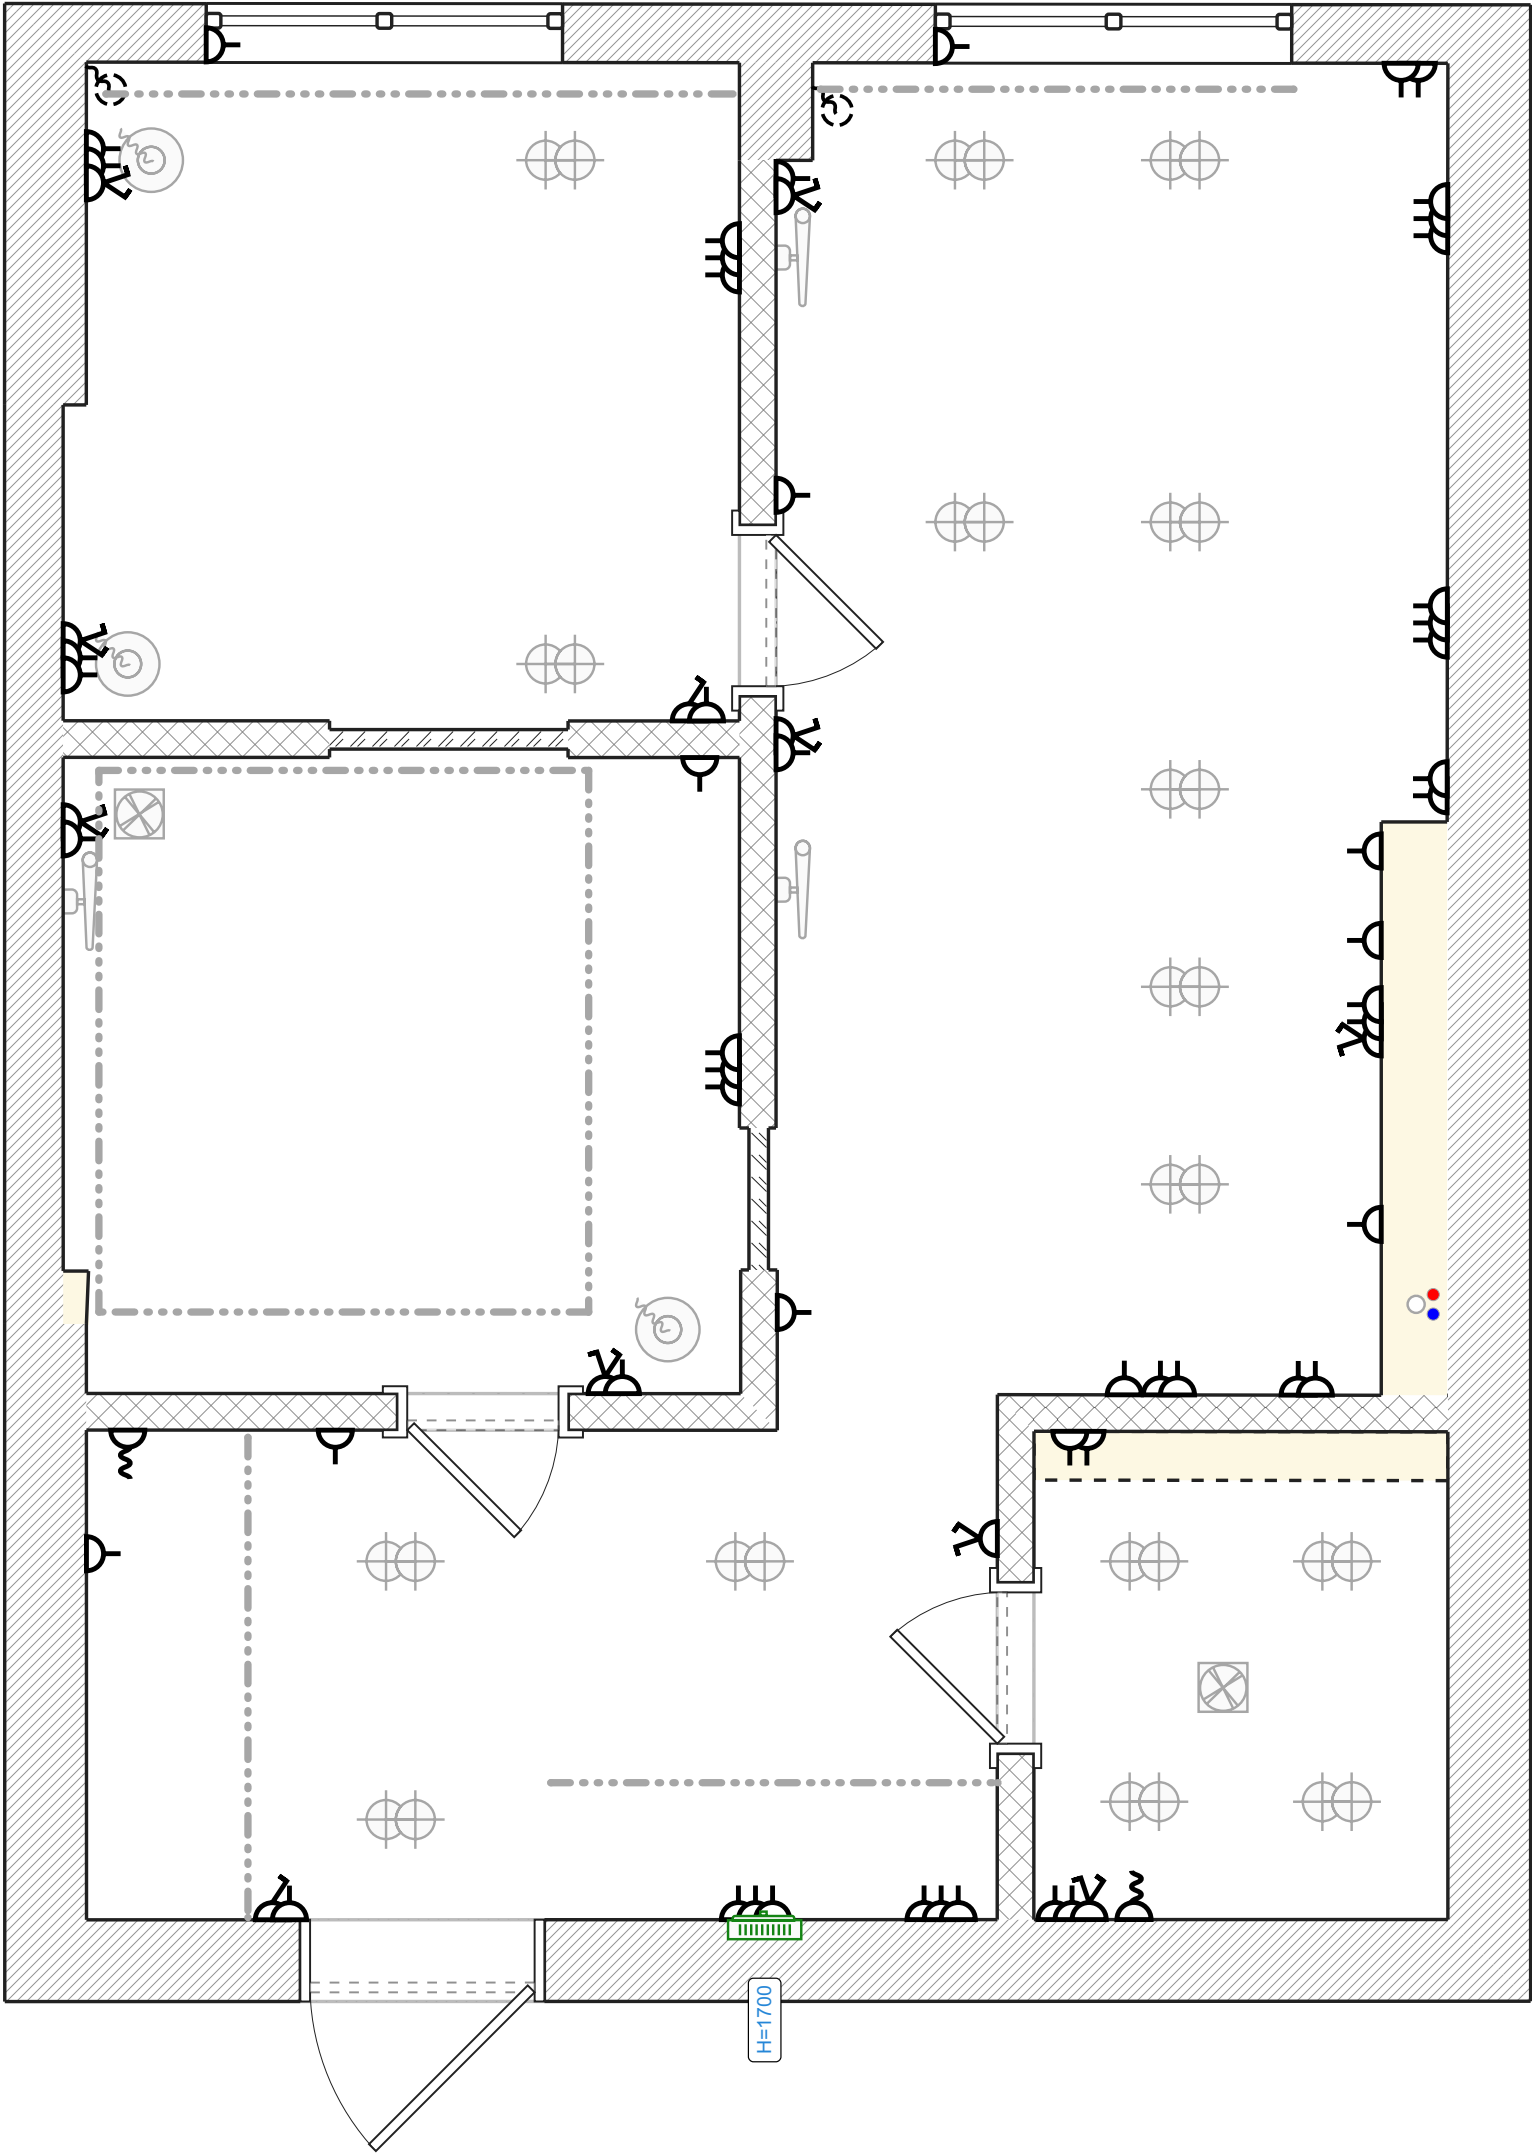

Напольные покрытия

Условные обозначения:


-  Паркетная доска
-  Керамогранит под мрамор

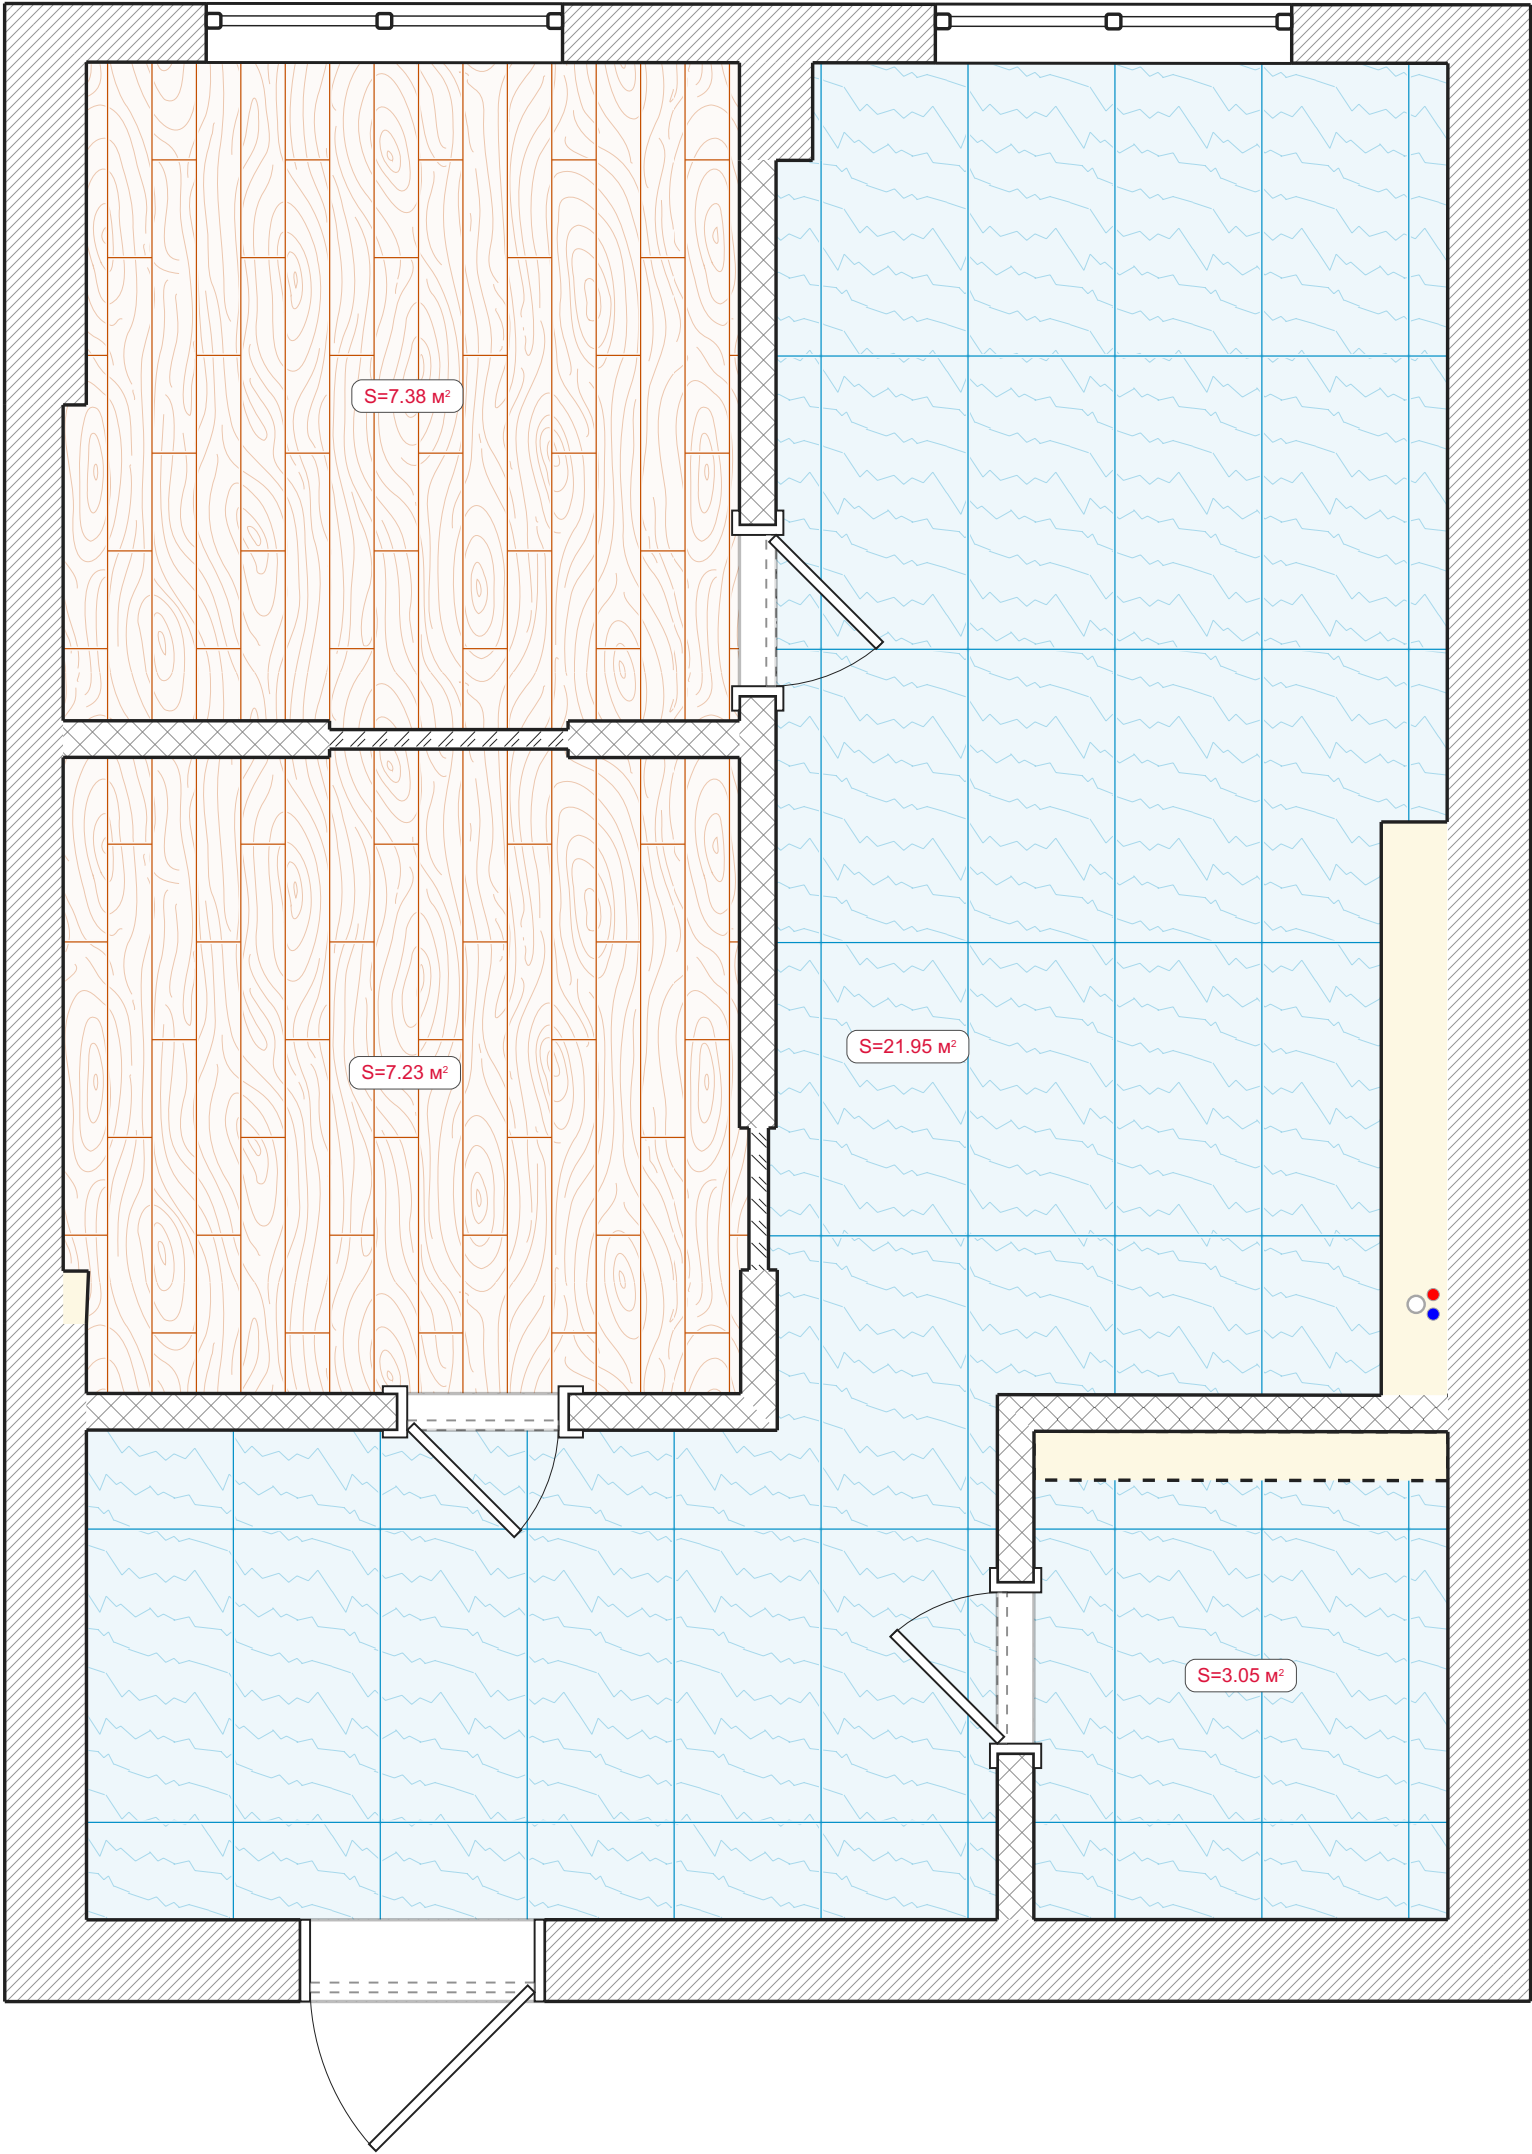

Отделка стен

Условные обозначения:


- Реечные панели
- Облицовка плиткой
- Обои под покраску

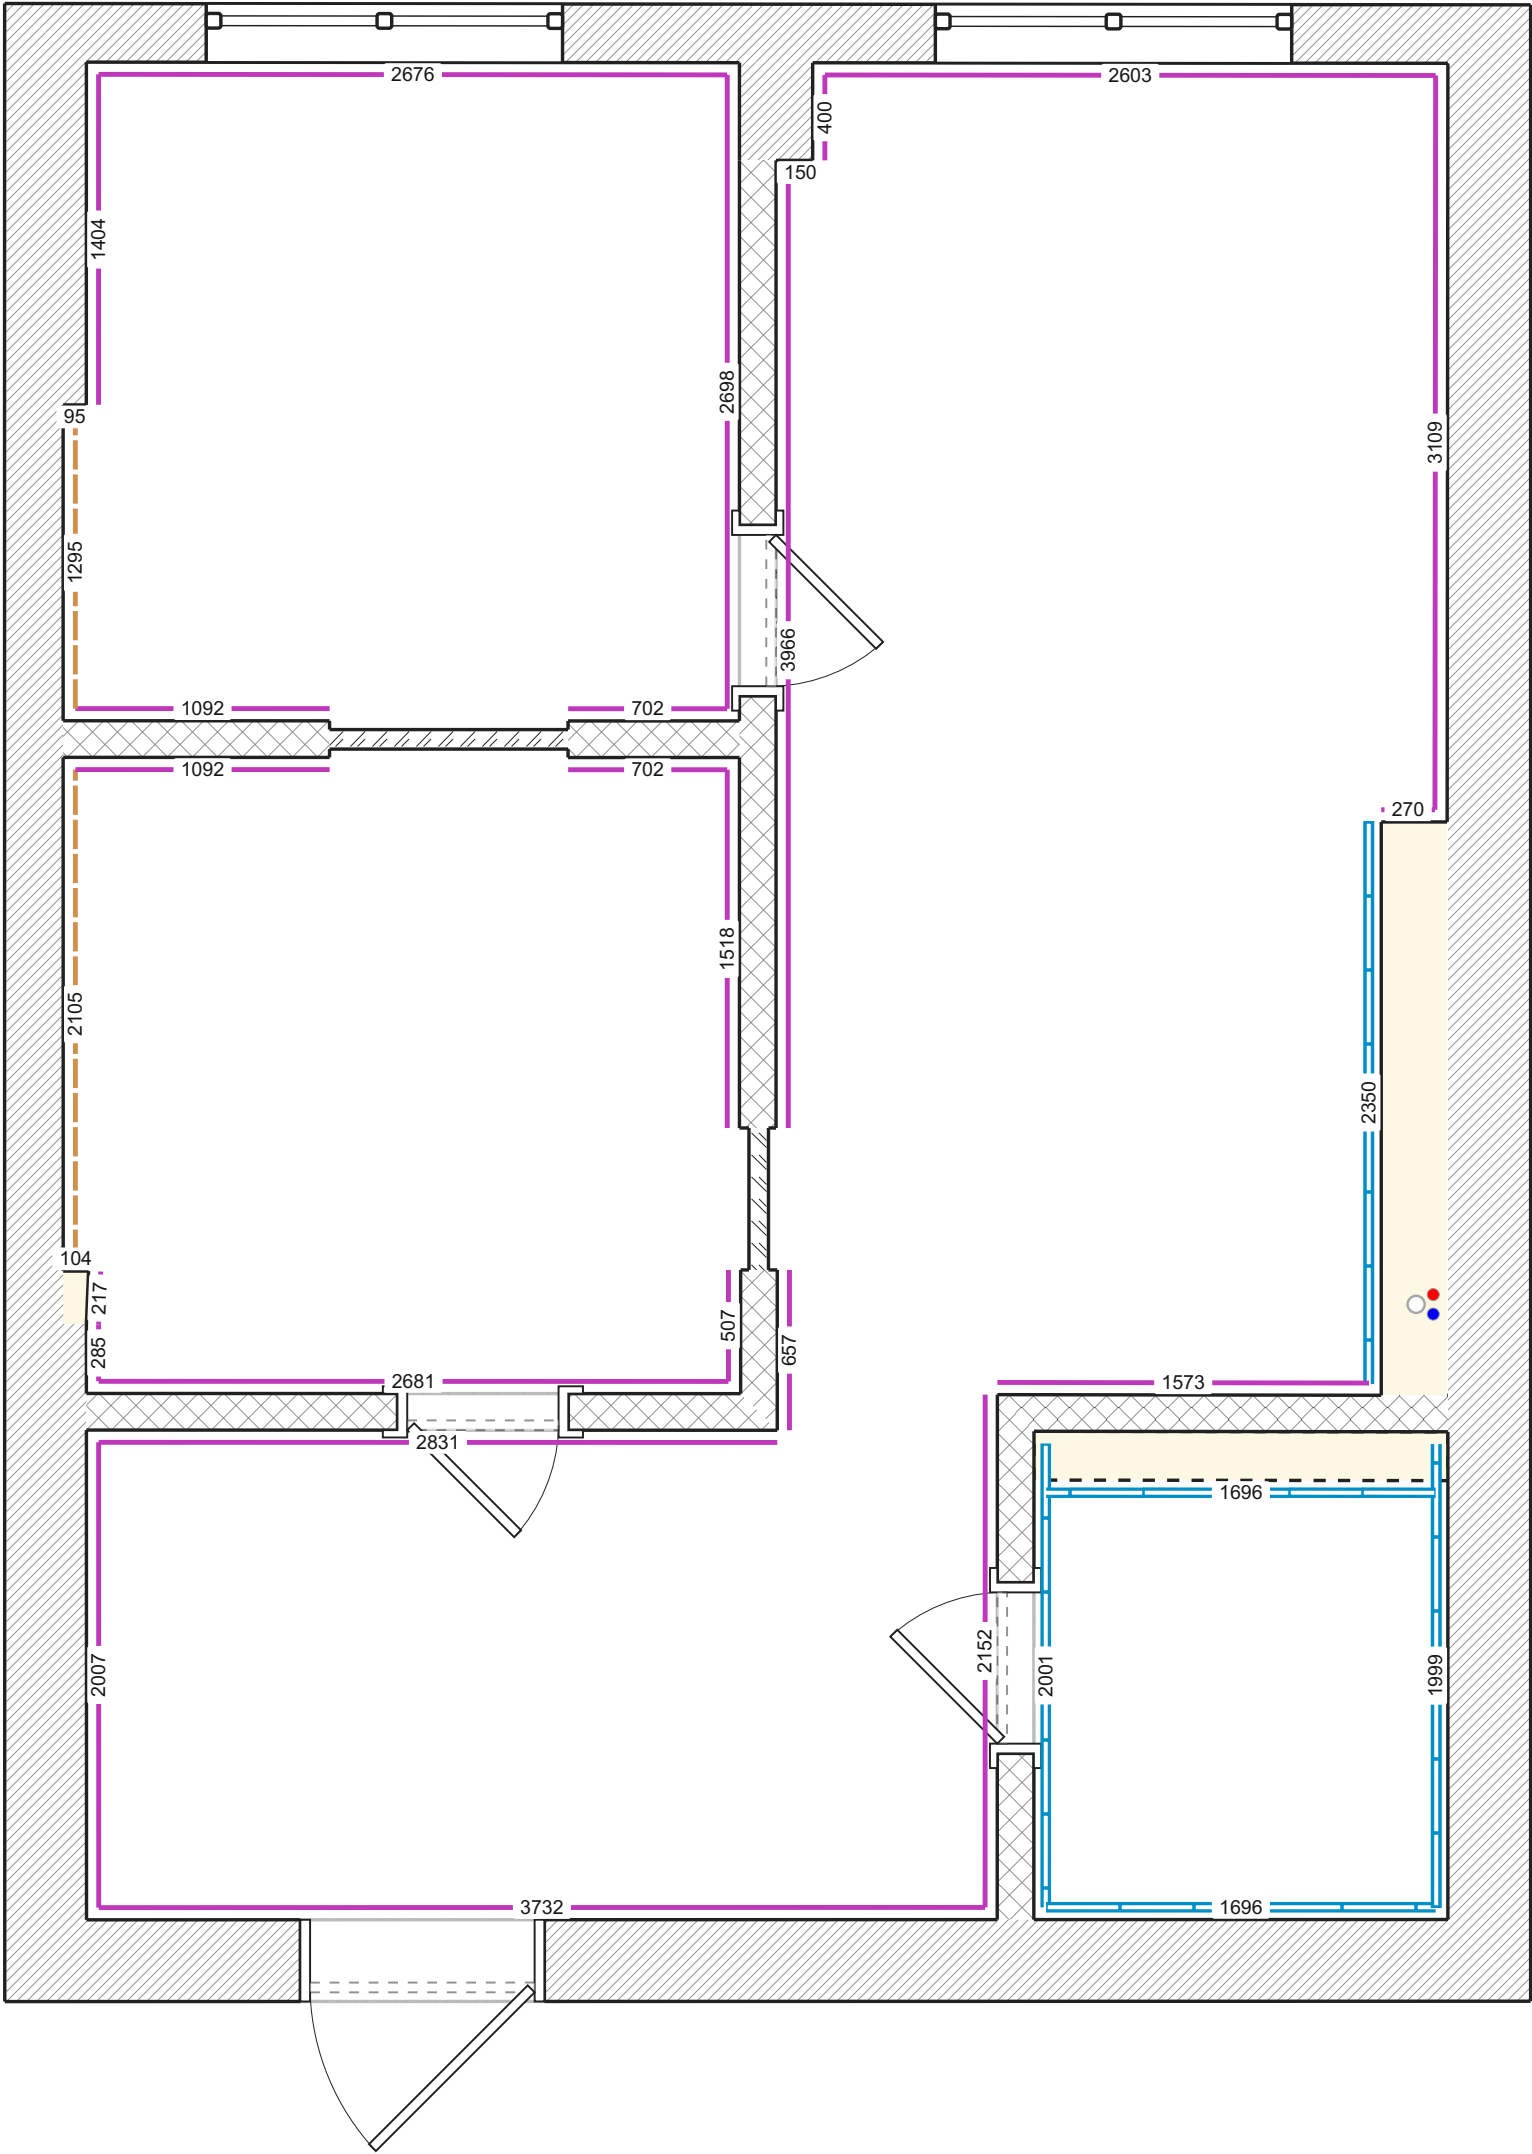

Потолки

Условные обозначения:


- Закарнизная ниша
- Потолок с теневым профилем
- Натяжной потолок (ткань)

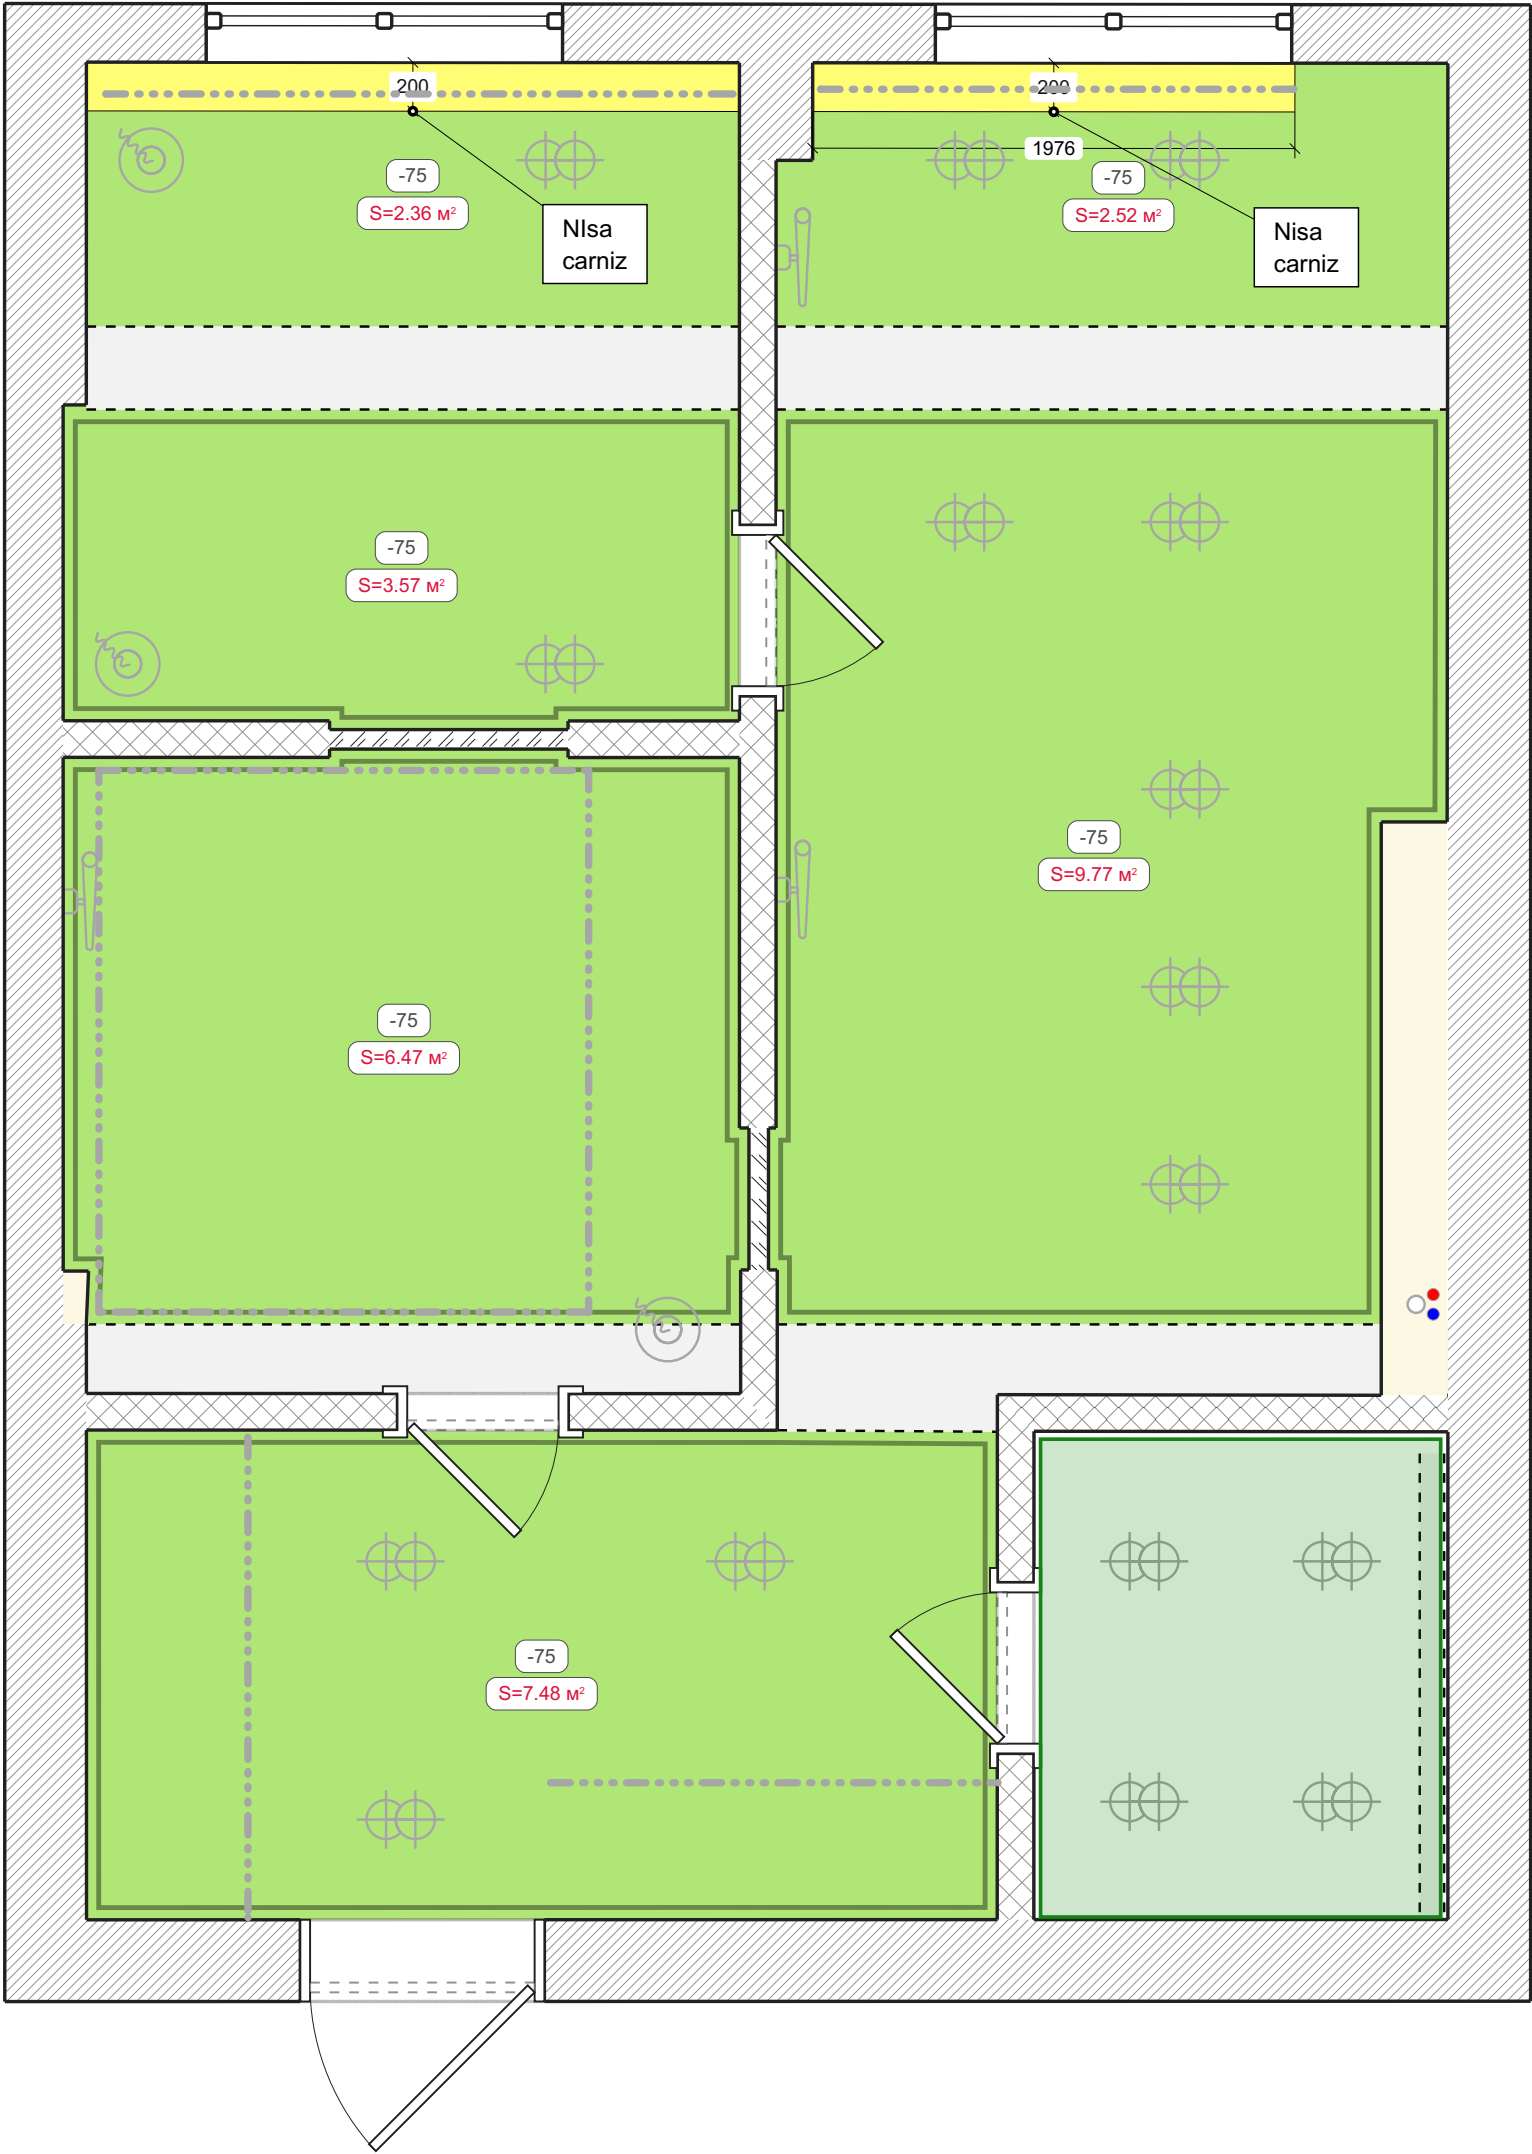


Гидроизоляция




Условные обозначения:

 Обмазочная гидроизоляция



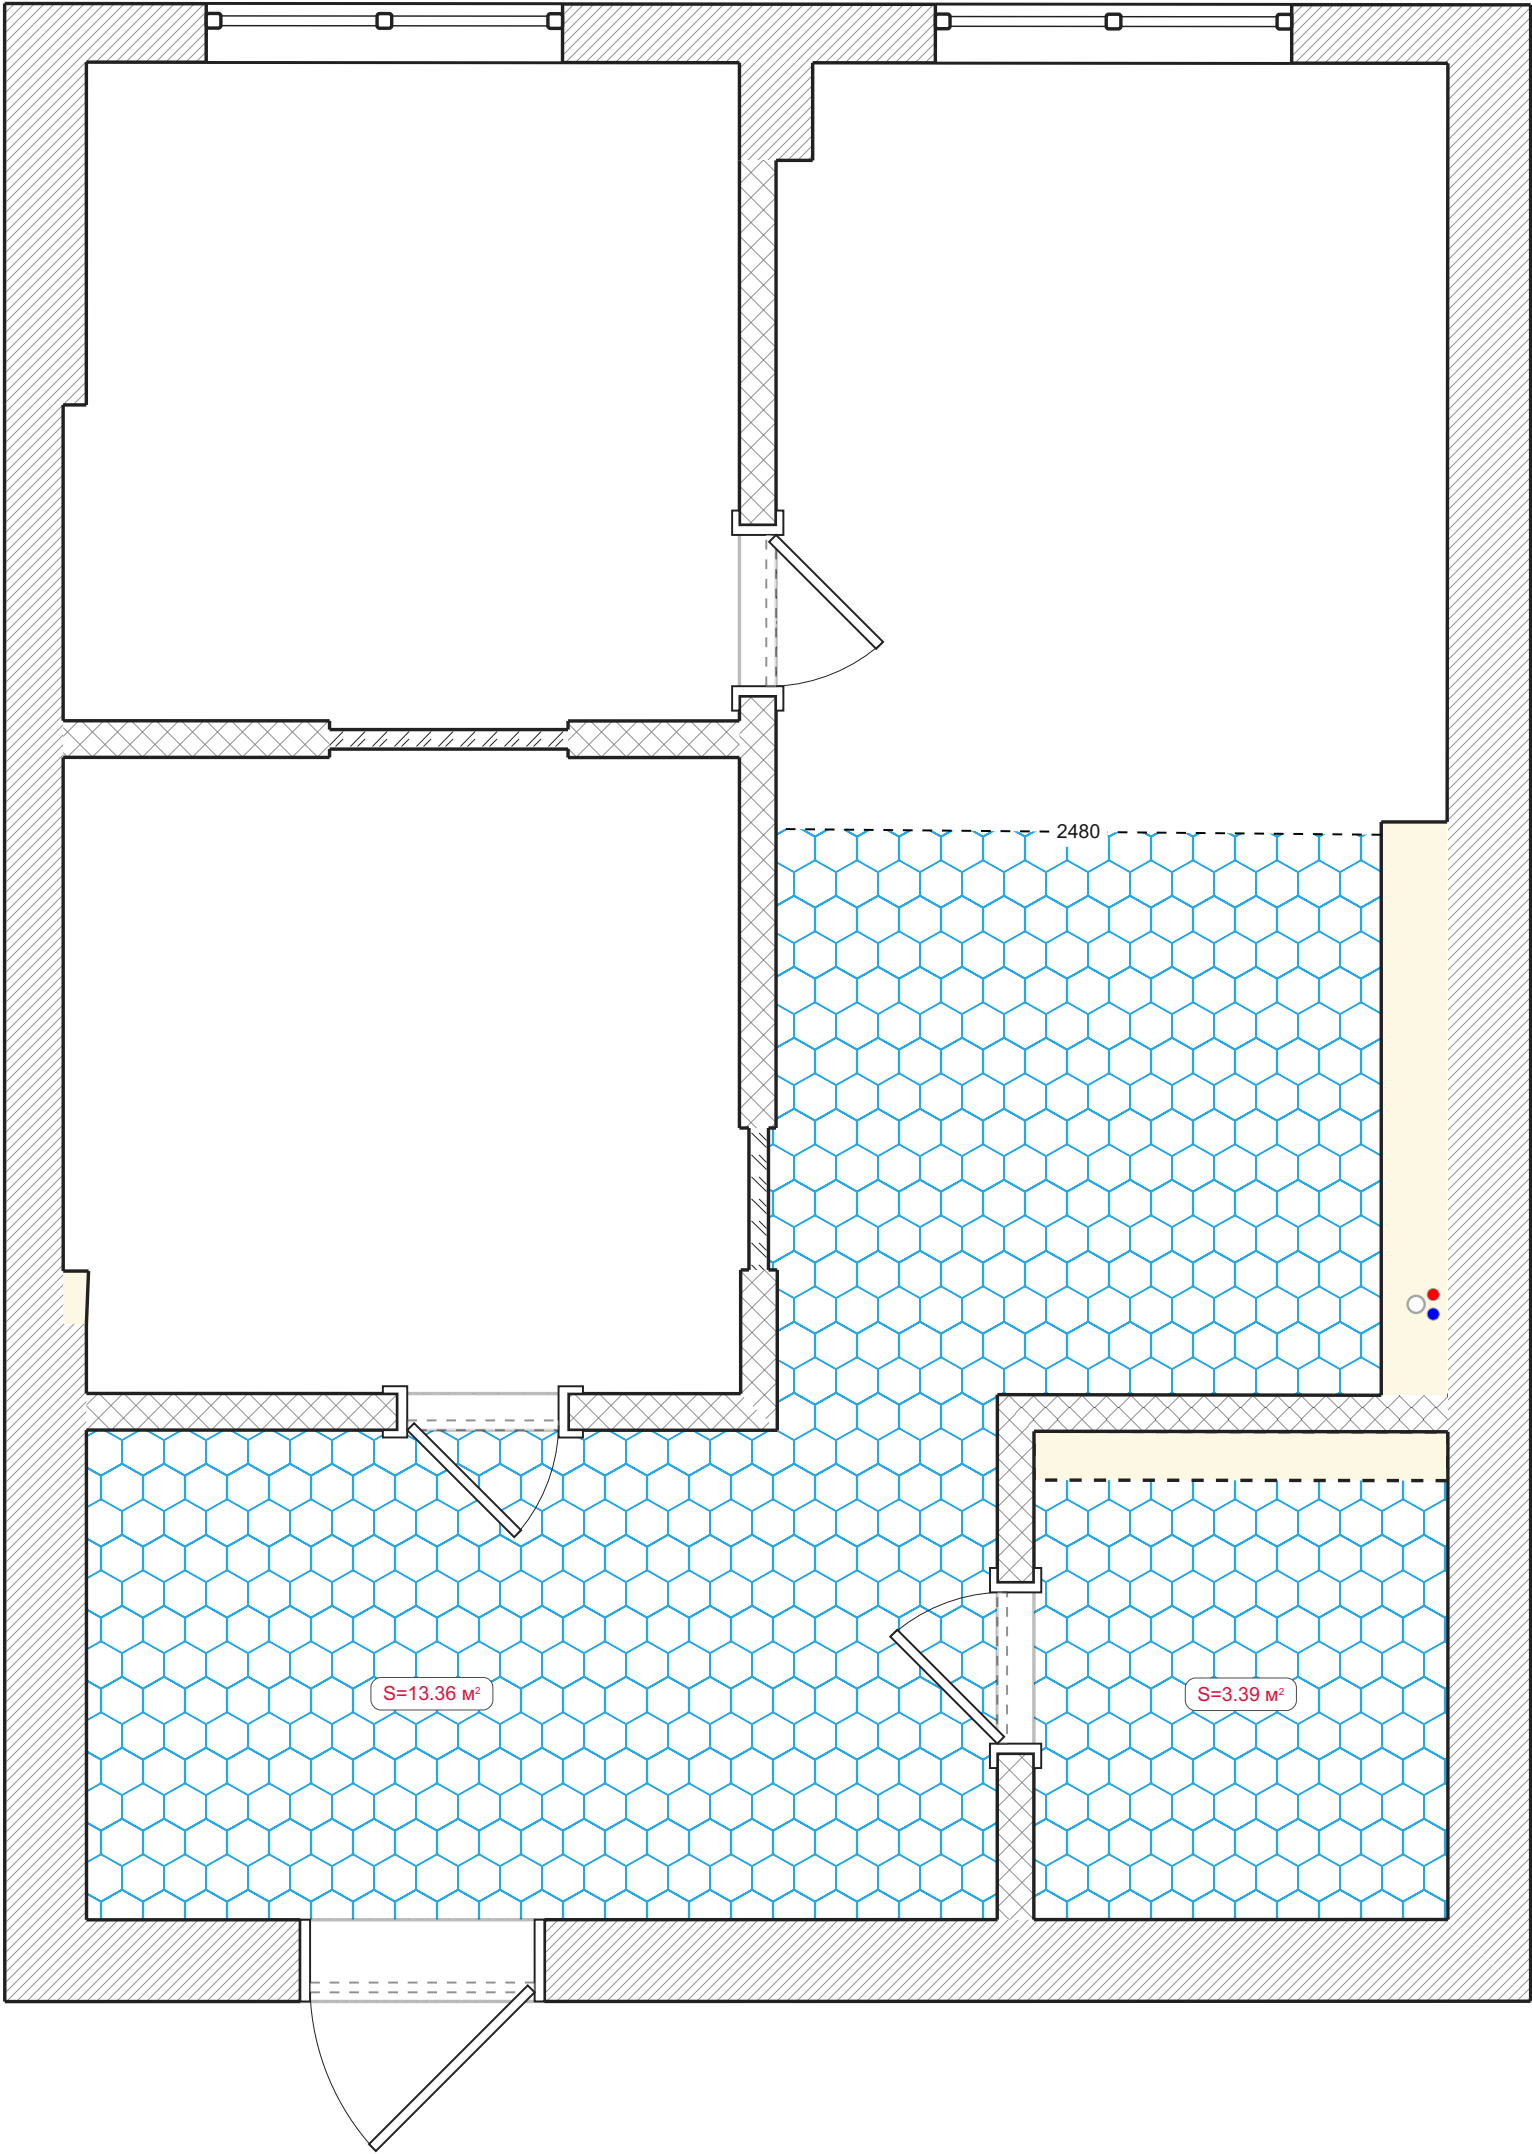


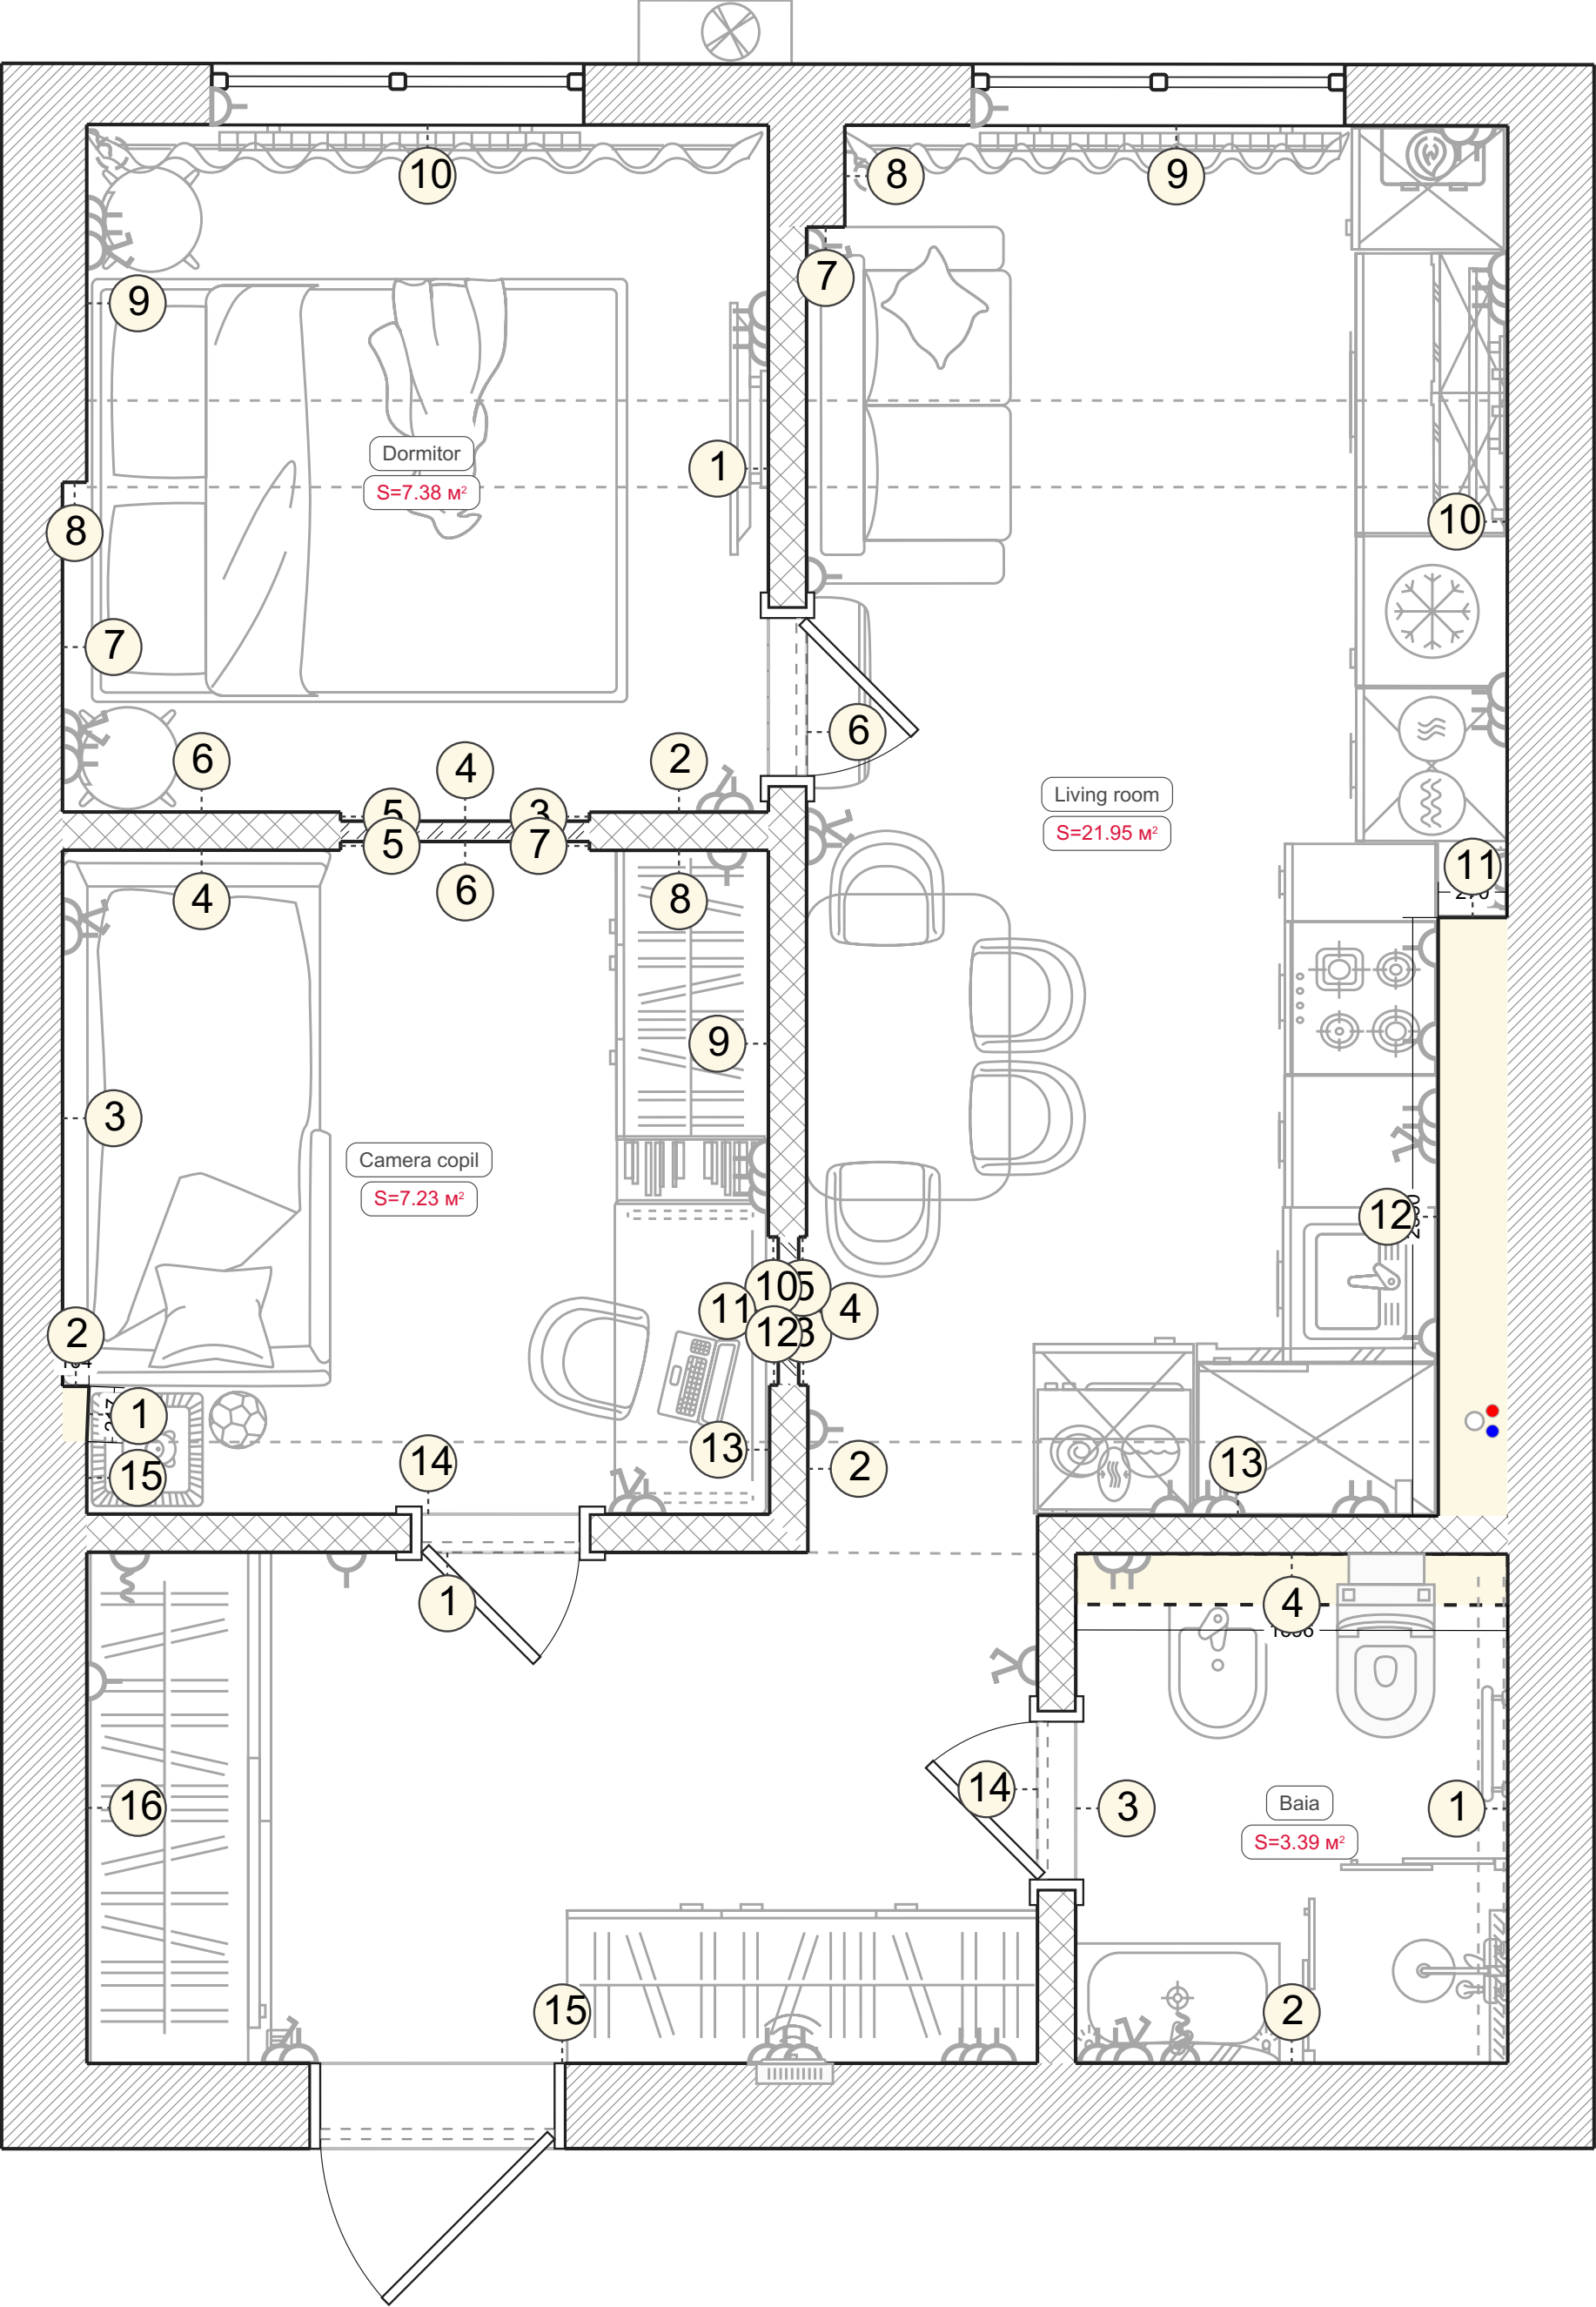



Развертки стен. Living room (1-16)

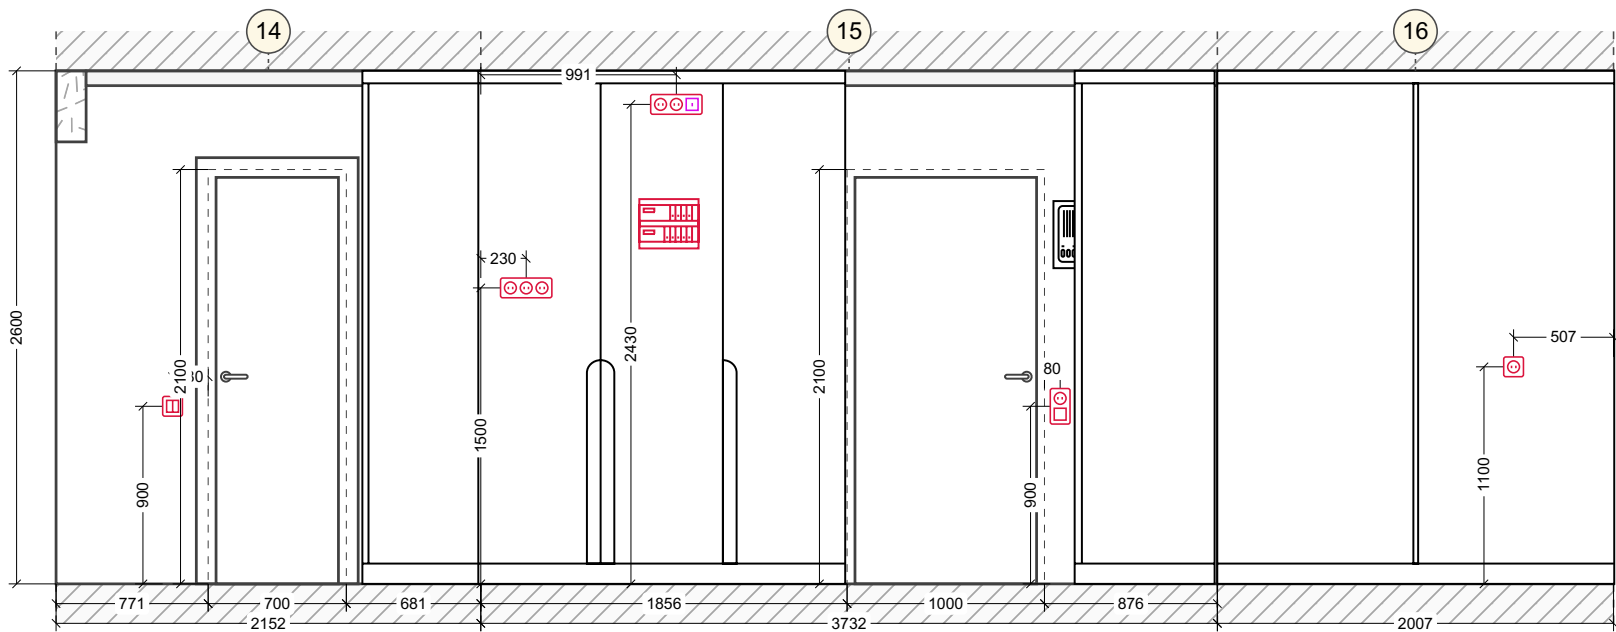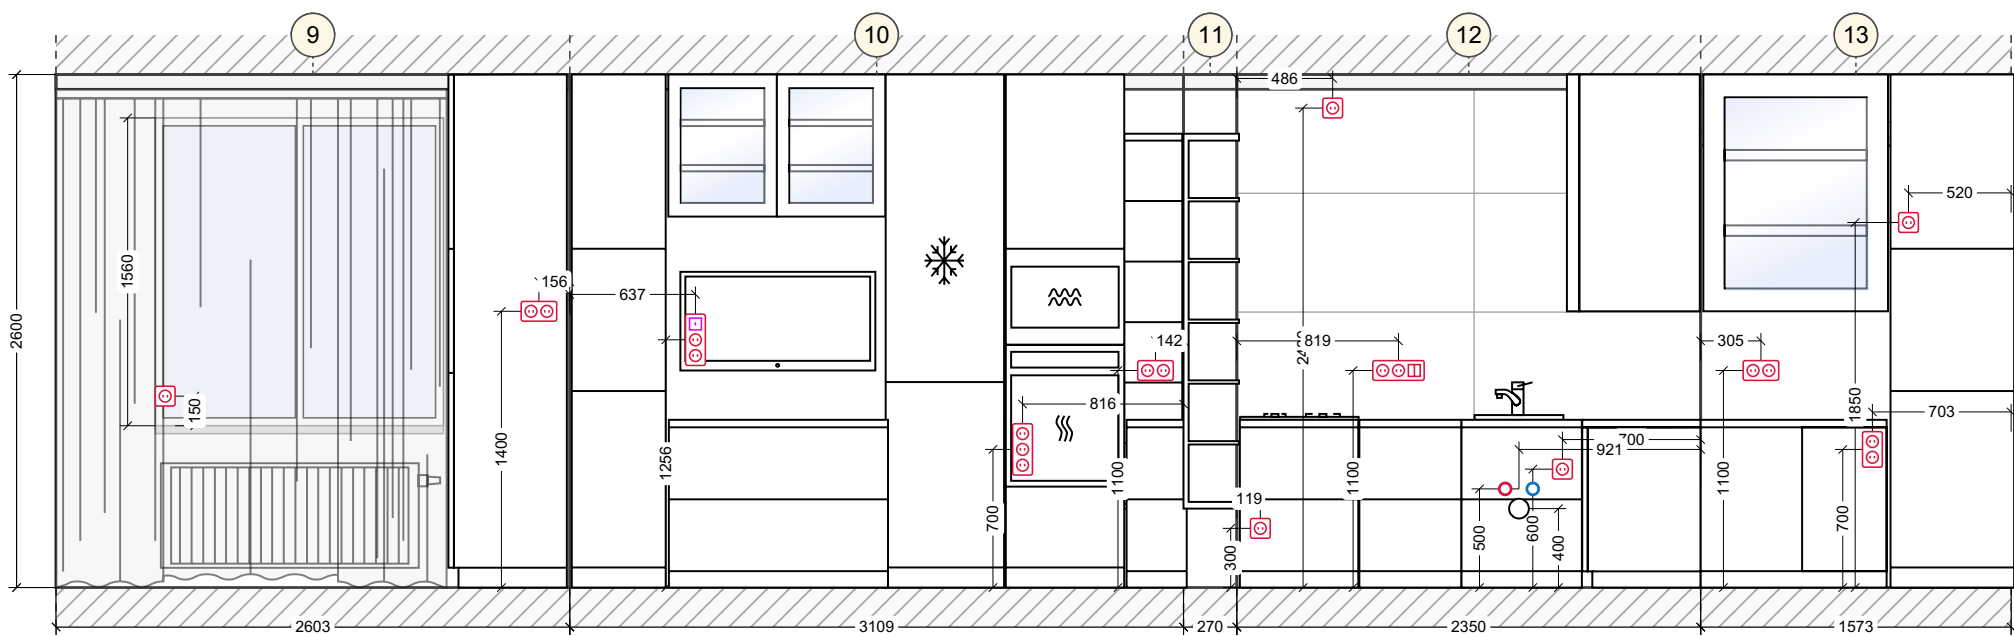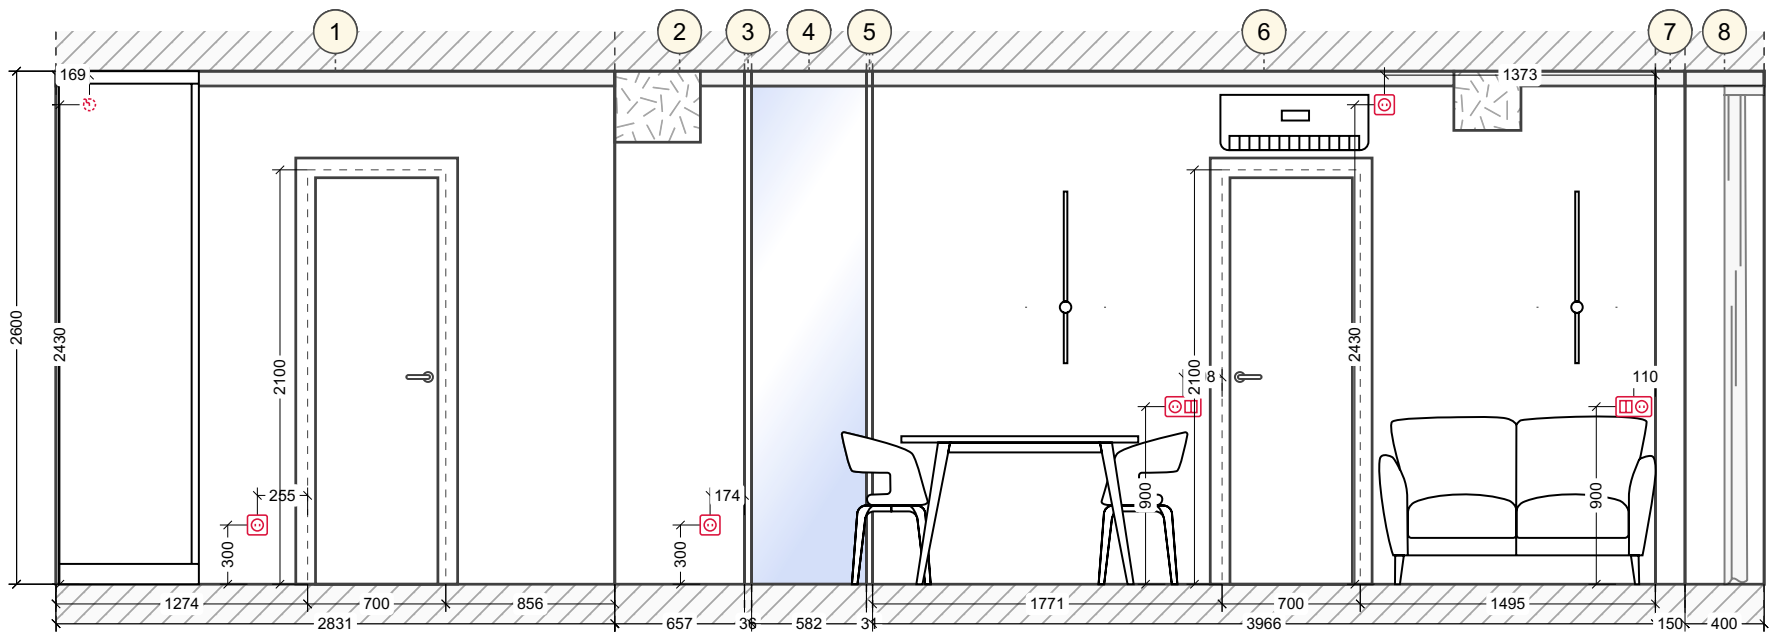



Развертки стен. Living room (1-16)

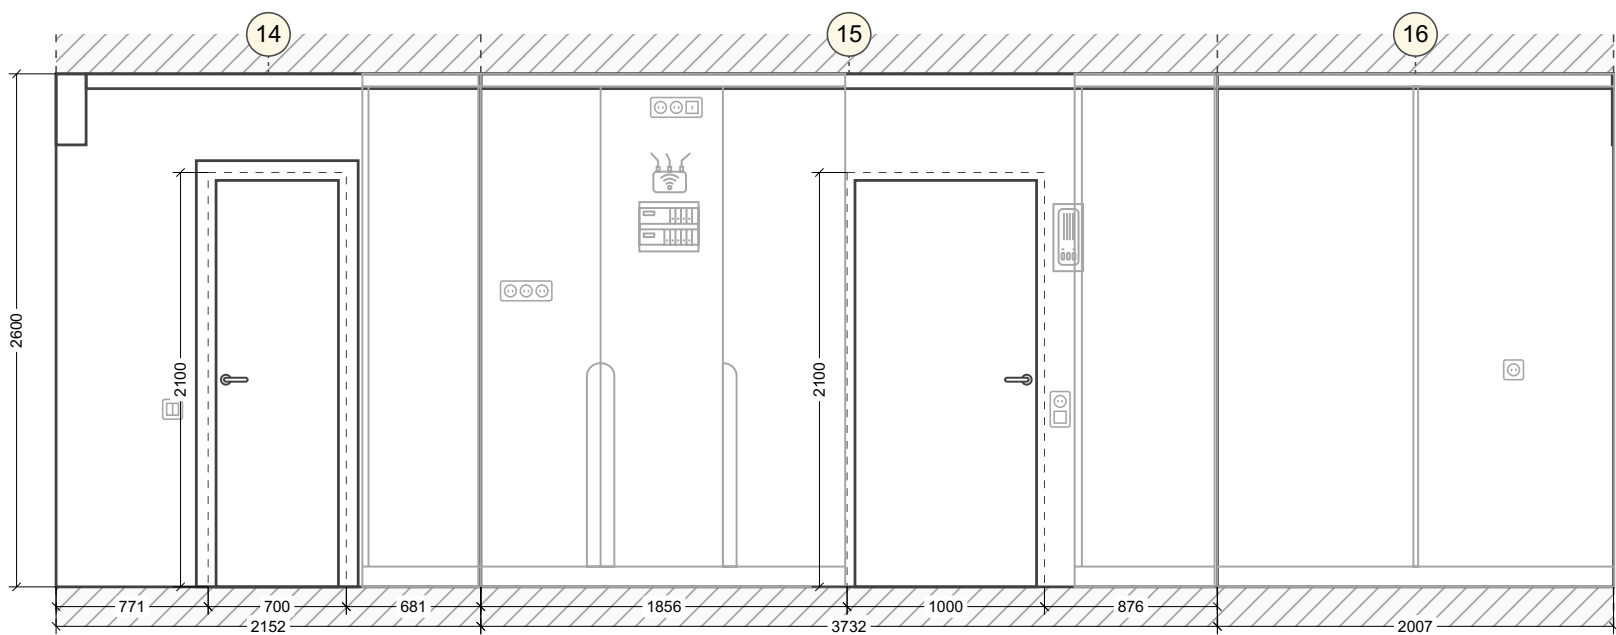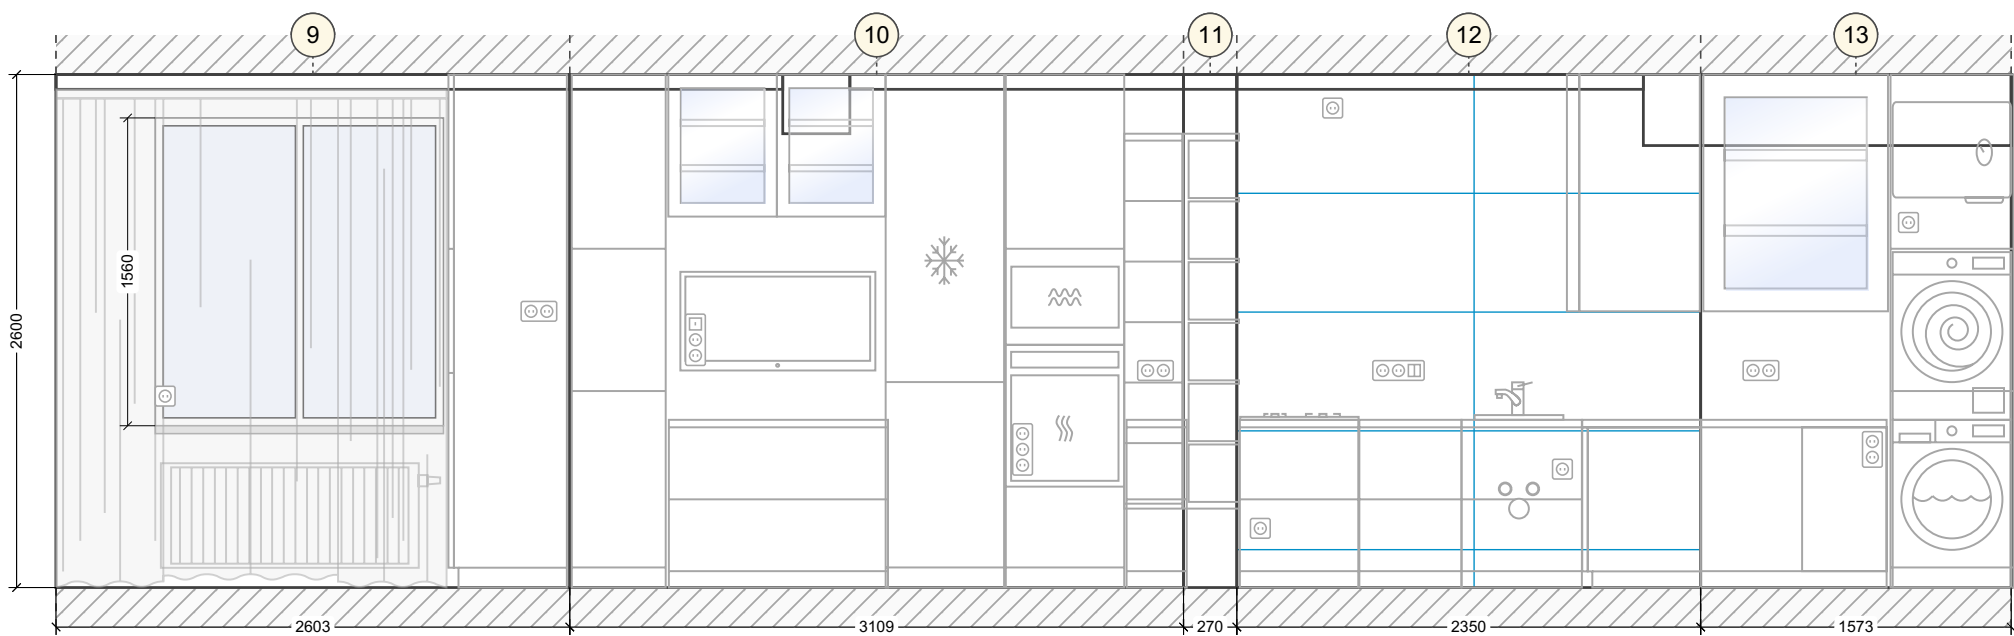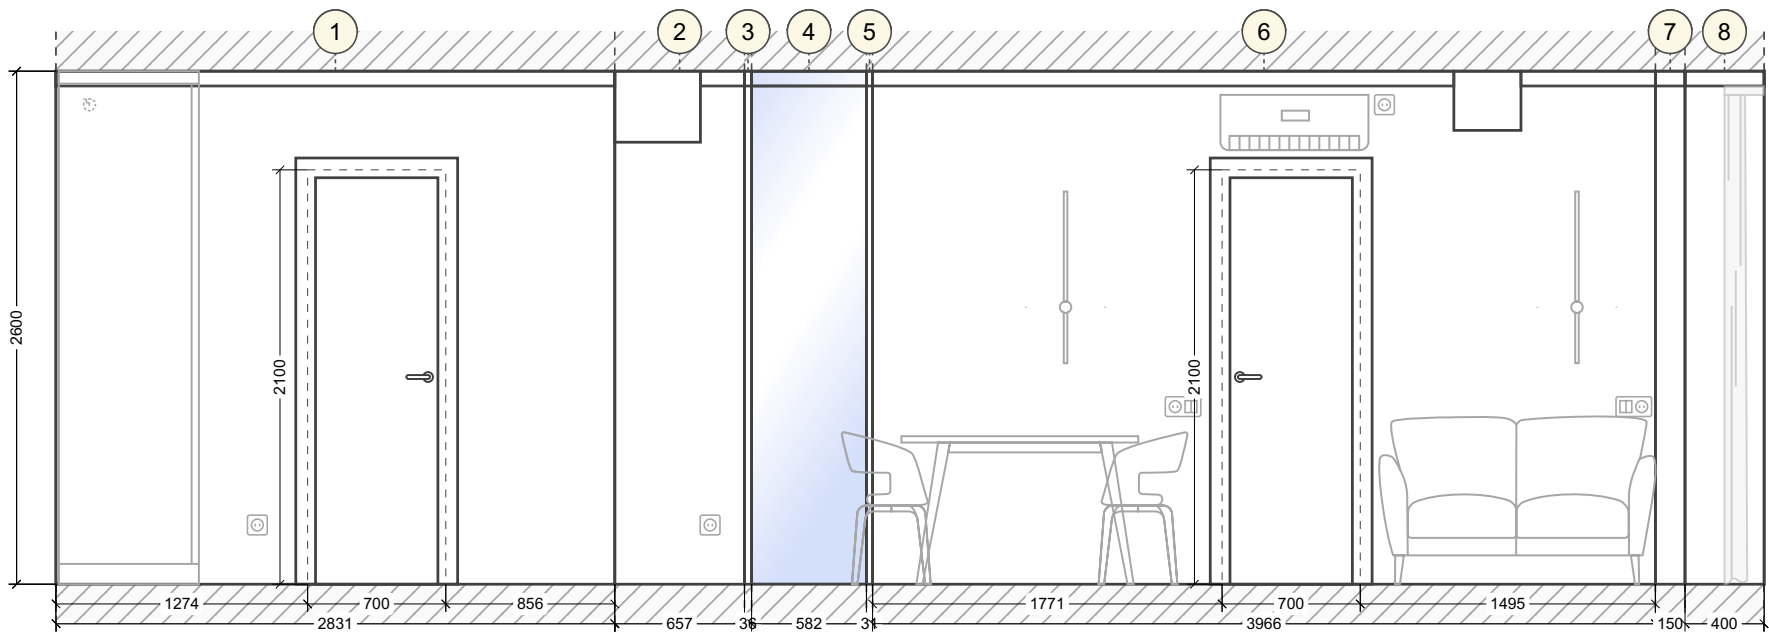

Развертки стен. Dormitor (1-10)

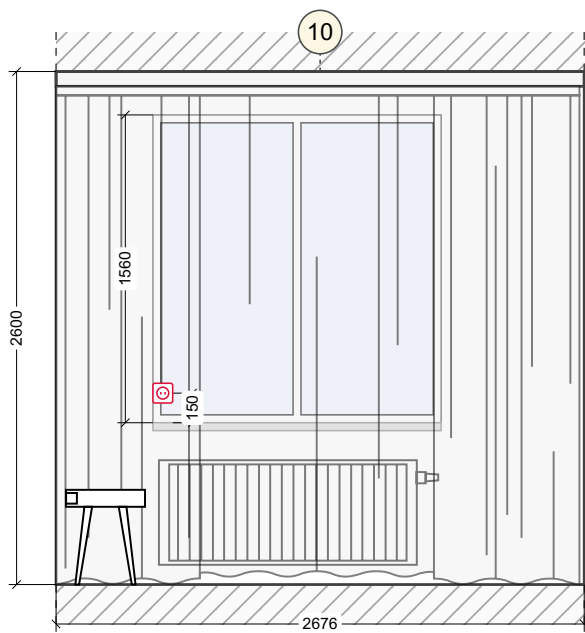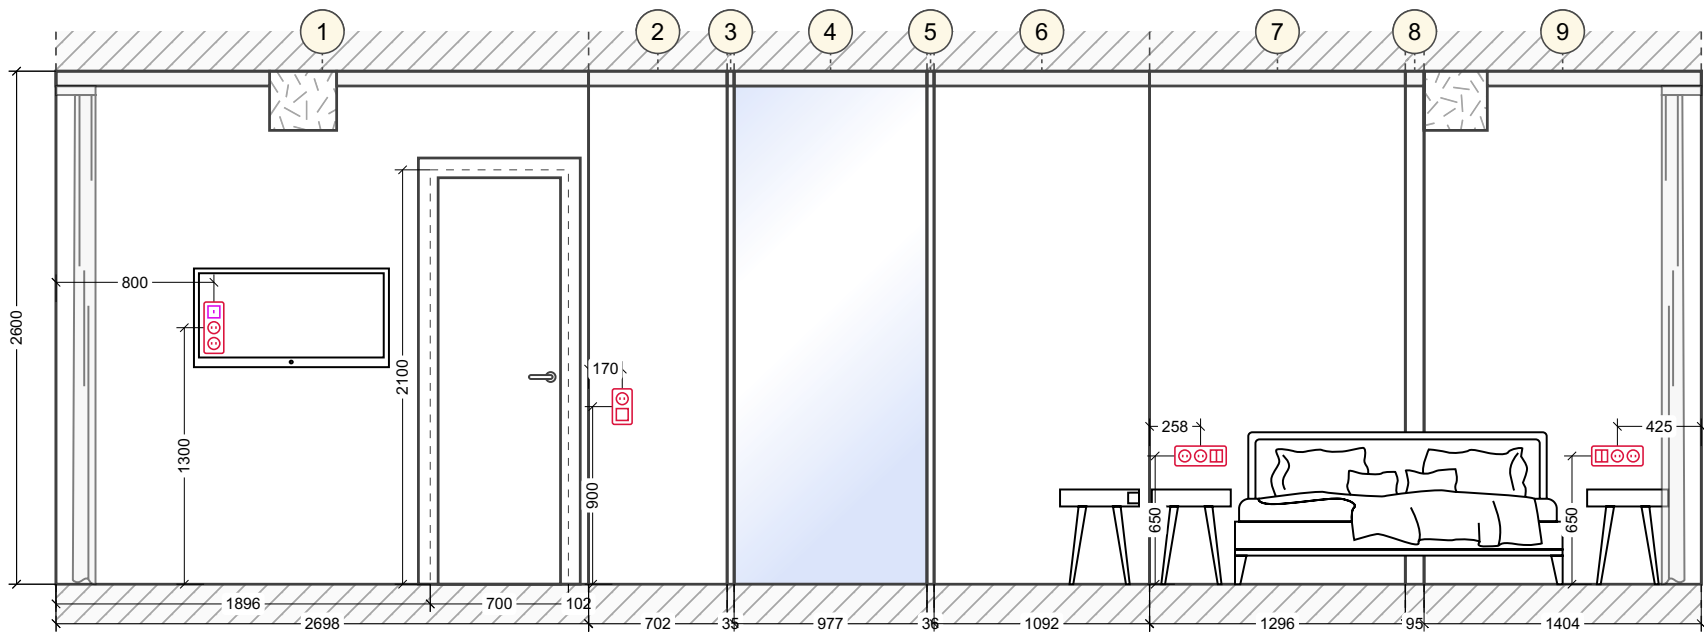

Развертки стен. Сатема copil (1-15)

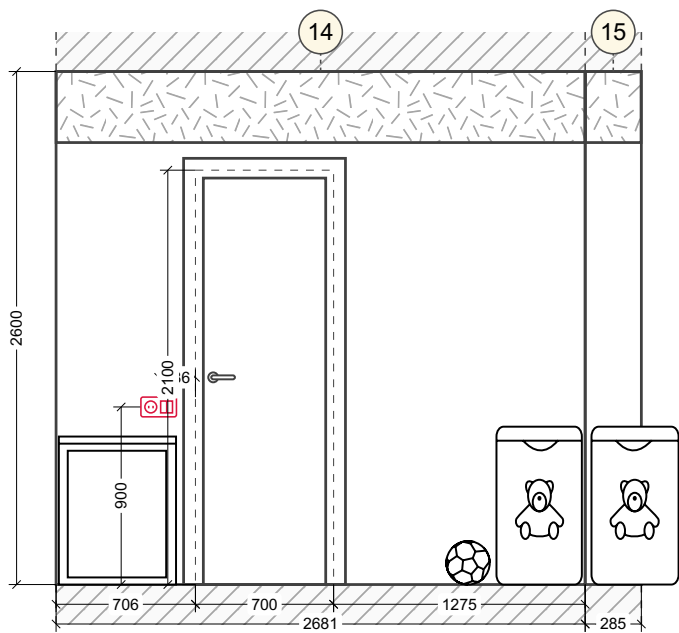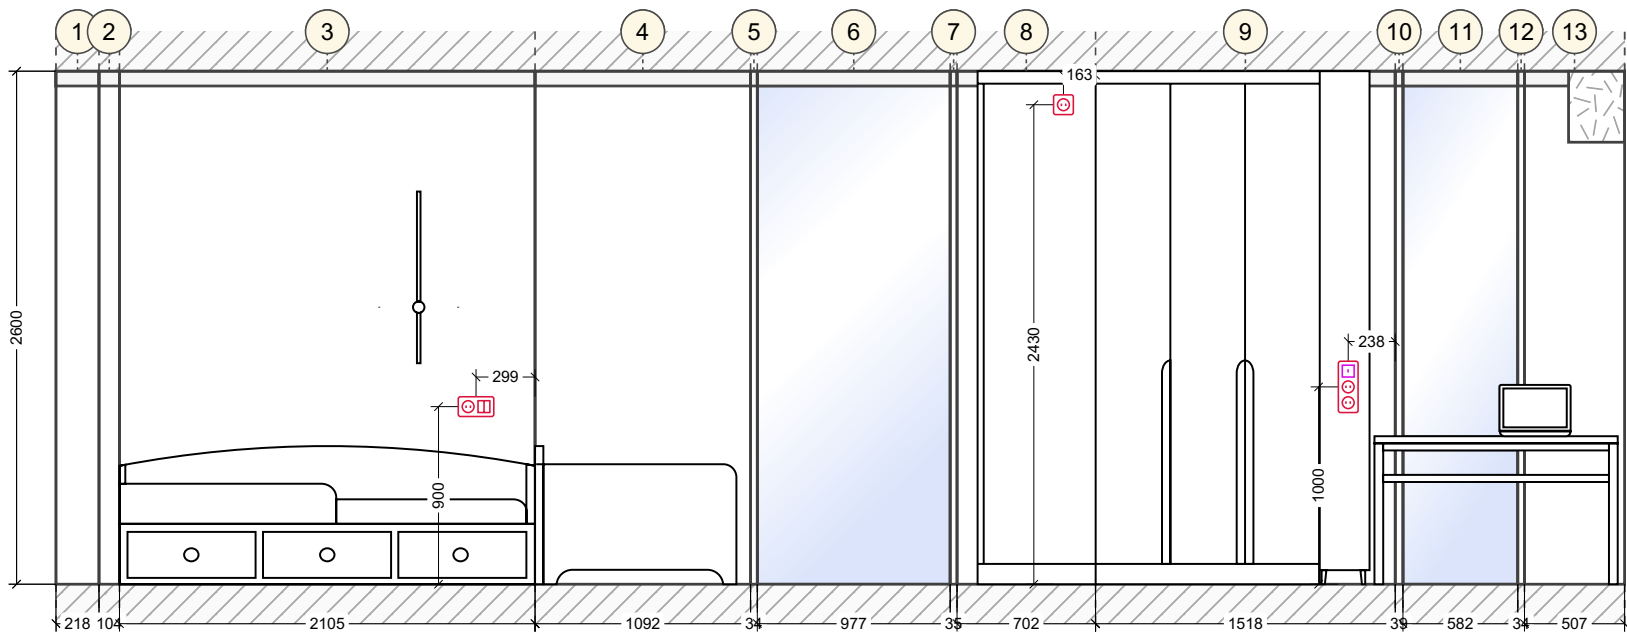

Развертки стен. Baia (1-4)

